



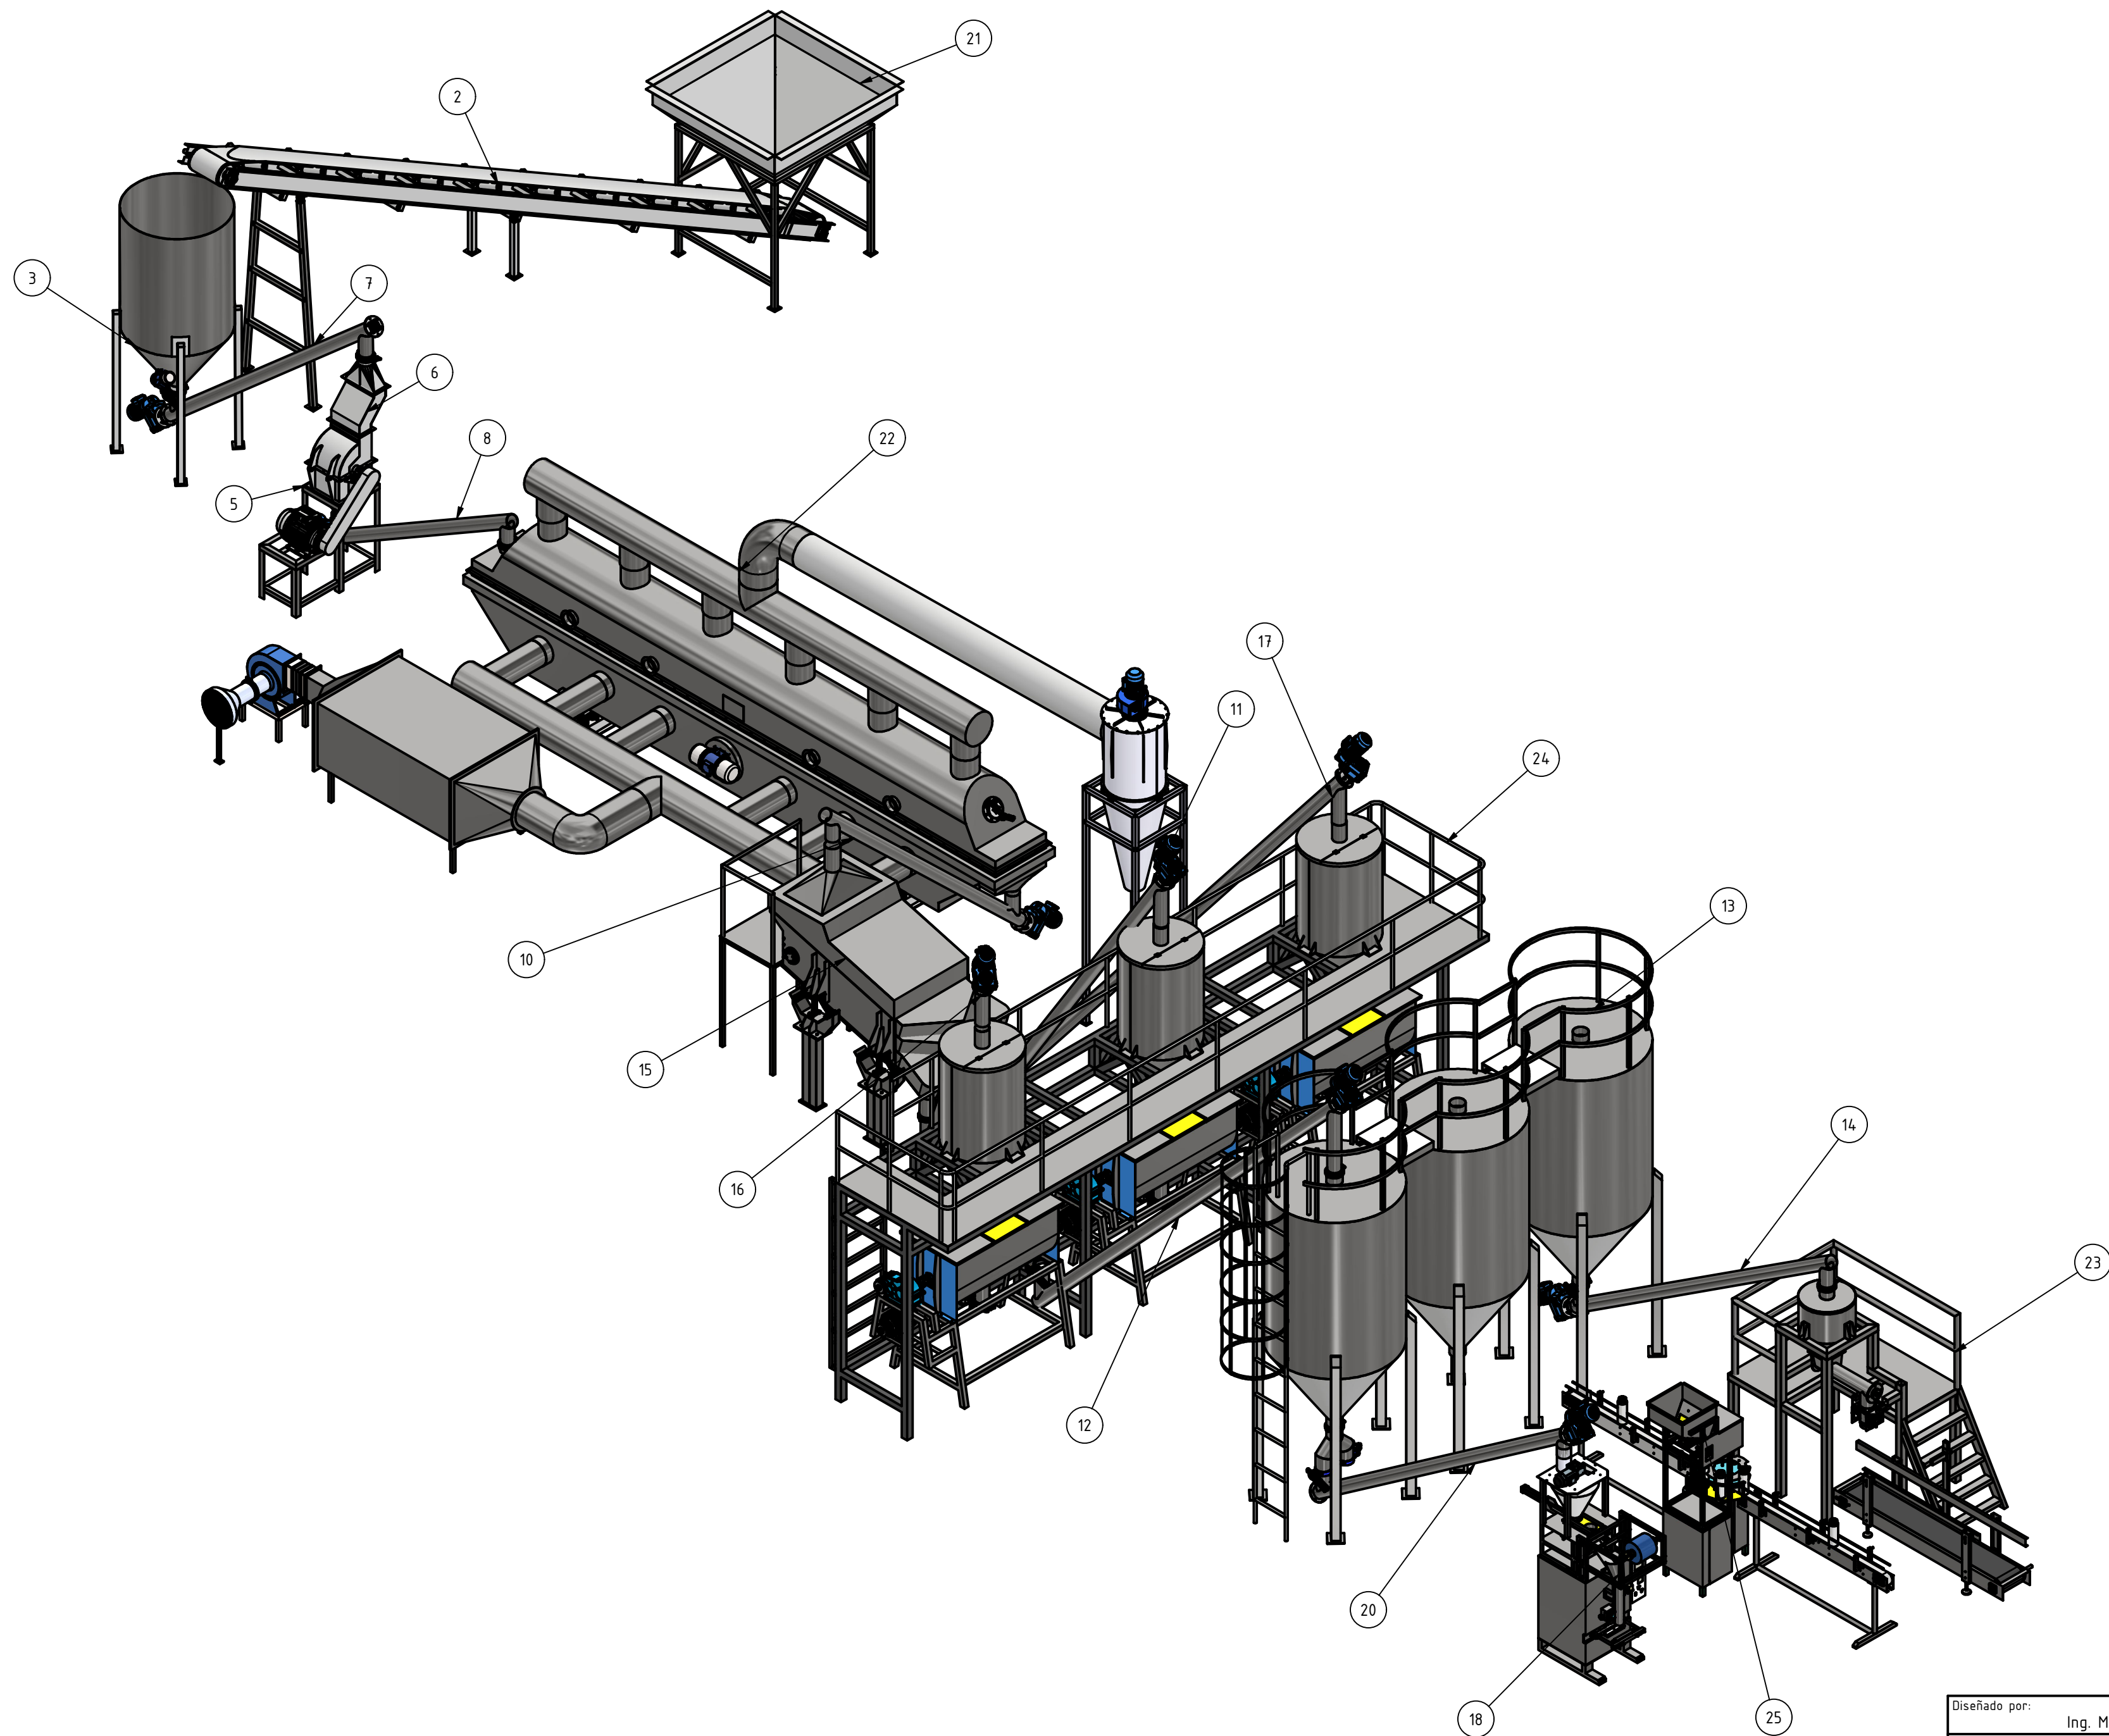

Lista de Partes			
ITEM	QTY	PART NUMBER	DESCRIPTION
1	1	PARTE ESTRUCTURAL PLANTA PROCESADORA DE SAL	
2	1	CINTA	
3	1	TOLVA 1	
5	1	MOLINO DOBLE	
6	1	TRAMPRA Y BY	
7	1	HELICOIDAL 3500MM	
8	1	H4000MM2	
10	1	H4000MM3	
11	1	H4000MM5	
12	1	HEL5500MM1	
13	1	Ensamblaje Final	
14	1	H4500MM6	
15	1	Ensamble Final	
16	1	H4500MM7	
17	1	H4500MM8	
18	1	SACHETADORA VOLUMETRICA 1000 Gr.	
20	1	H4500MM9	
21	1	TOLVA DE RECECION TR	
22	1	SECADOR LECHO FLUIDISADO	
23	1	Ensayadora Semi - Automática	
24	1	MEZCLADOR-ACUMULADOR A	
25	1	DOSIFICADOR CONTINUO DE POTES	

Diseñado por:		Revisado por:		Aprobado por:		Fecha		
Ing. Maguiber O		Ing. Roger Zeballos F.				7/8/2024		
Descr.:		Proyecto:						
Cant.: 1 pz. Mat.:								
		PLANTA DE SAL ENSAMBLE				A2	Plano 1 de 1	

 