



DETALLE CONSTRUCTIVO-TABLEROS DE DISTRIBUCION PRINCIPALES

TABLERO DISTRIBUCION GENERAL

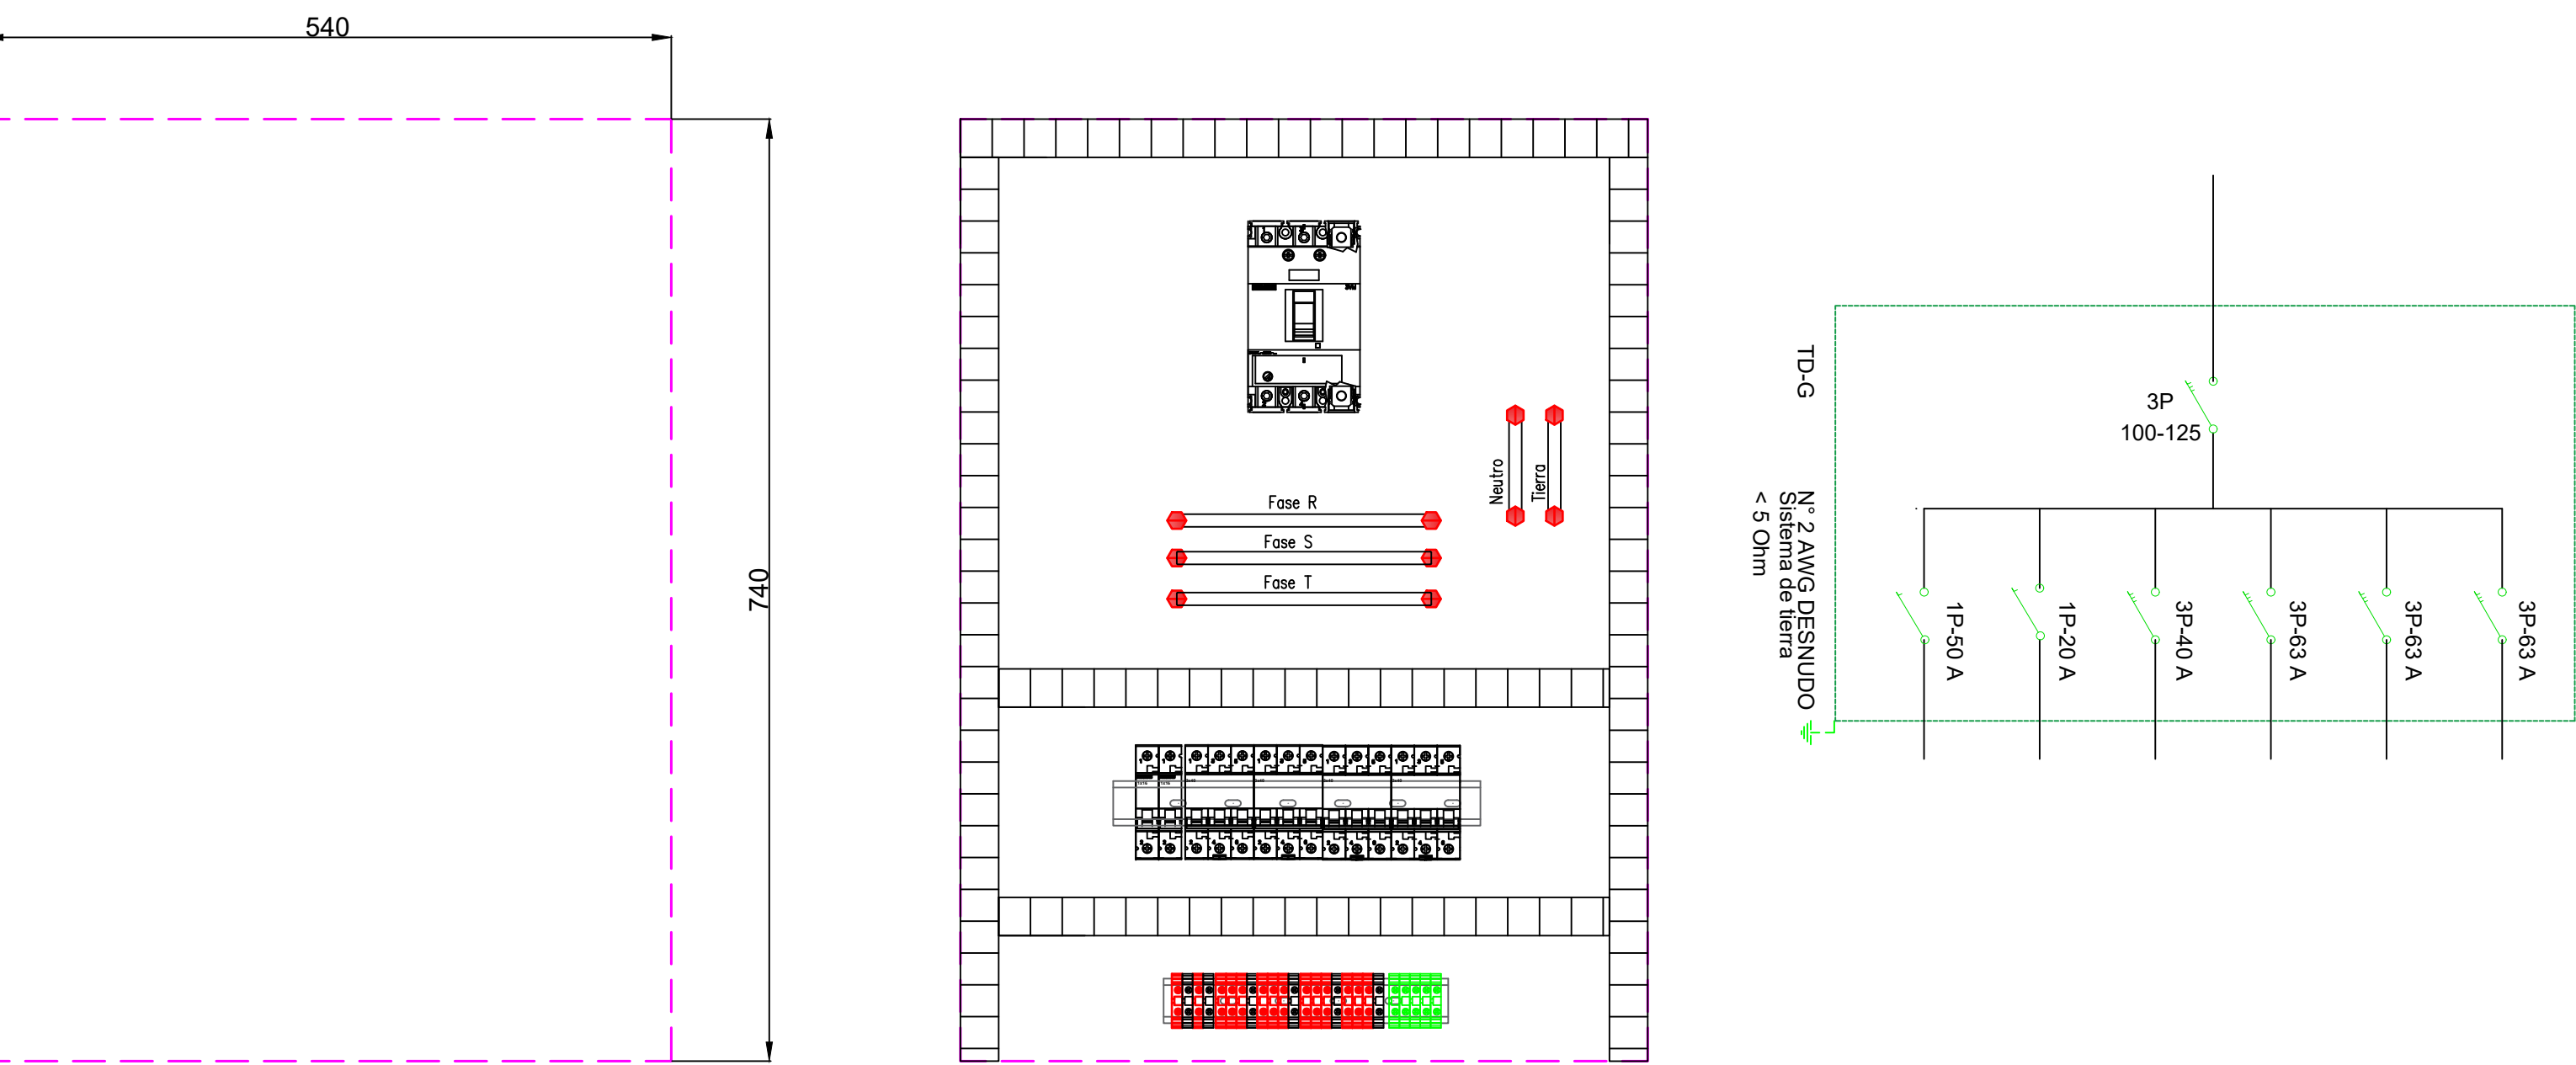


TABLERO PRINCIPAL 01

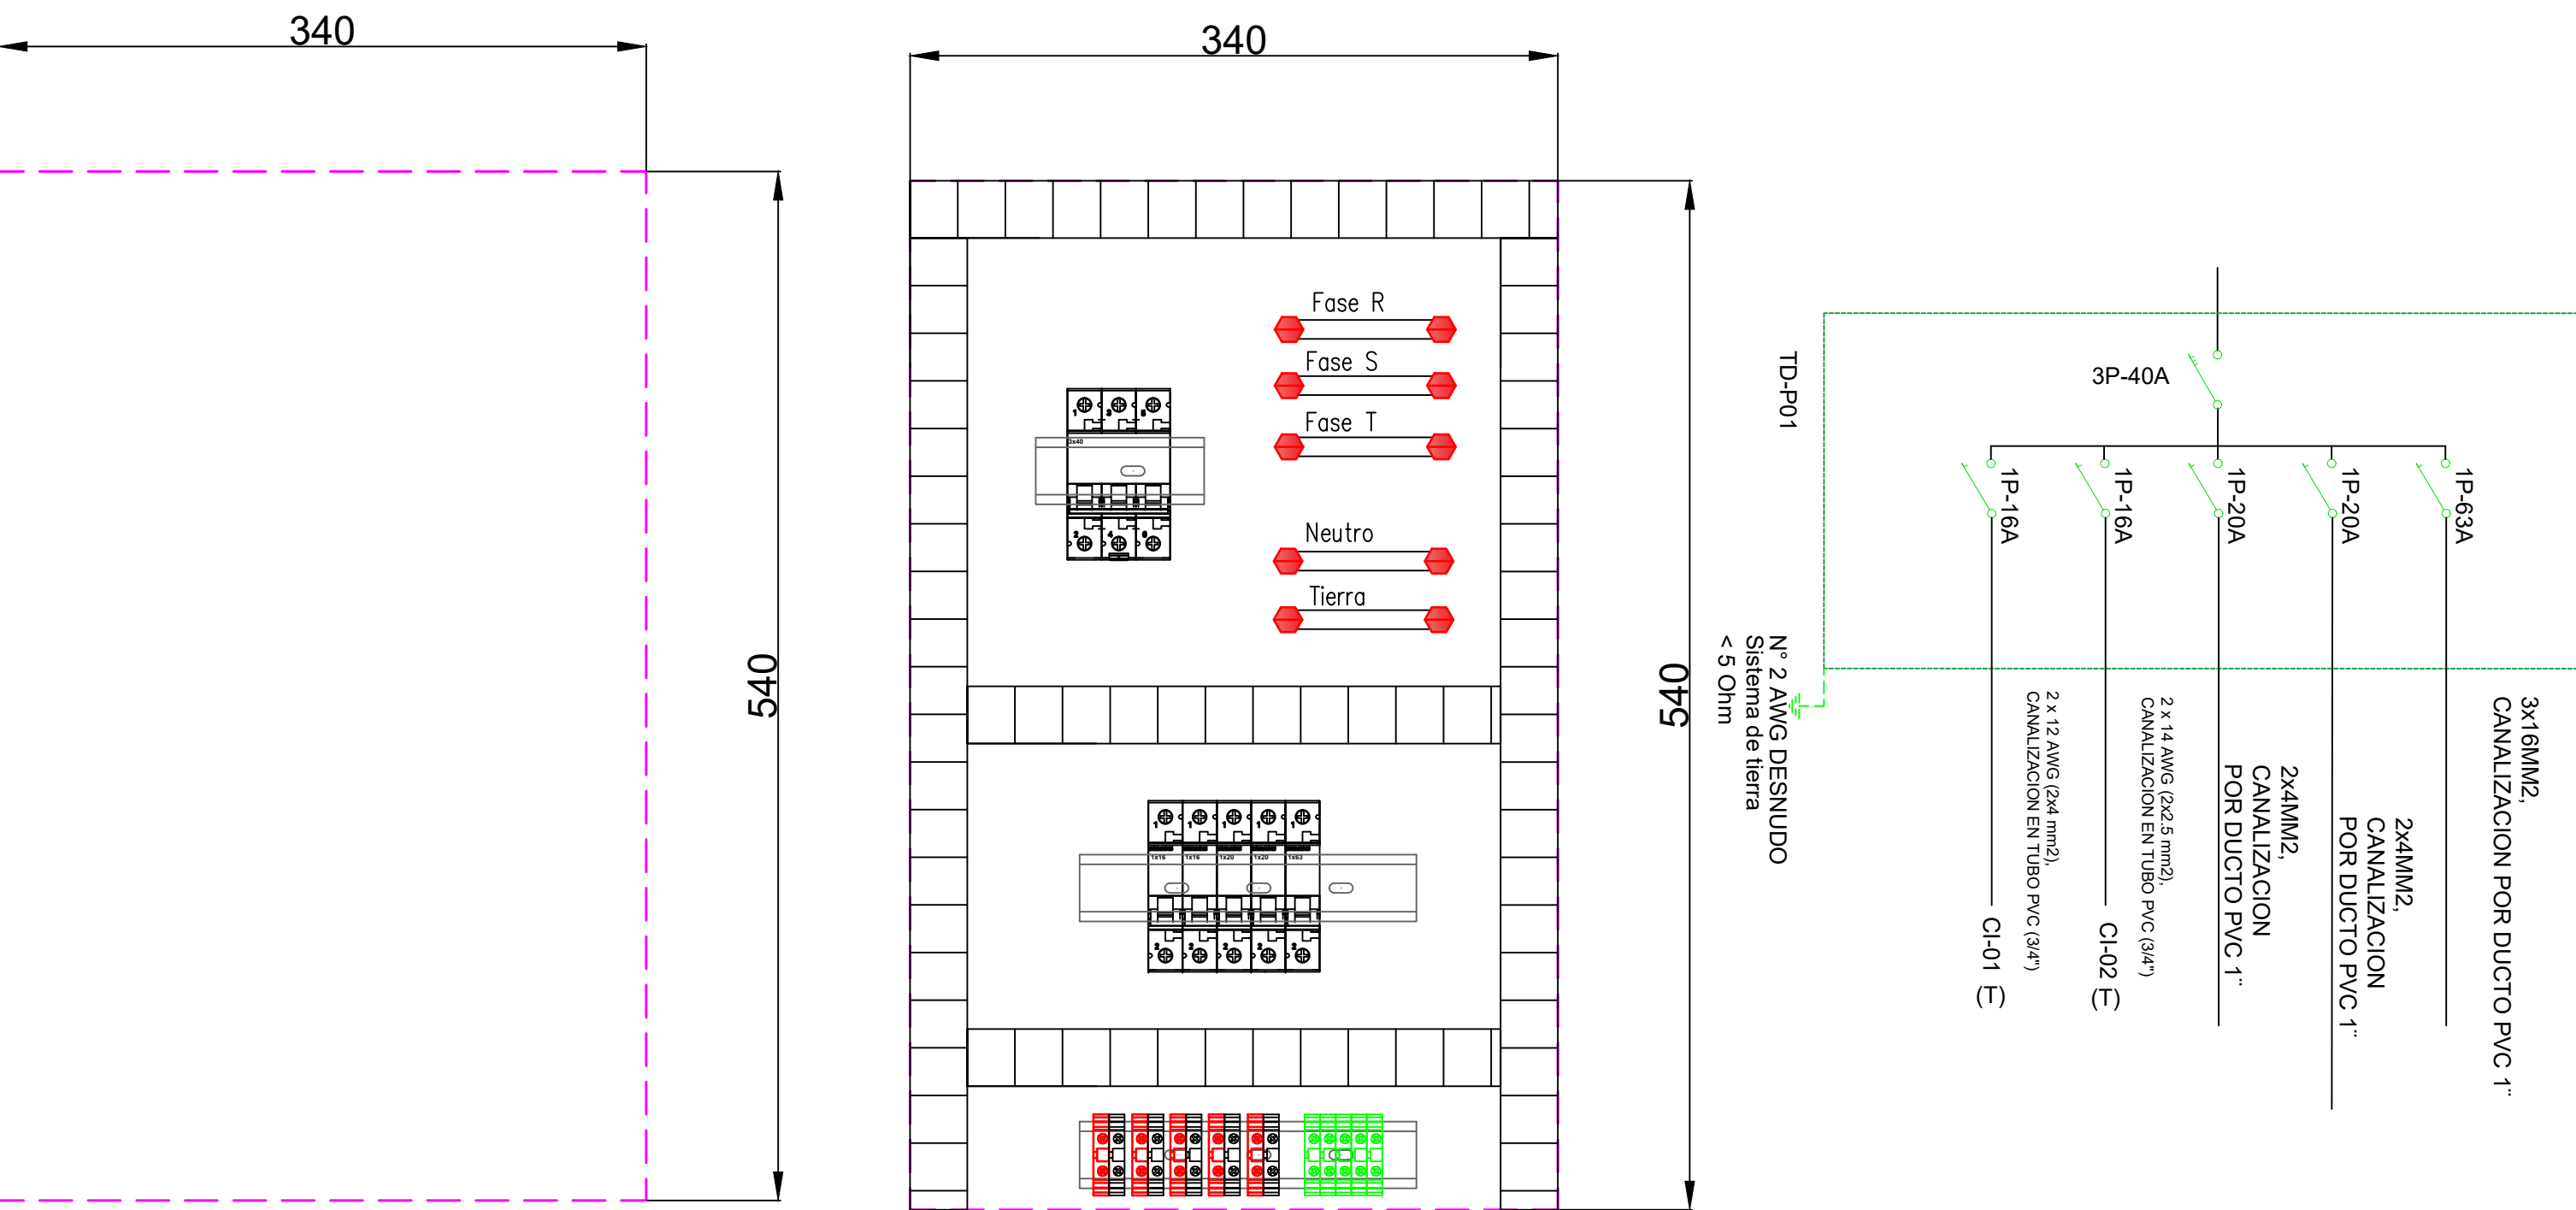


SIMBOLOGÍA	DESCRIPCIÓN
	Interruptor termomagnético tripolar
	Interruptor termomagnético monopolar
	Interruptor diferencial


TABLERO PRINCIPAL 02

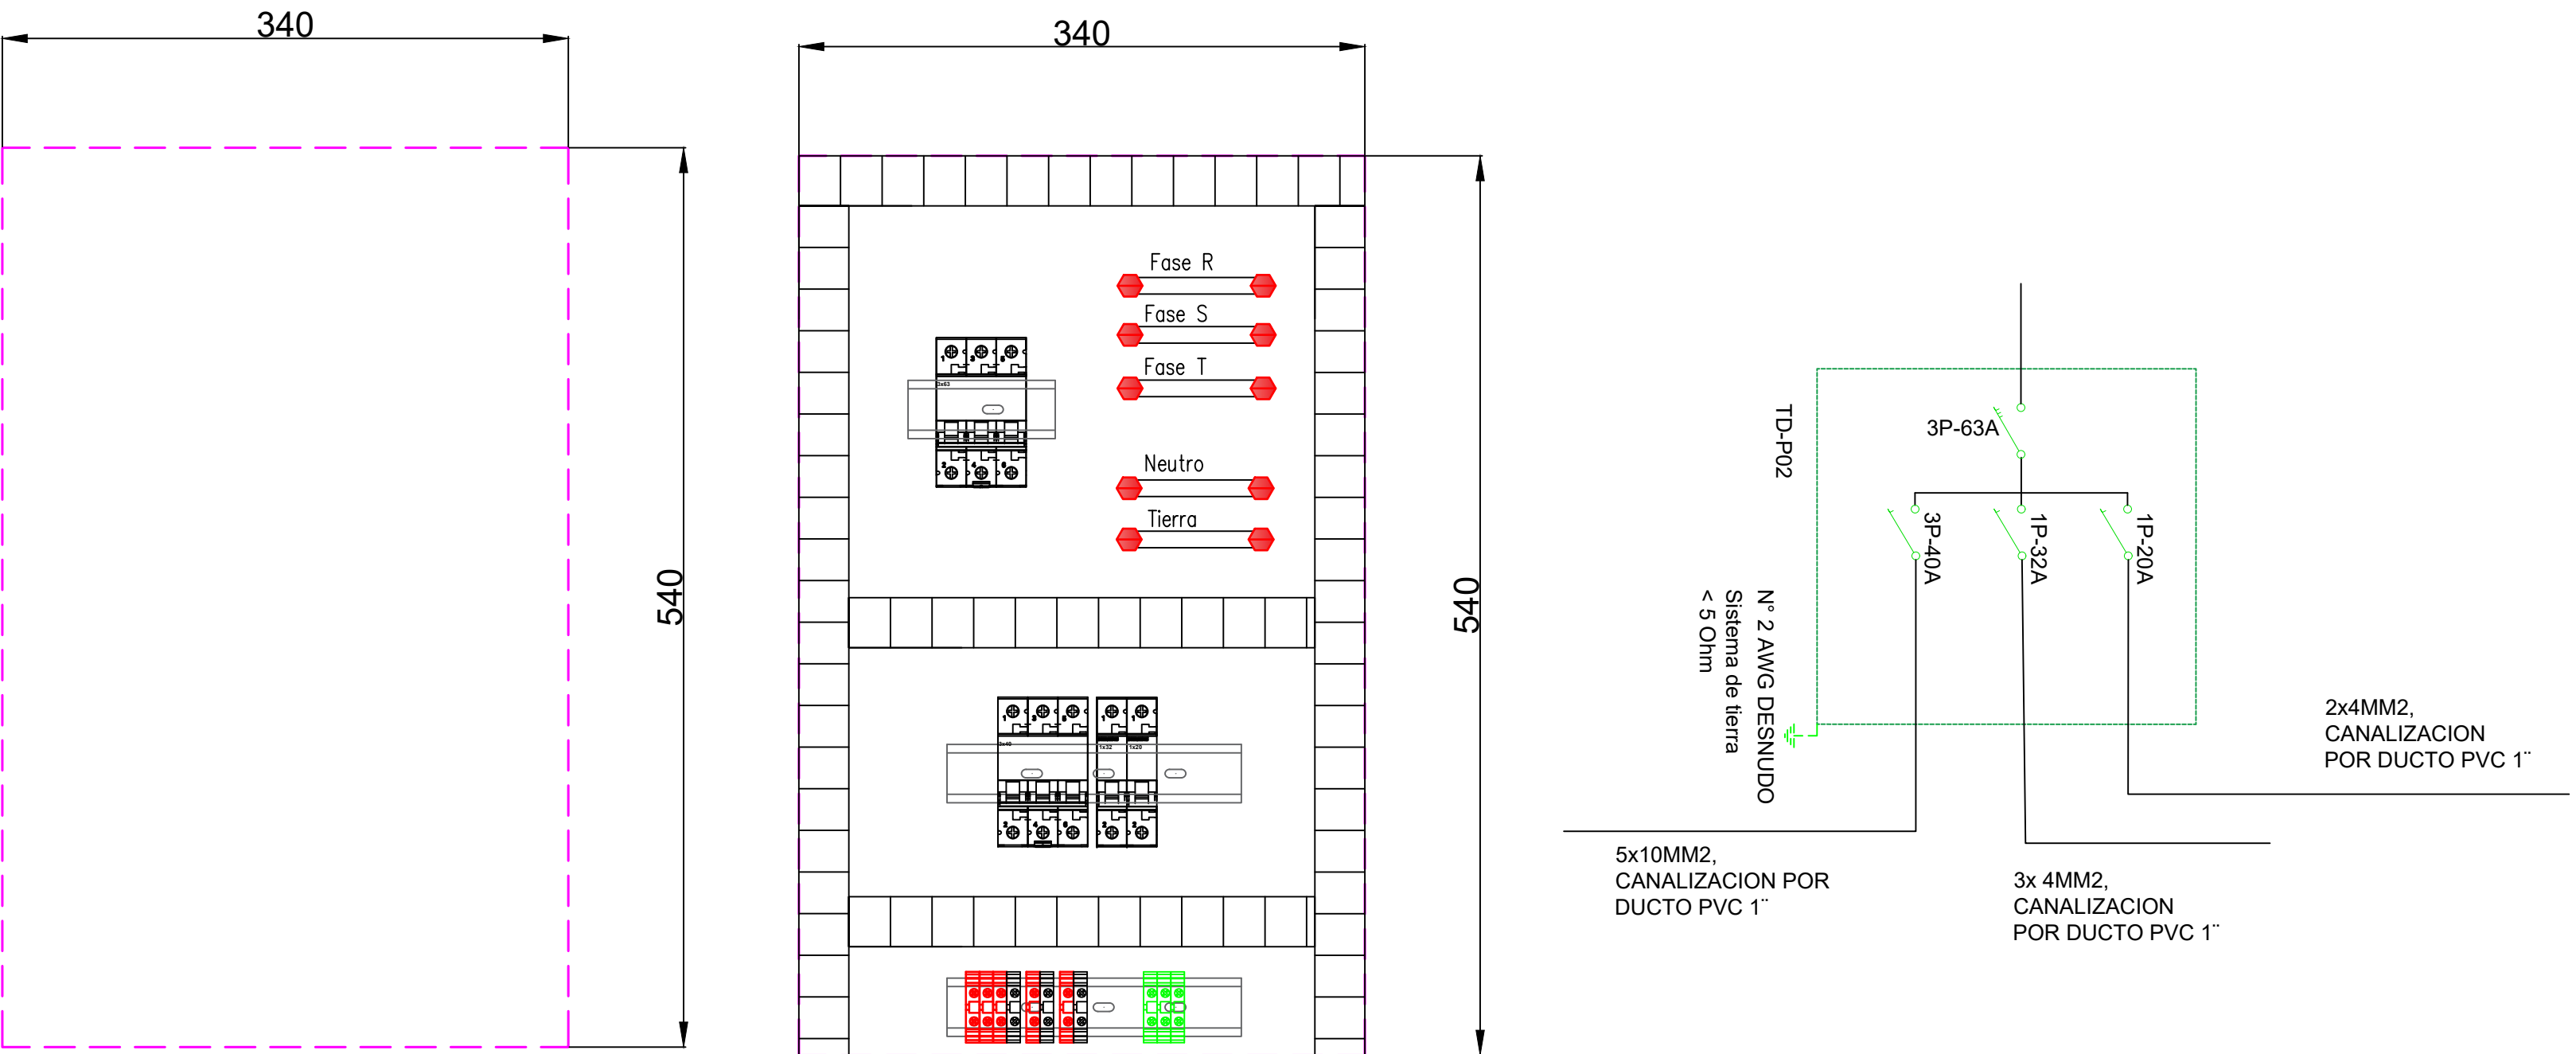


TABLERO PRINCIPAL 03

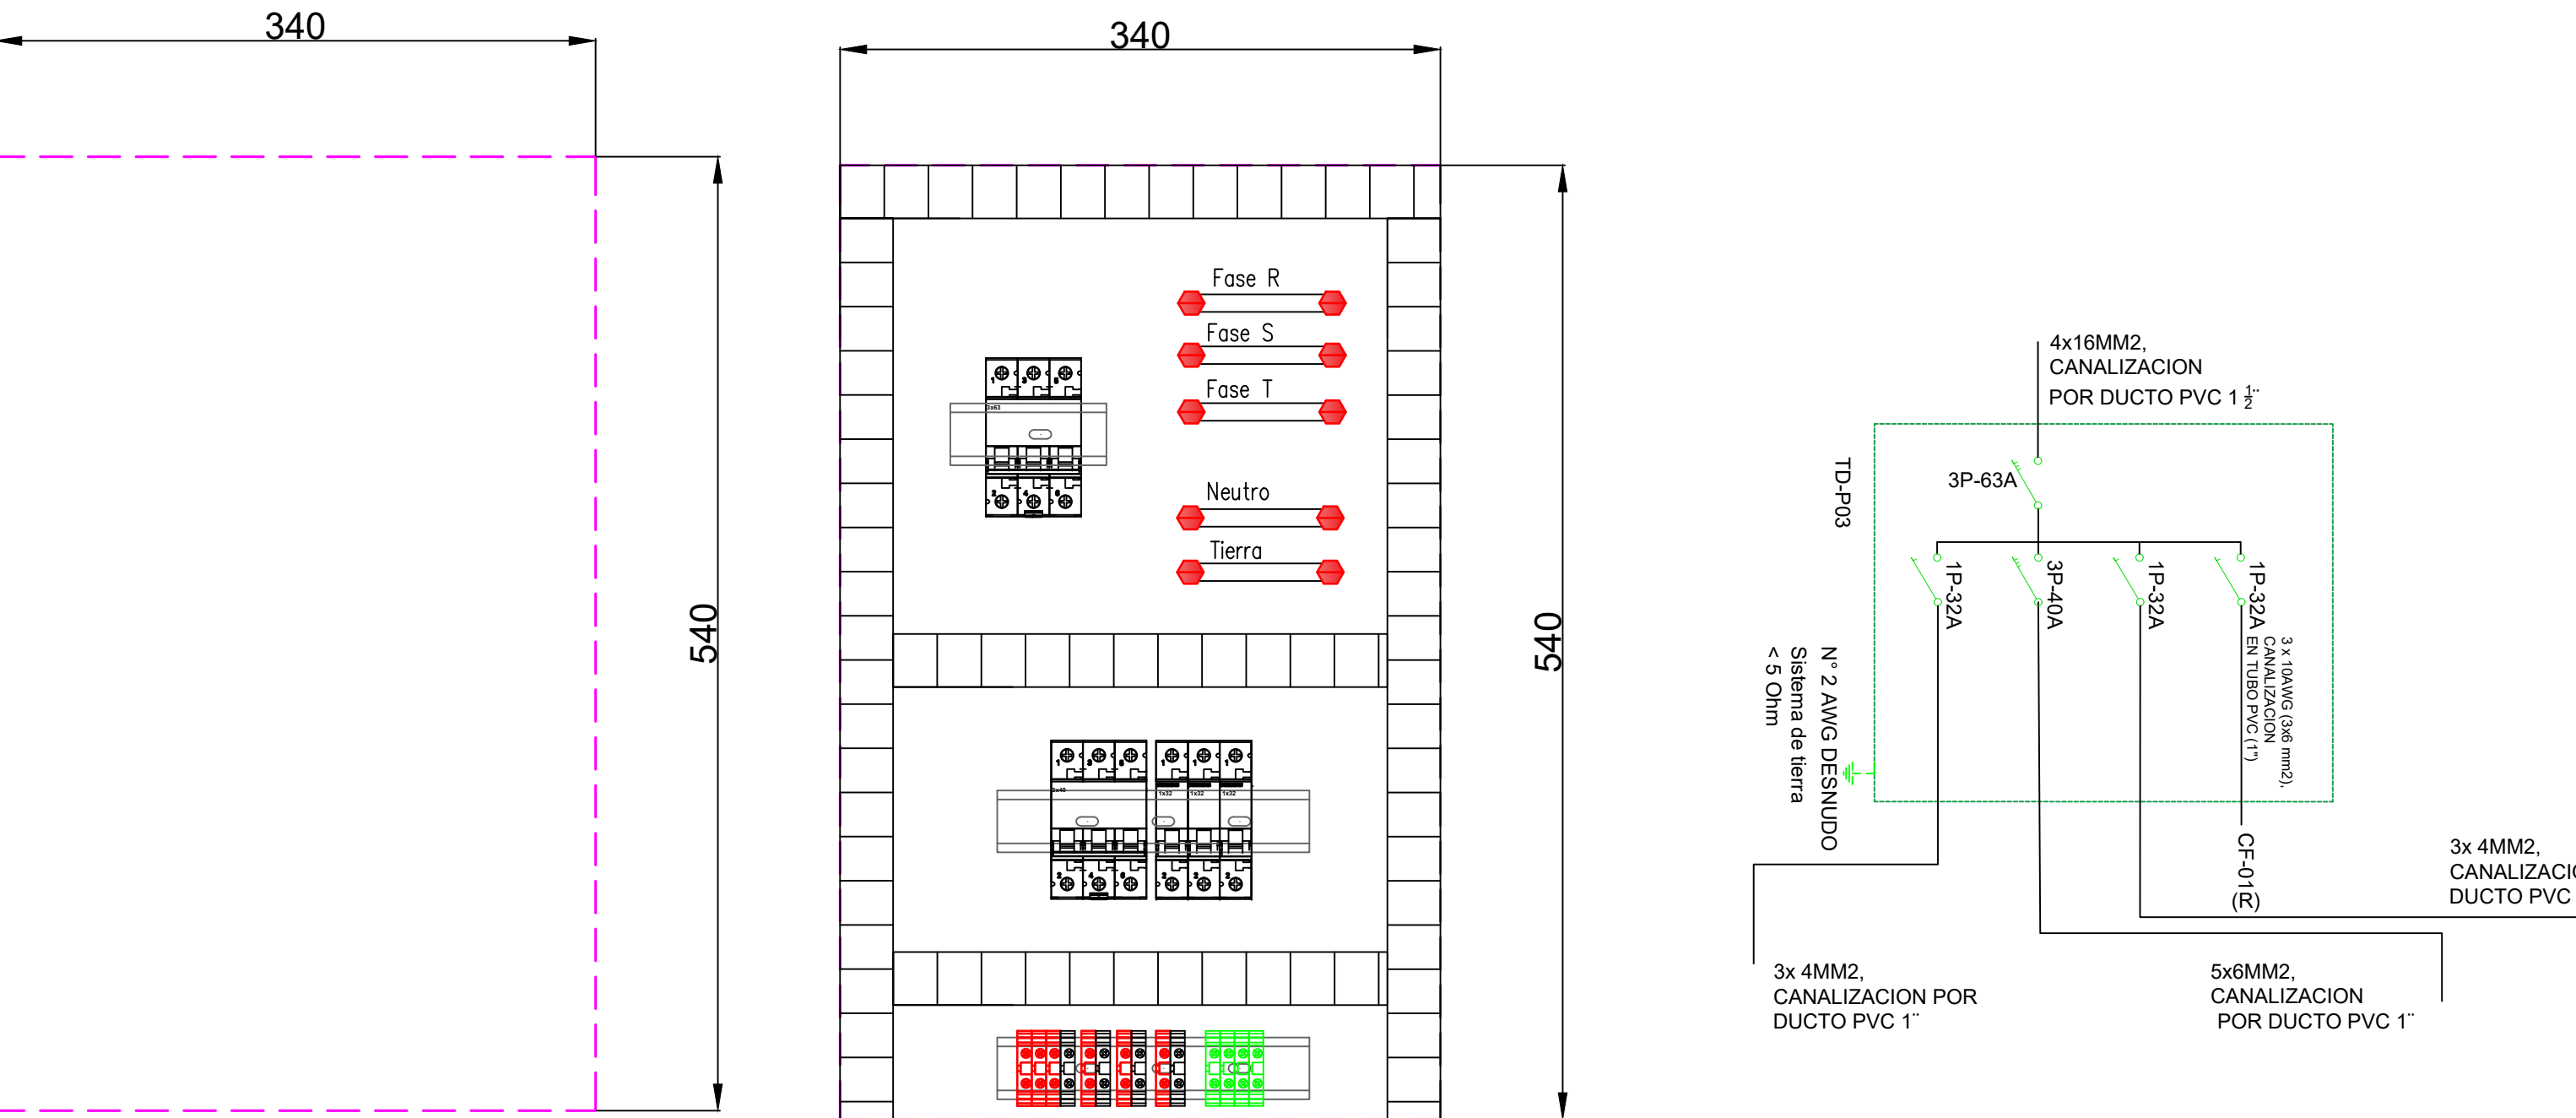



TABLERO PRINCIPAL 04

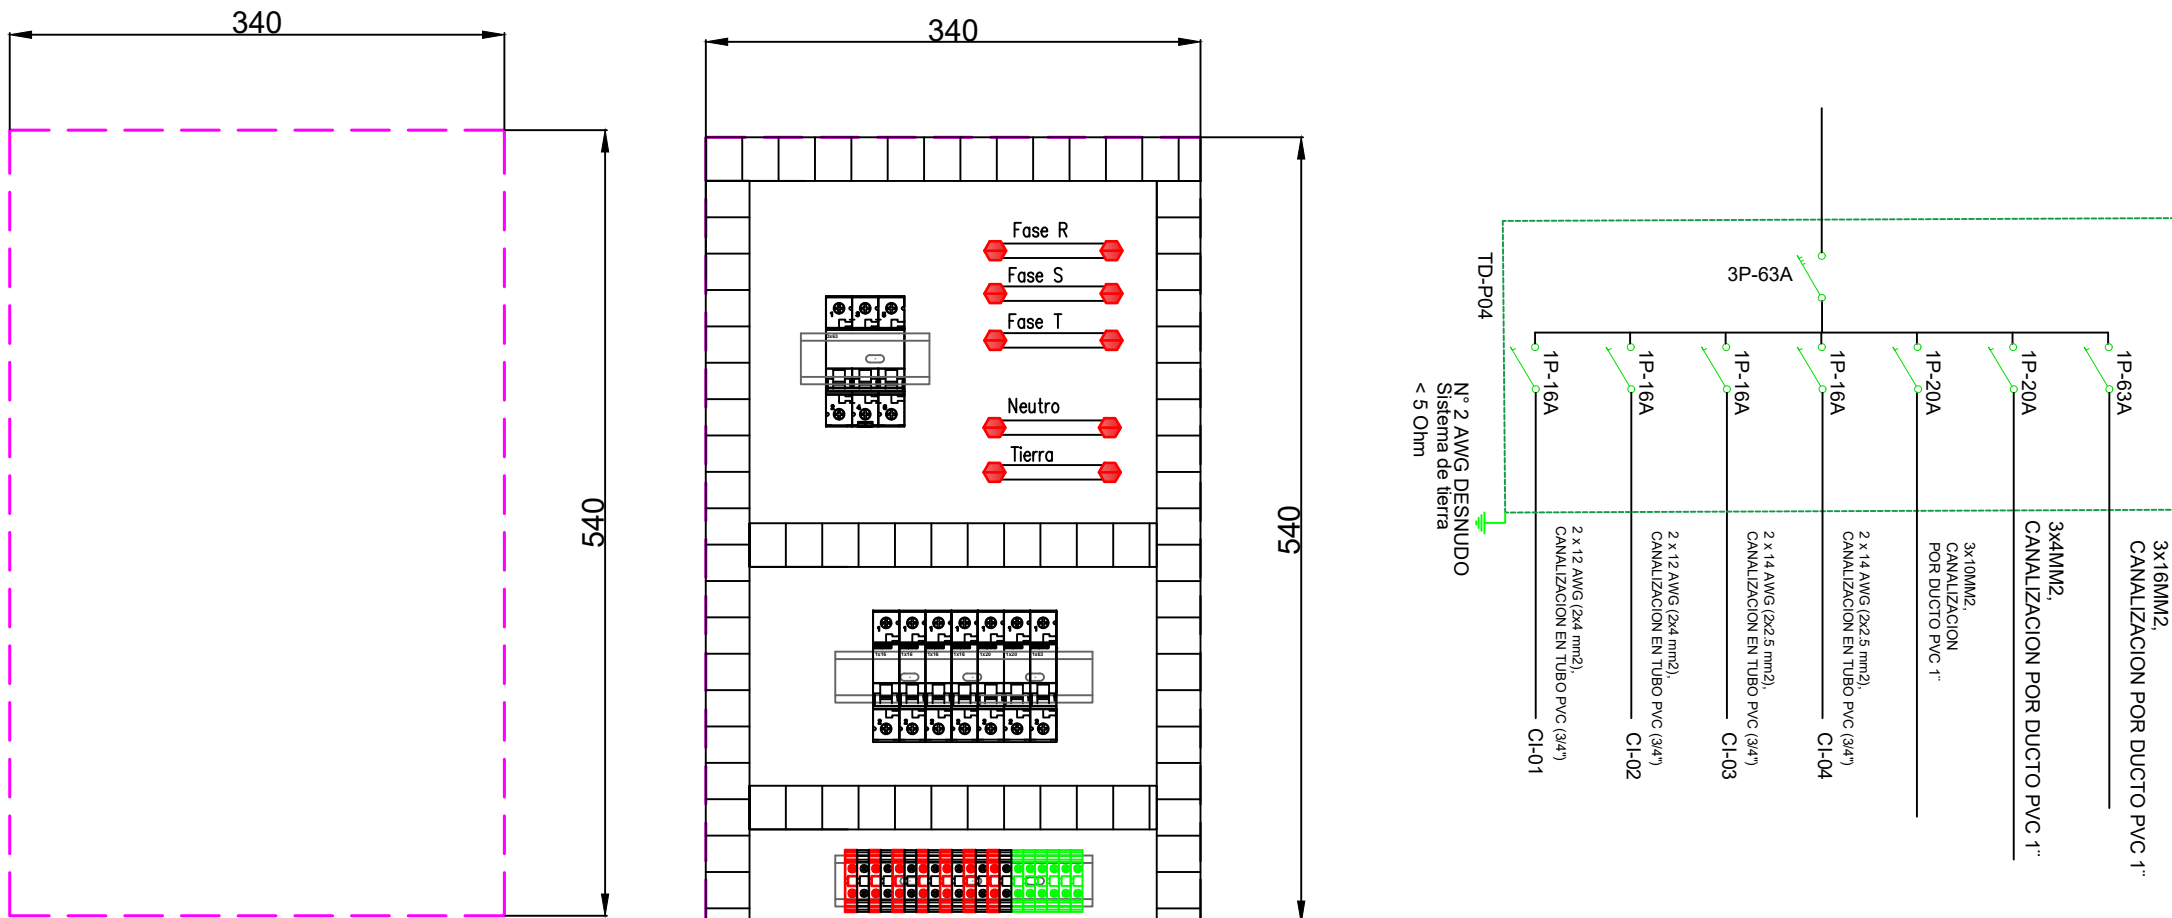

TABLERO PRINCIPAL 05

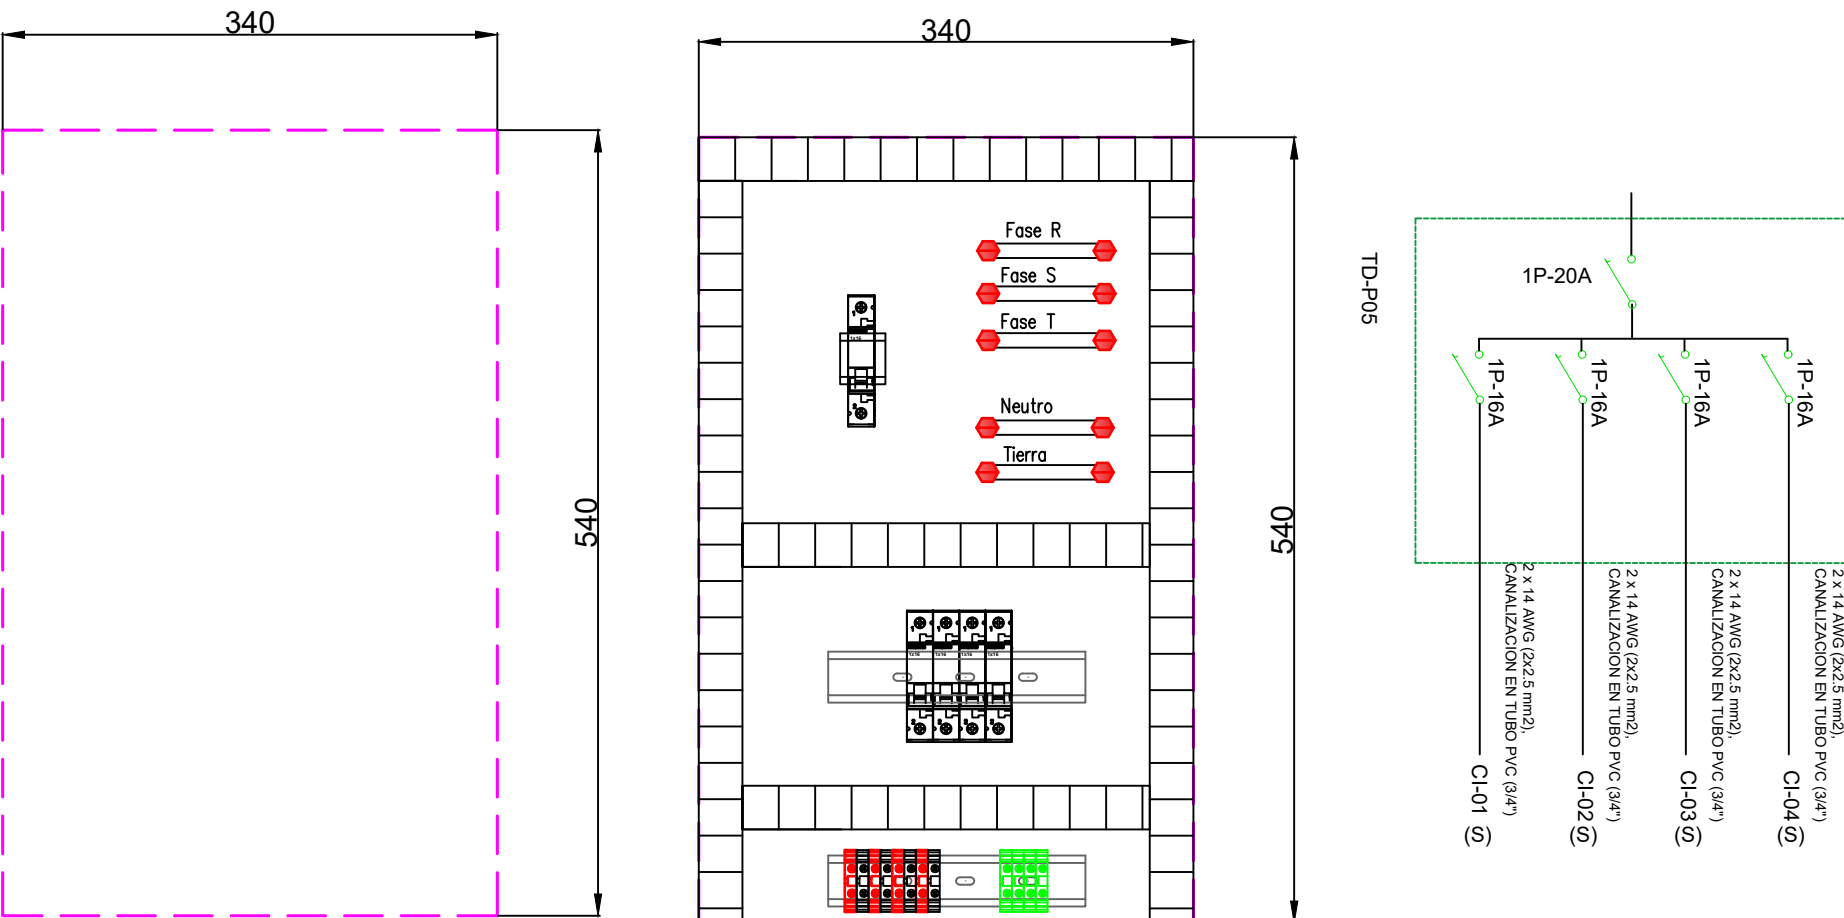

TABLERO PRINCIPALANF

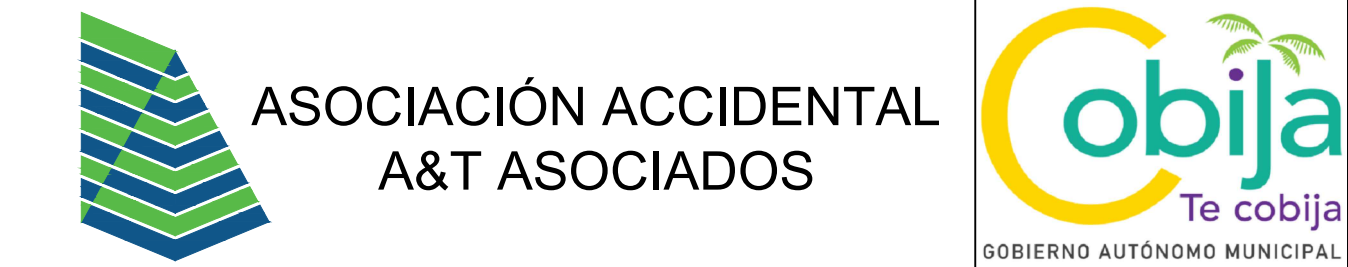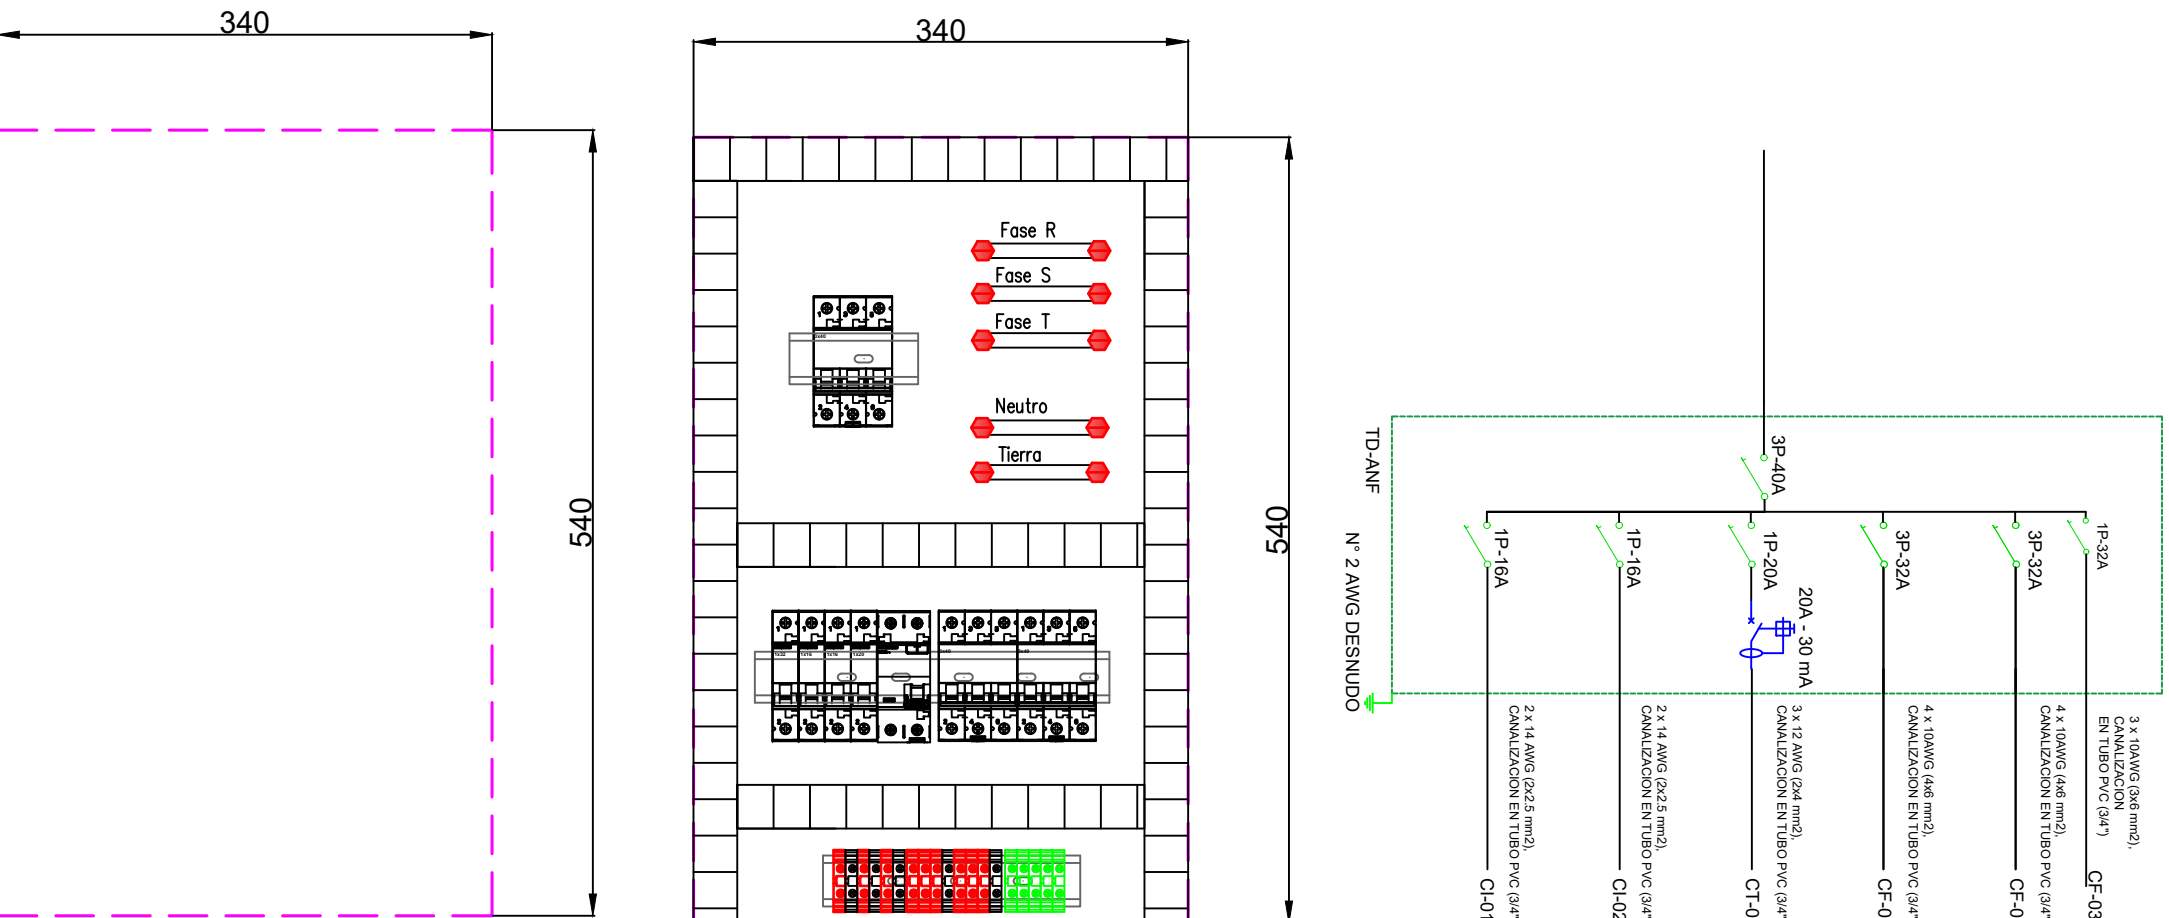

TABLEROS DE DISTRIBUCION			
PROPIETARIO (S): GOBIERNO AUTÓNOMO MUNICIPAL DE COBILJA		PROYECTO: SERVICIO DE CONSULTORÍA POR PRODUCTO PARA EL ESTUDIO DE DISEÑO TÉCNICO DE PREVENCIÓN "CONSTRUCCIÓN PLAZA DEL BICENTENARIO DE BOLIVIA EN EL MUNICIPIO DE COBILJA"	
UBICACION ESC: 1:1000		ZONA : MANANTIAL AV/ CALLE : ENTRE AV/TAHUAMANU ESQ. AV. LAS PALMAS ESQ. AV. 9 DE FEBRERO. DISTRITO : 02 PREDIO : 001 MANZANA : 051 CÓDIGO CAT. : 02 051 001 FECHA : Cobija, Diciembre 2024	
		SUPERFICIE DE LOTE : 35989.57 m2 SUPERFICIE A CONSTRUIR : 852.78 m2 SUPERFICIE CUBIERTA ABIERTA (MIRADOR) : 1472.46 m2	
ÁREAS A CONSTRUIR		N I V E L E S	
		RELEV.	CONST. PARCIAL
		Nivel 1 (arbolito)	+/-0.00 845.12 845.17 m2
		Nivel 1 (Servicio P. pública)	+1.45 106.40 106.40 m2
		Nivel 1 (Kiosco)	+1.75 95.14 95.14 m2
		Nivel 1 (Puesto de seguridad 1)	-2.76 3.06 3.06 m2
		Nivel 1 (Puesto de seguridad 1) 2.00	3.06 3.06 m2
		Nivel 1 (Interculturalidad)	+/- 0.00 571.43 571.42 m2
		Nivel 2 (Interculturalidad)	+ 3.25 254.65 254.65 m2
		TOTAL	826.07 m2 852.78 m2 1678.85 m2
		SUPERFICIE TOTAL CONSTRUIDA	852.78 m2

SELLO DE APROBACION G.A.M.C.		FIRMA DEL PROPIETARIO
RESPONSABLE PLAN REGULADOR GAMC	JEFE PLAN REGULADOR GAMC	DIRECTOR PLAN REGULADOR GAMC
SELLO DE ENTE COLEGIADO		ING. JOSÉ ANTONIO VELARDE NAVARRO SELLO