


PLANTA ALTA

"UNIDAD EDUCATIVA WAÑOMA BAJA-POROMA"

DUCTOS DE TOMACORRIENTES PLANTA ALTA VISTA ISOMETRICA DUCTEADO O-S

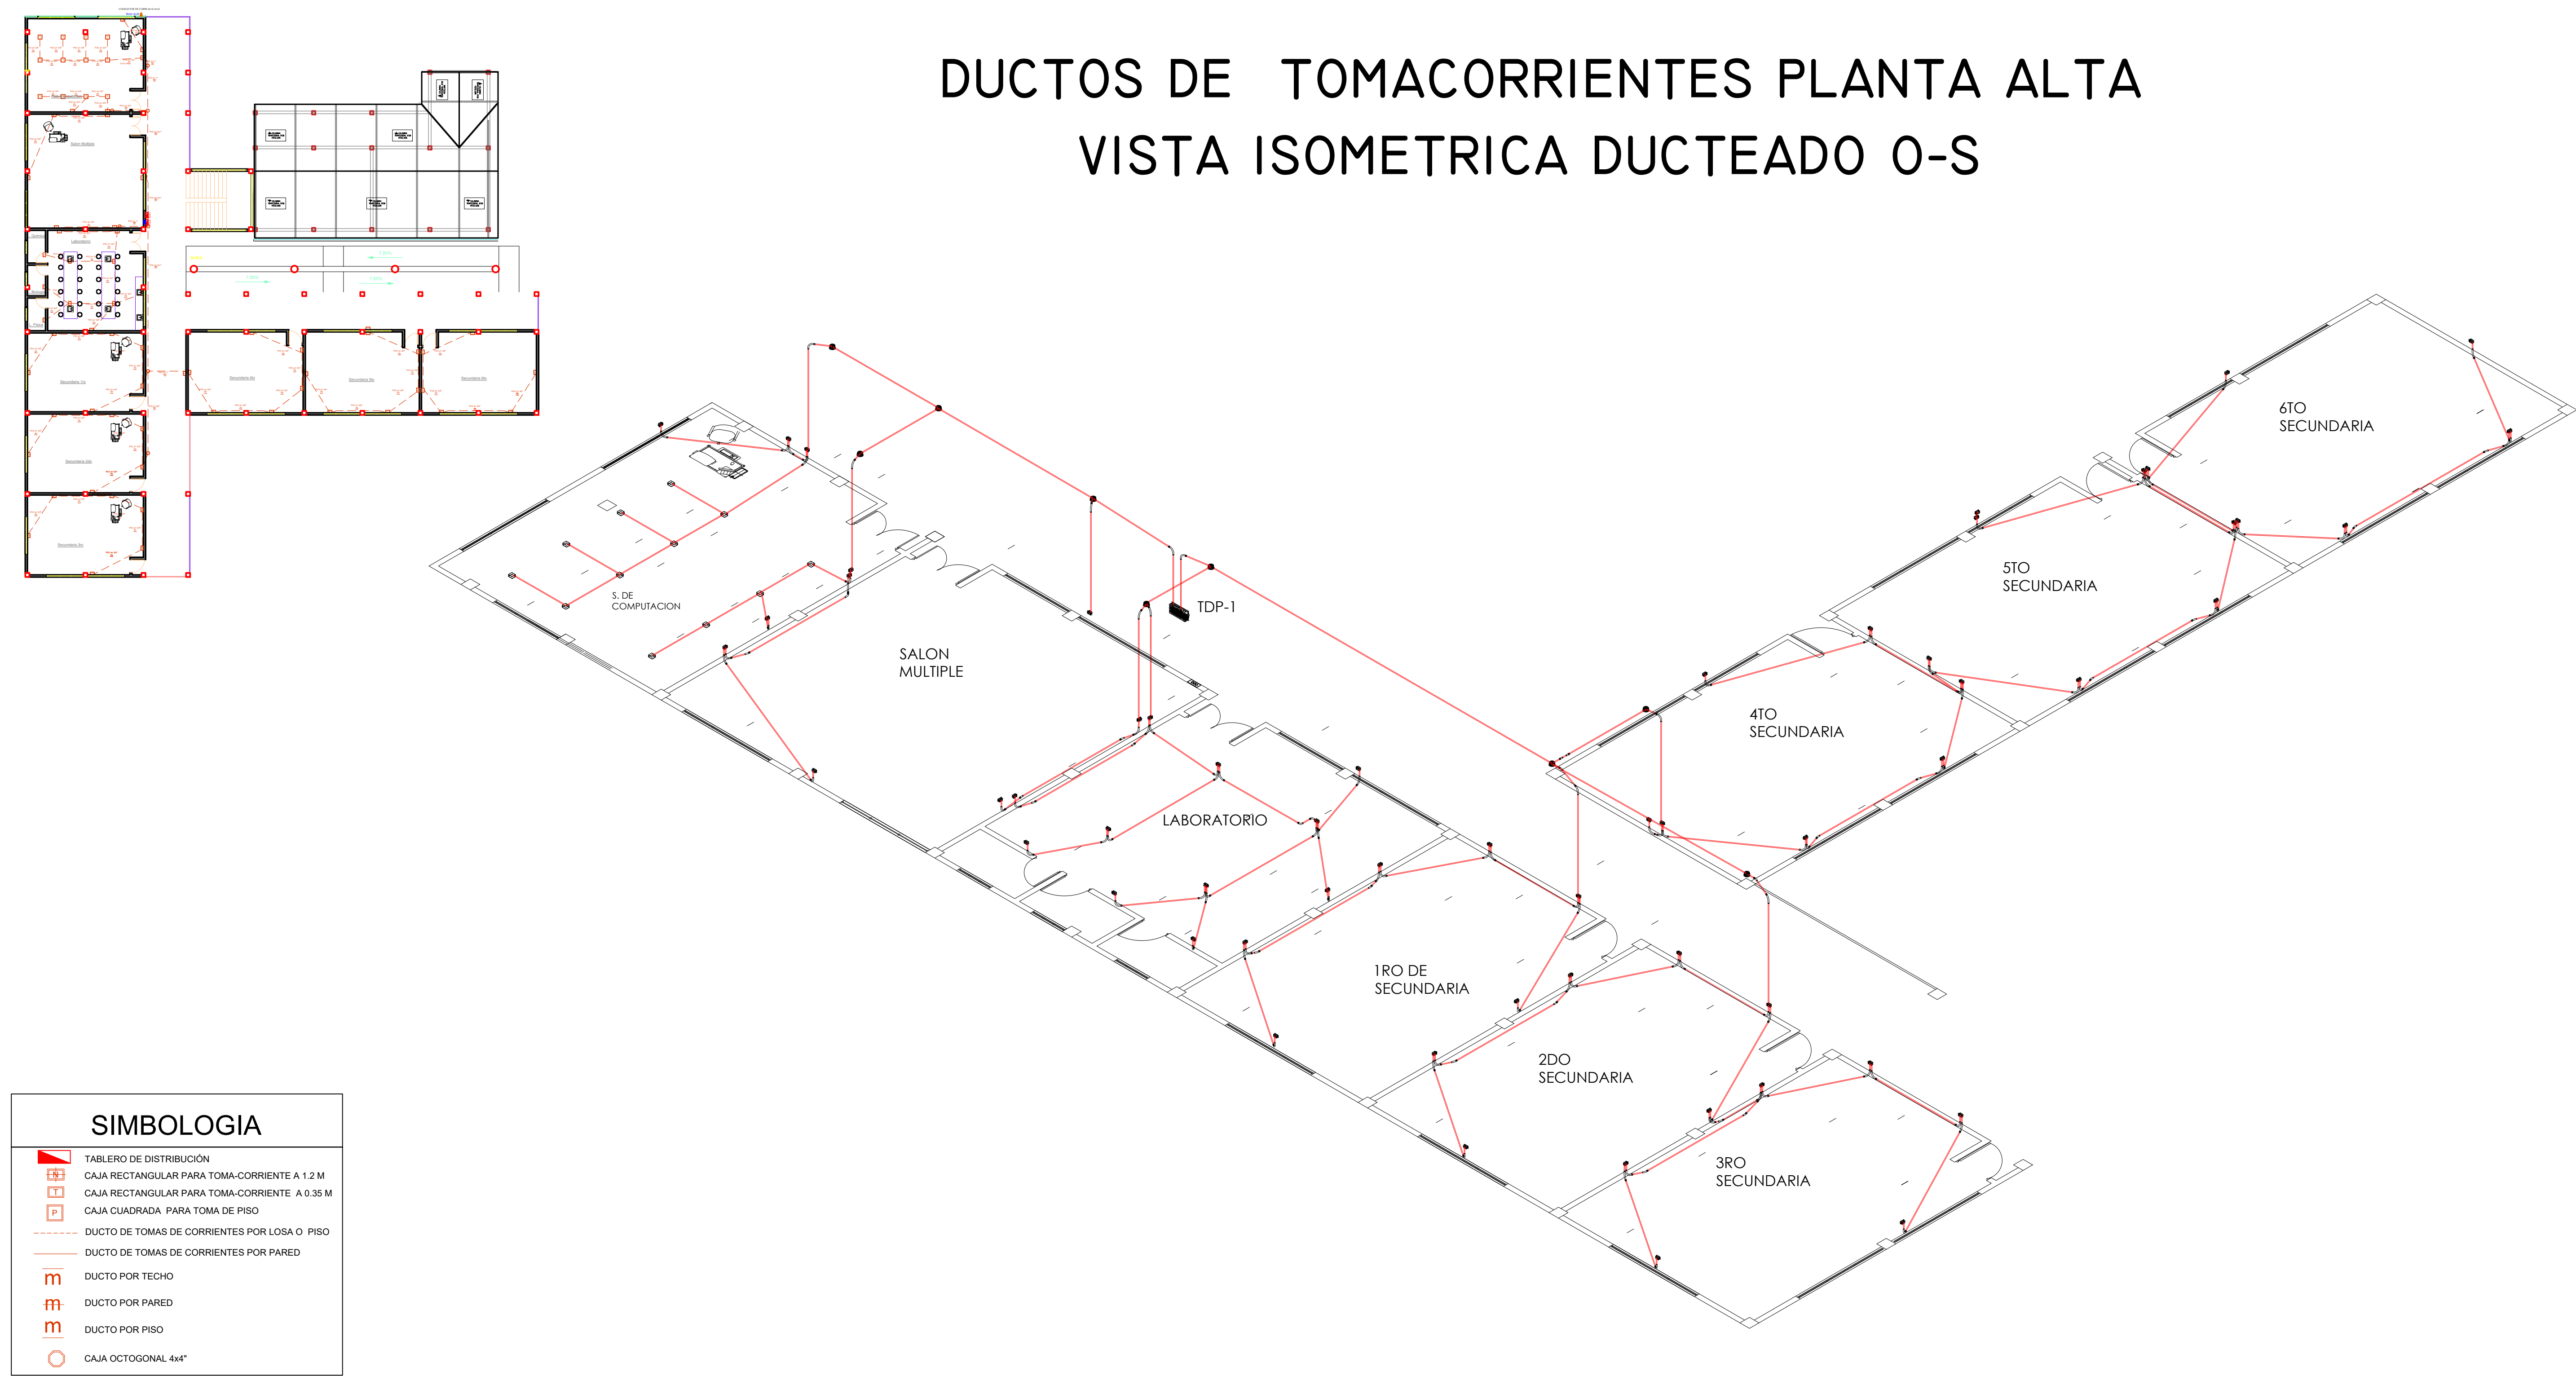

SIMBOLOGIA

- TABLERO DE DISTRIBUCION
- CAJA RECTANGULAR PARA TOMA-CORRIENTE A 1.2 M
- CAJA RECTANGULAR PARA TOMA-CORRIENTE A 0.35 M
- CAJA CUADRADA PARA TOMA DE PISO
- DUCTO DE TOMAS DE CORRIENTES POR LOSA O PISO
- DUCTO DE TOMAS DE CORRIENTES POR PARED
- DUCTO POR TECHO
- DUCTO POR PARED
- DUCTO POR PISO
- CAJA OCTOGONAL 4x4"



EMPRESA ASOCIACIÓN ACCIDENTAL
JUKUMARI Y ASOCIADOS

GERENTE DE SUPERVISIÓN
HIDELEX CONSTRUCCIONES

FISCAL DE OBRA
G.A.M.POROMA



NOMBRE DEL PROYECTO:
CONST. UNIDAD EDUCATIVA WAÑOMA BAJA - POROMA

ESCALA: **INDICADA** Fecha: **MAYO 2025** Lámina: **EL-11.1**

CONTENIDO DE LA LÁMINA:
PLANOS AS BUILT-PLANOS ELECTRICOS