
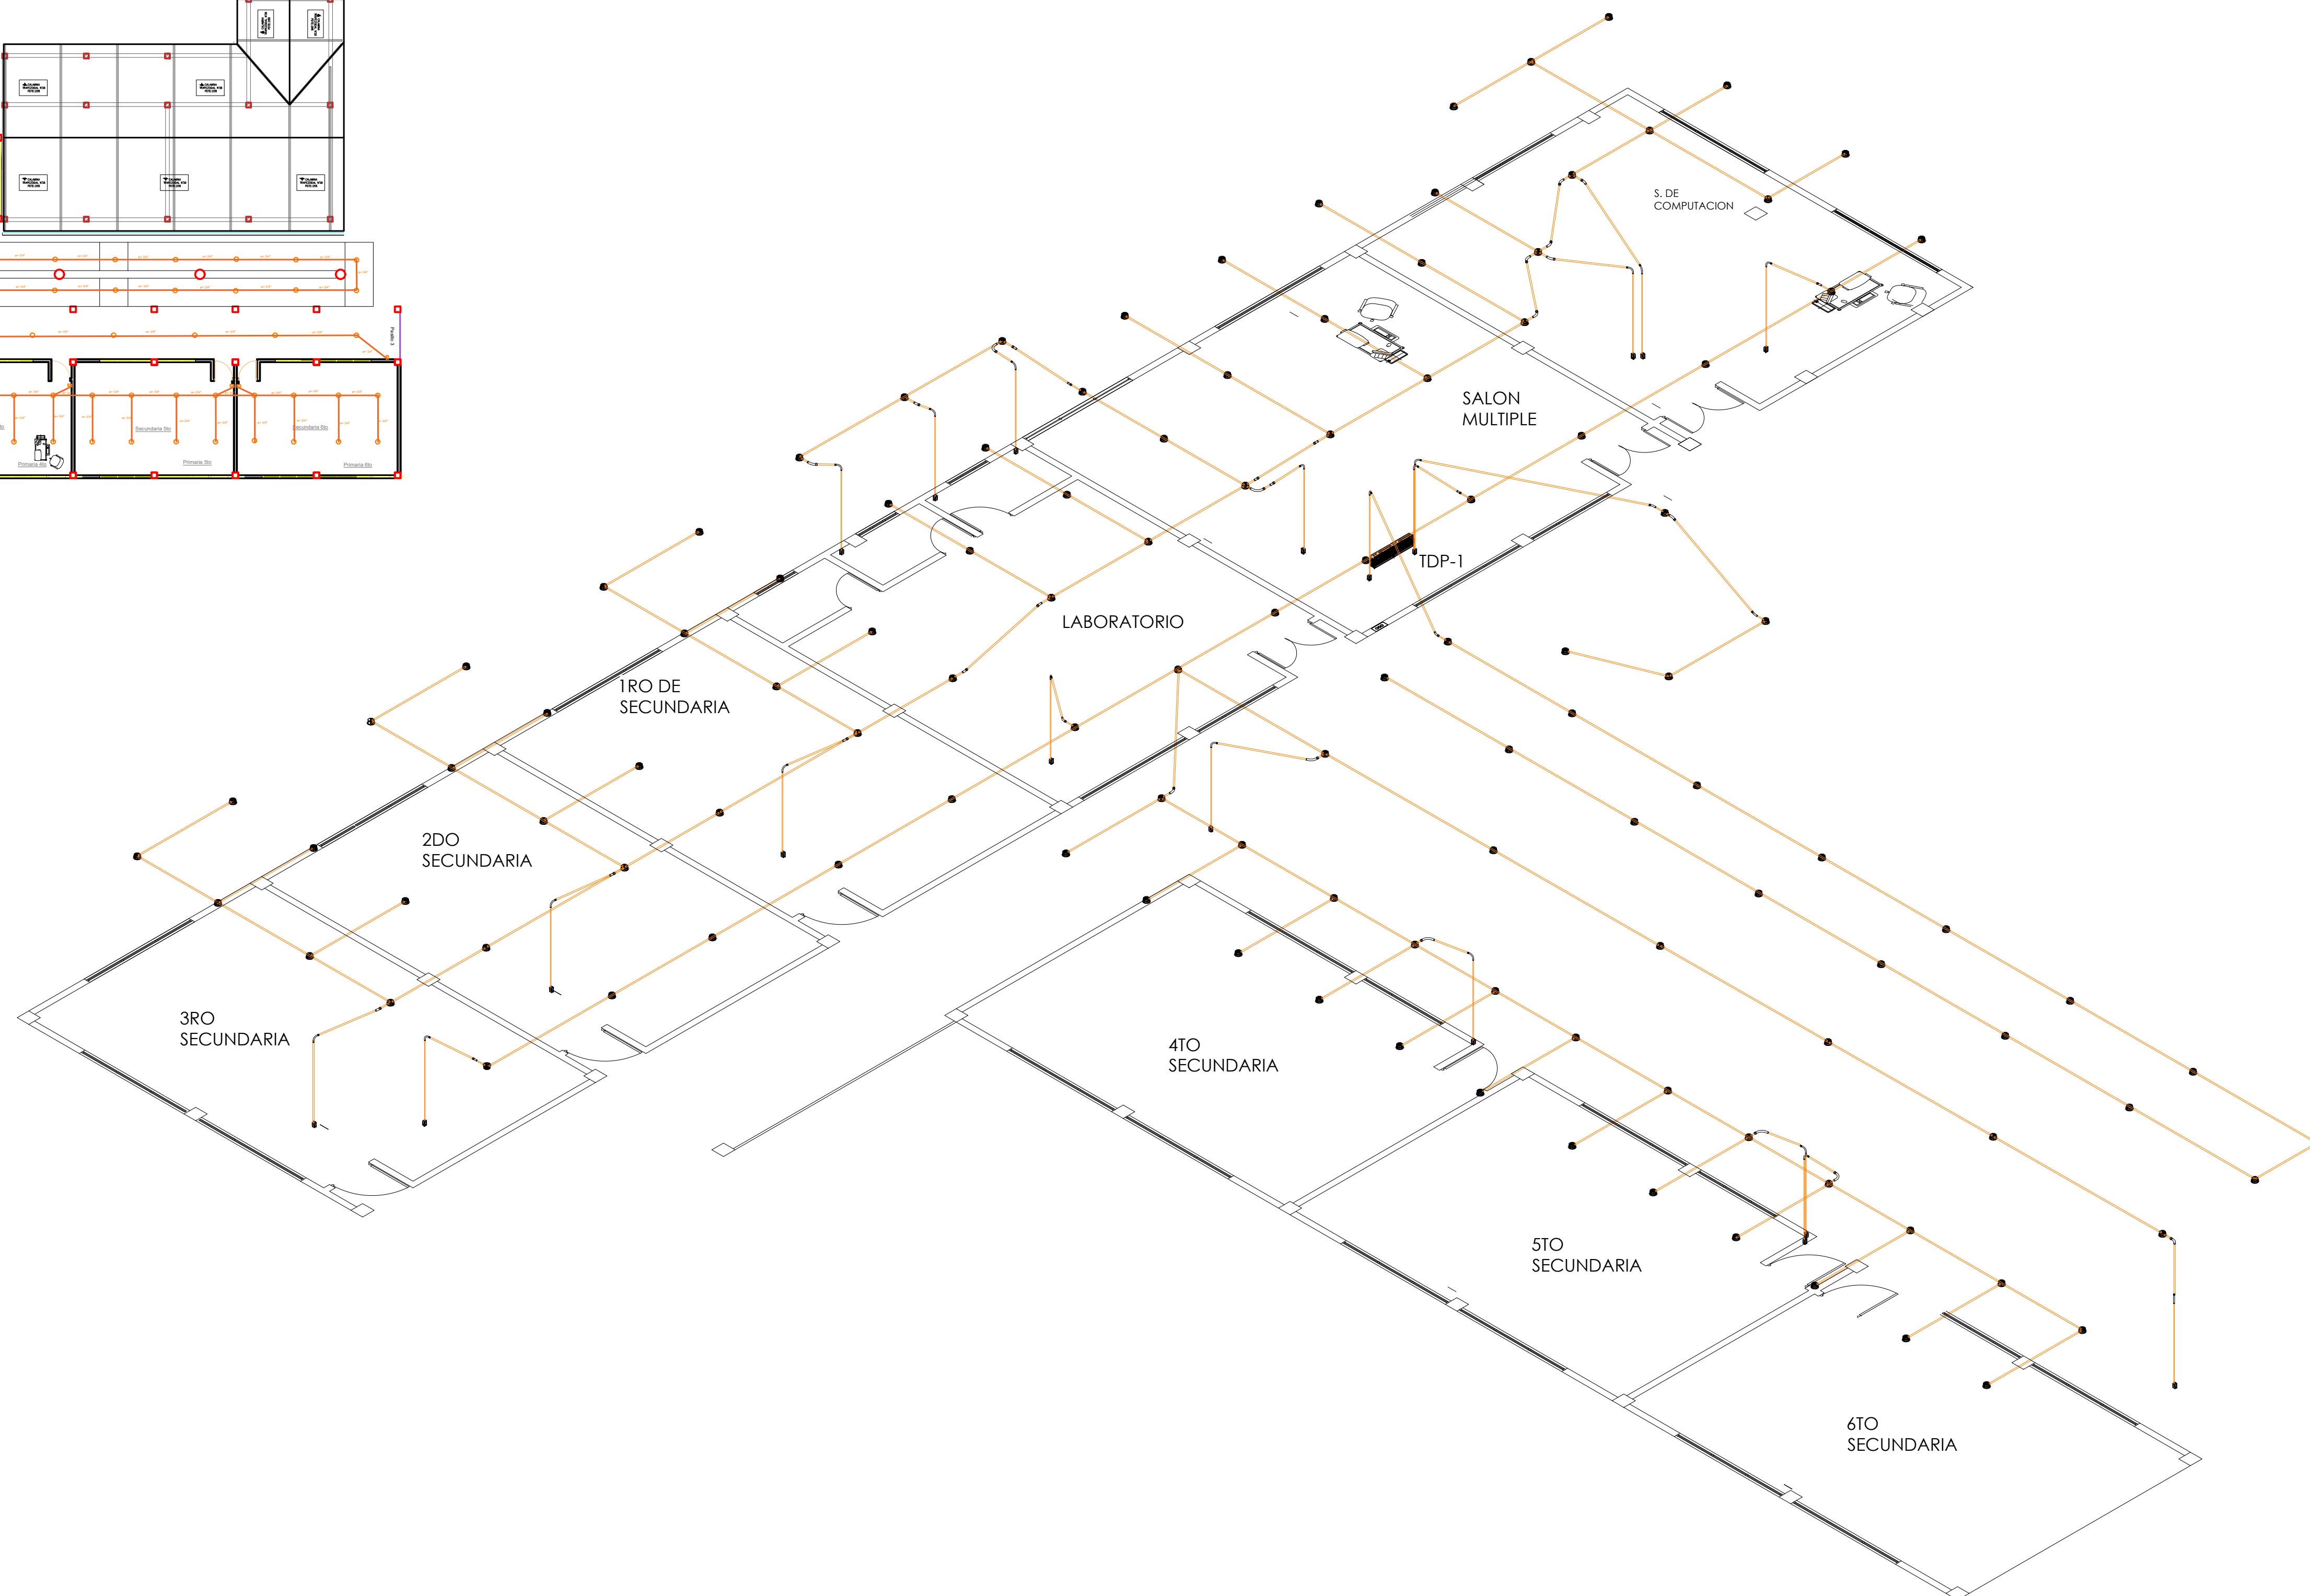


PLANTA ALTA

"UNIDAD EDUCATIVA WAÑOMA BAJA-POROMA"

DUCTOS DE ILUMINACIÓN MODIFICADO PLANTA ALTA

VISTA ISOMETRICA DUCTEADO S-E

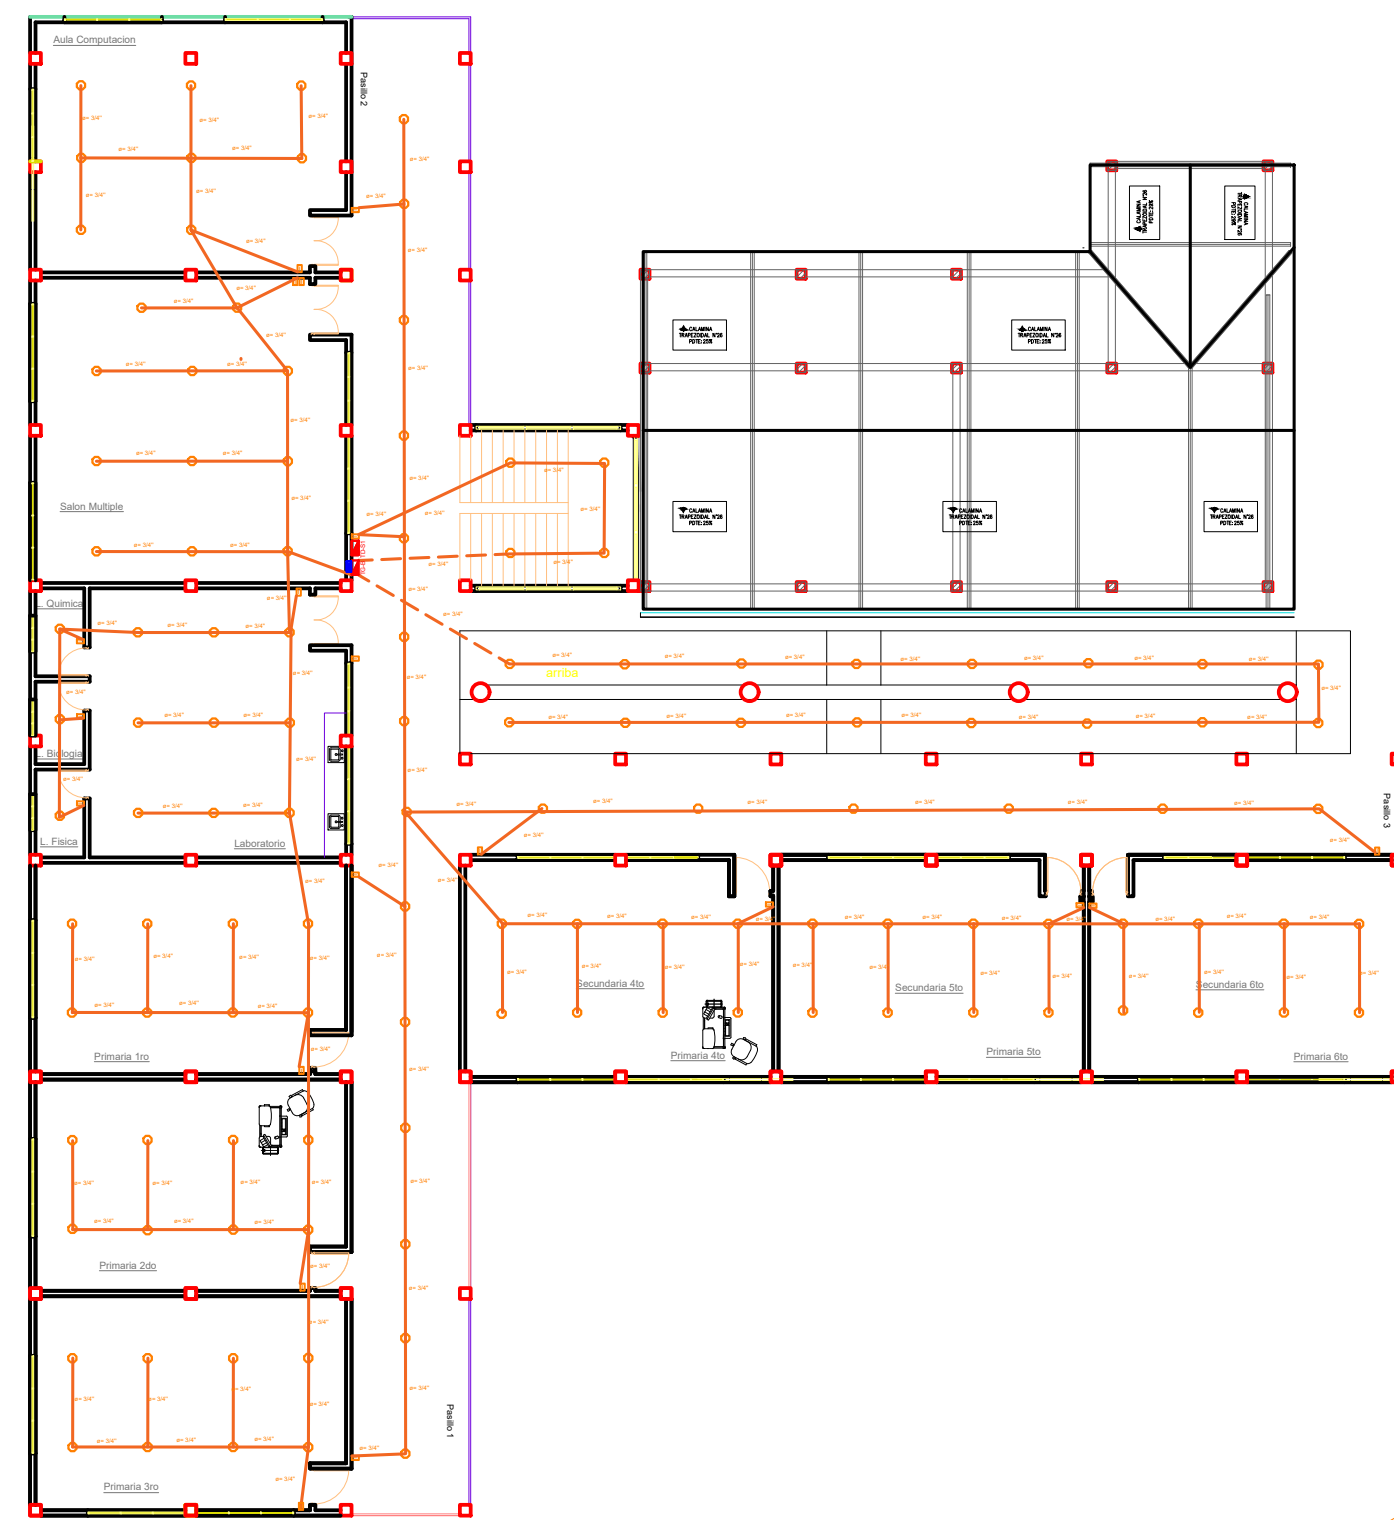

**EMPRESA ASOCIACIÓN ACCIDENTAL
JUKUMARI Y ASOCIADOS**

**GERENTE DE SUPERVISIÓN
HIDELEX CONSTRUCCIONES**

**FISCAL DE OBRA
G.A.M.POROMA**



NOMBRE DEL PROYECTO:
**CONST. UNIDAD EDUCATIVA WAÑOMA BAJA -
POROMA**

ESCALA: **INDICADA** Fecha: **MAYO 2025** Lámina: **EL-9**

CONTENIDO DE LA LÁMINA:
PLANOS AS BUILT-PLANOS ELECTRICOS