


DIAGRAMA UNIFILAR

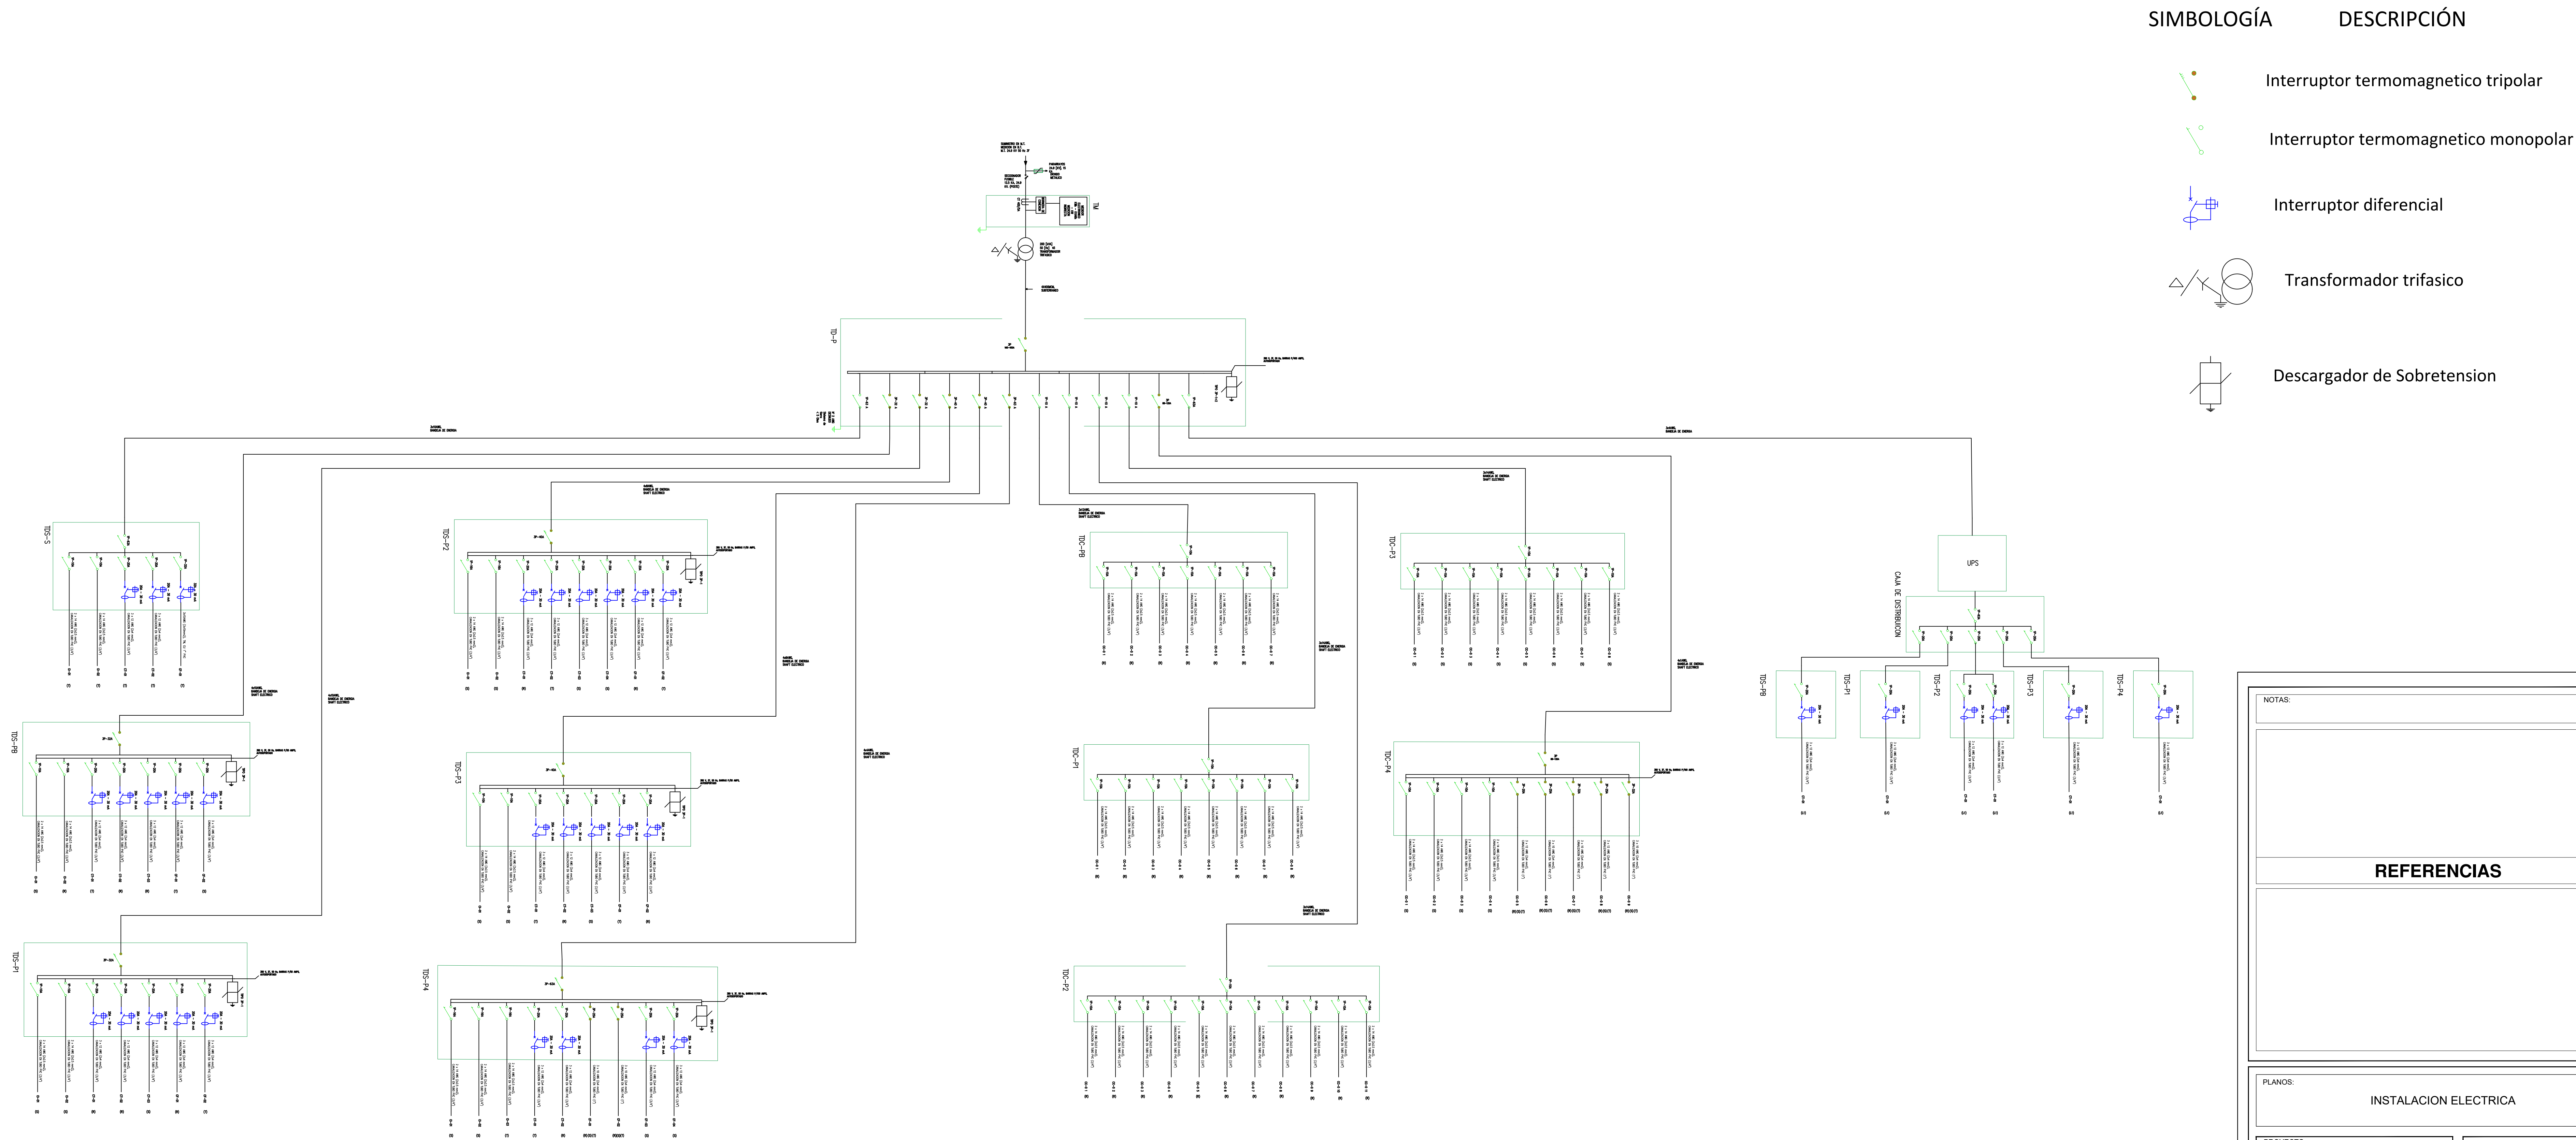

SIMBOLOGÍA	DESCRIPCIÓN
	Interruptor termomagnetico tripolar
	Interruptor termomagnetico monopolar
	Interruptor diferencial
	Transformador trifasico
	Descargador de Sobretension

NOTAS:

REFERENCIAS

PLANS:

INSTALACION ELECTRICA

PROYECTO:

DISEÑO ELECTRICO FISCALIA

PROPIETARIO:

FISCALIA

PROYECTISTA:

ING. JORGE FERNANDO POVEDA RUIZ

DIRECCION :

EDUARDO BERDECIO

CODIGO CATASTRAL

00700020016

SUP. TOTAL CONST:

2895.77 M2

FECHA: 05/09/2023

ESCALA: INDICADAS

LÁMINA: 16 DE 16


SELLOS DE APROBACIÓN G.A.M.S.:

SELLOS ENTE COLEGADO:

PLANO DE UBICACION :

Esc. 1: 5000

DISTRIBUCIÓN DE LUMINARIAS

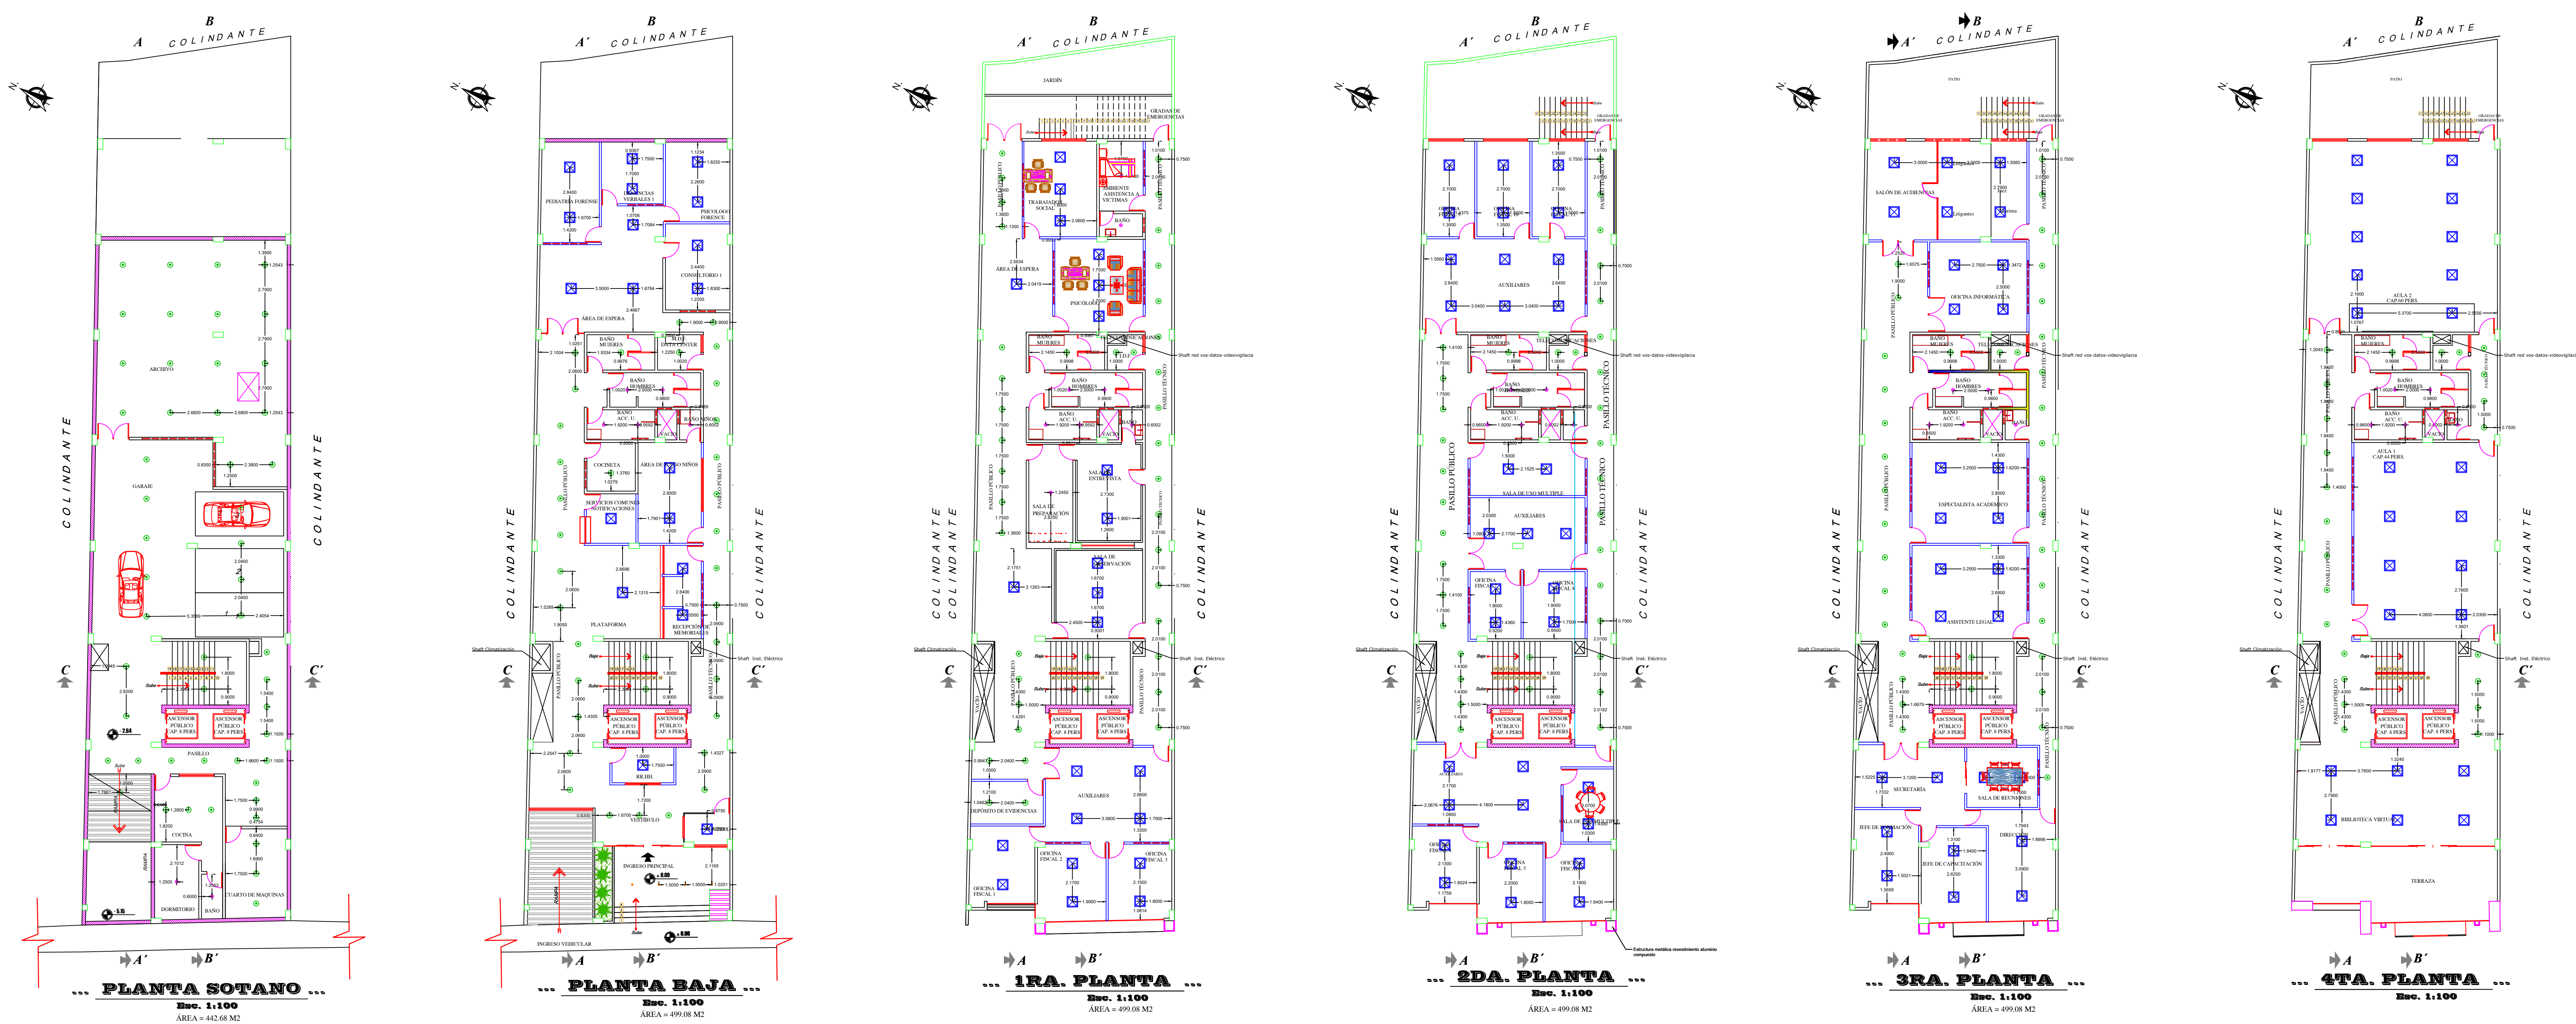

SIMBOLOGÍA	DESCRIPCIÓN
	Interruptor de Simple, h=1.25m.
	Interruptor conmutador, h=1.25m.
	Interruptor doble, h=1.25m.
	Caja Octogonal.
	Caja Rectangular.
	Ducteado de Iluminación, PVC - 3/4".
	Circuito de iluminación 1
	Circuito de iluminación 2
	Luminaria led 60 w
	Luminaria led 24 w
	Luminaria led 12 w
	Luminaria Spot led 8 w

NOTAS:

REFERENCIAS

PLANOS:

INSTALACION ELECTRICA

PROYECTO:

DISENO ELECTRICO FISCALIA

PROPIETARIO:

FISCALIA

PROYECTISTA:

ING. JORGE FERNANDO POVEDA RUIZ

DIRECCION :

EDUARDO BERDECIO

CODIGO CATASTRAL

0070020016

SUP. TOTAL CONST:

2895.77 M2

FECHA: 05/09/2023

ESCALA: INDICADAS

LÁMINA: 1 DE 16


SELLOS DE APROBACIÓN G.A.M.S.:

PLANO DE UBICACION:

Esc. 1: 5000

SELLOS ENTE COLEGADO:

CIRCUITO DE ILUMINACIÓN

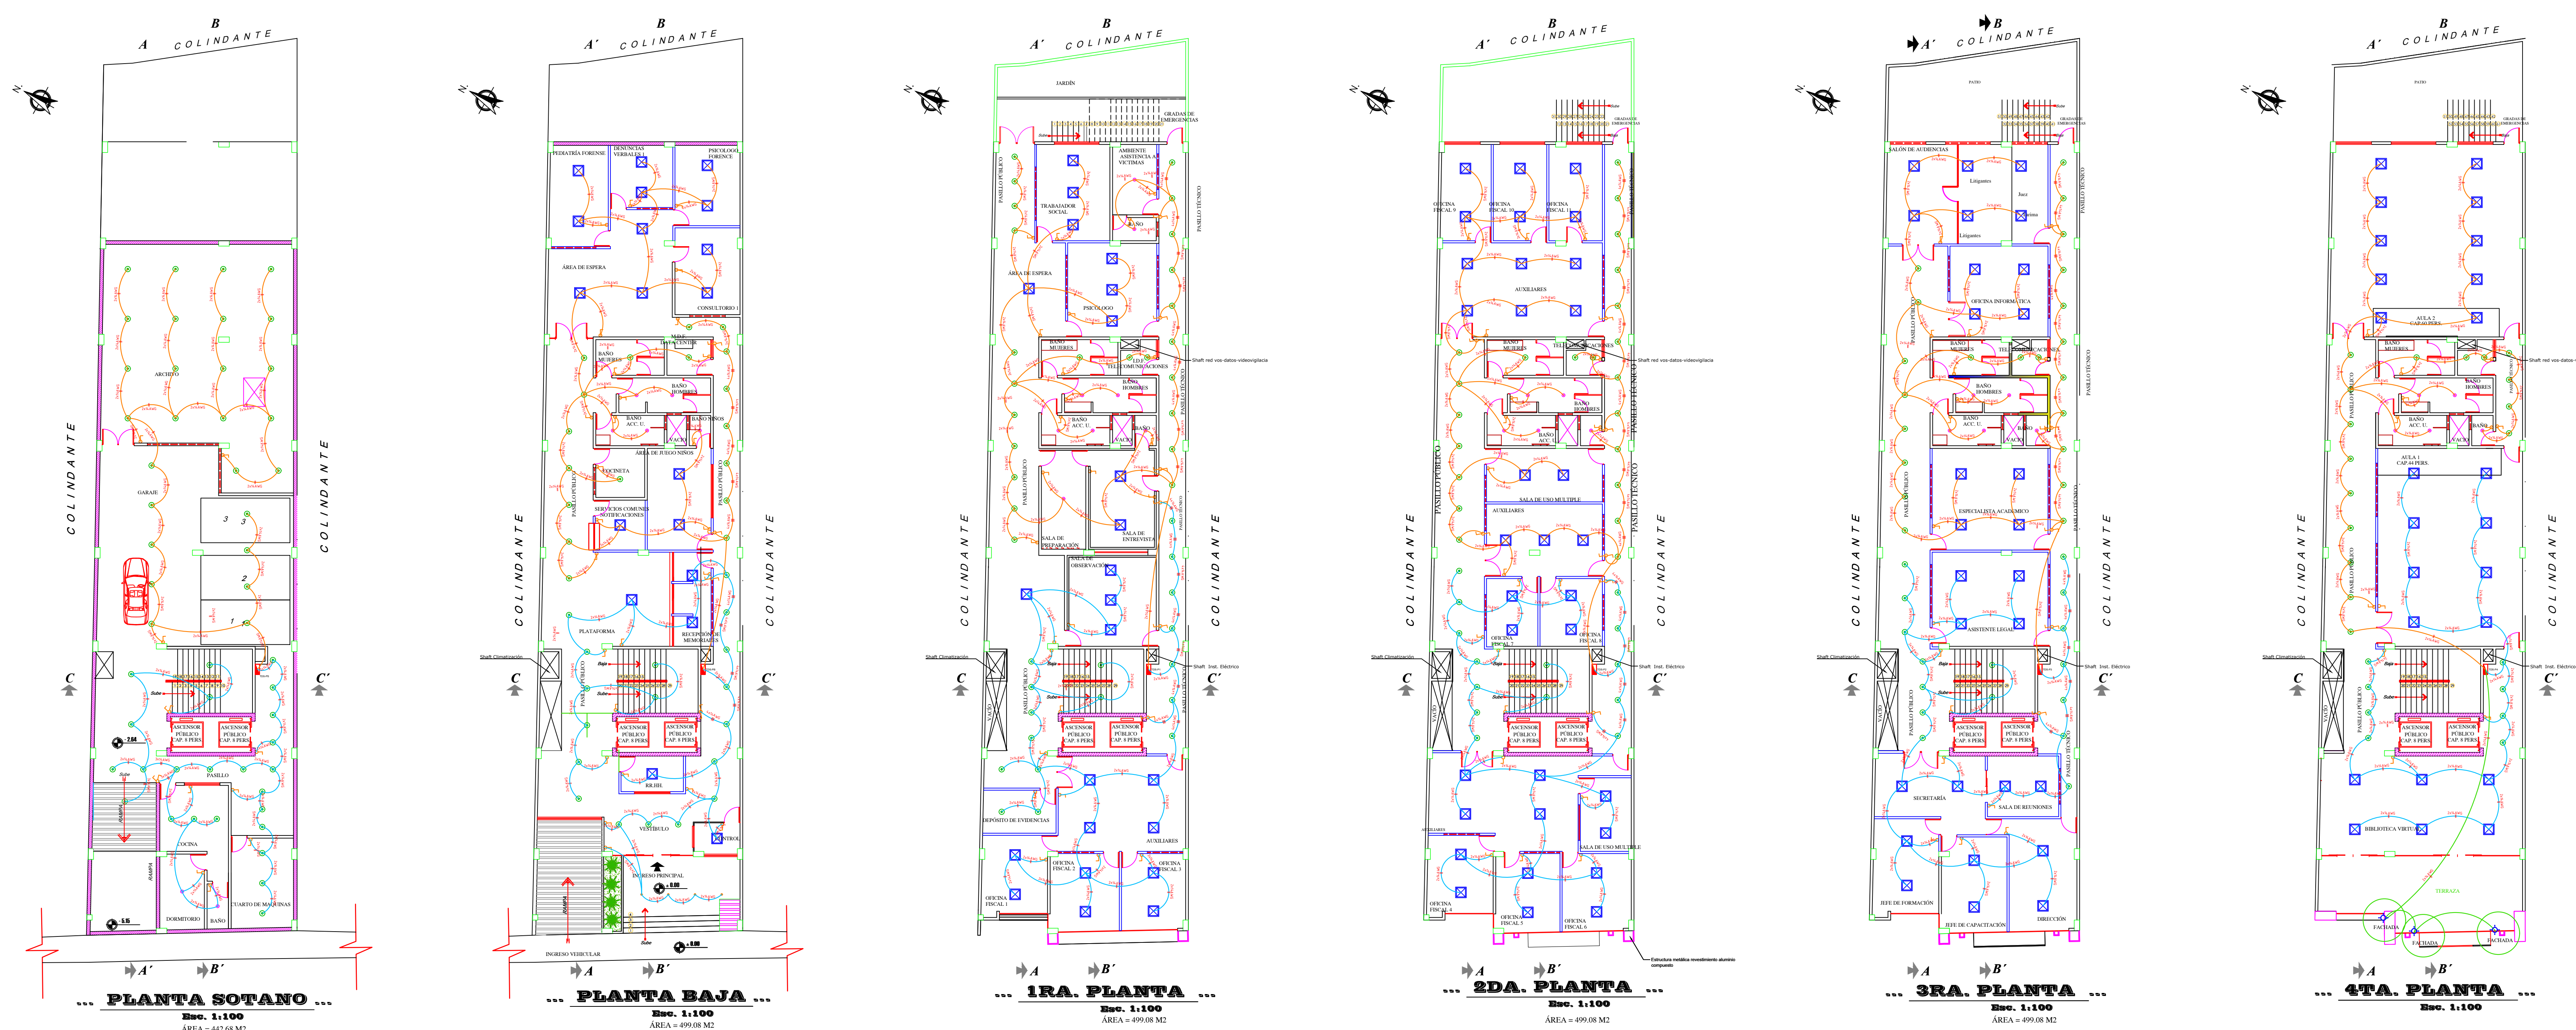

SIMBOLOGÍA	DESCRIPCIÓN
	Interruptor de Simple, h=1.25m.
	Interruptor conmutador, h=1.25m.
	Interruptor doble, h=1.25m.
	Caja Octogonal.
	Caja Rectangular.
	Ducteado de Iluminación, PVC - 3/4".
	Circuito de iluminación 1
	Circuito de iluminación 2
	Luminaria led 60 w
	Luminaria led 24 w
	Luminaria led 12 w
	Luminaria led 8 w

NOTAS:

REFERENCIAS

PLANOS:

INSTALACION ELECTRICA

PROYECTO:

DISEÑO ELECTRICO FISCALIA

PROPIETARIO:

FISCALIA

PROYECTISTA:

ING. JORGE FERNANDO POVEDA RUIZ

DIRECCION :

EDUARDO BERDECIO

CODIGO CATASTRAL

007 0002 0016

SUP. TOTAL CONST:

2895.77 M2

FECHA: 05/09/2023

ESCALA: INDICADAS

LÁMINA: 2 DE 16


SELLOS DE APROBACIÓN G.A.M.S.:

SELLOS ENTE COLEGADO:

PLANO DE UBICACION :

Esc. 1: 5000

DUCTEADO LUMINARIAS

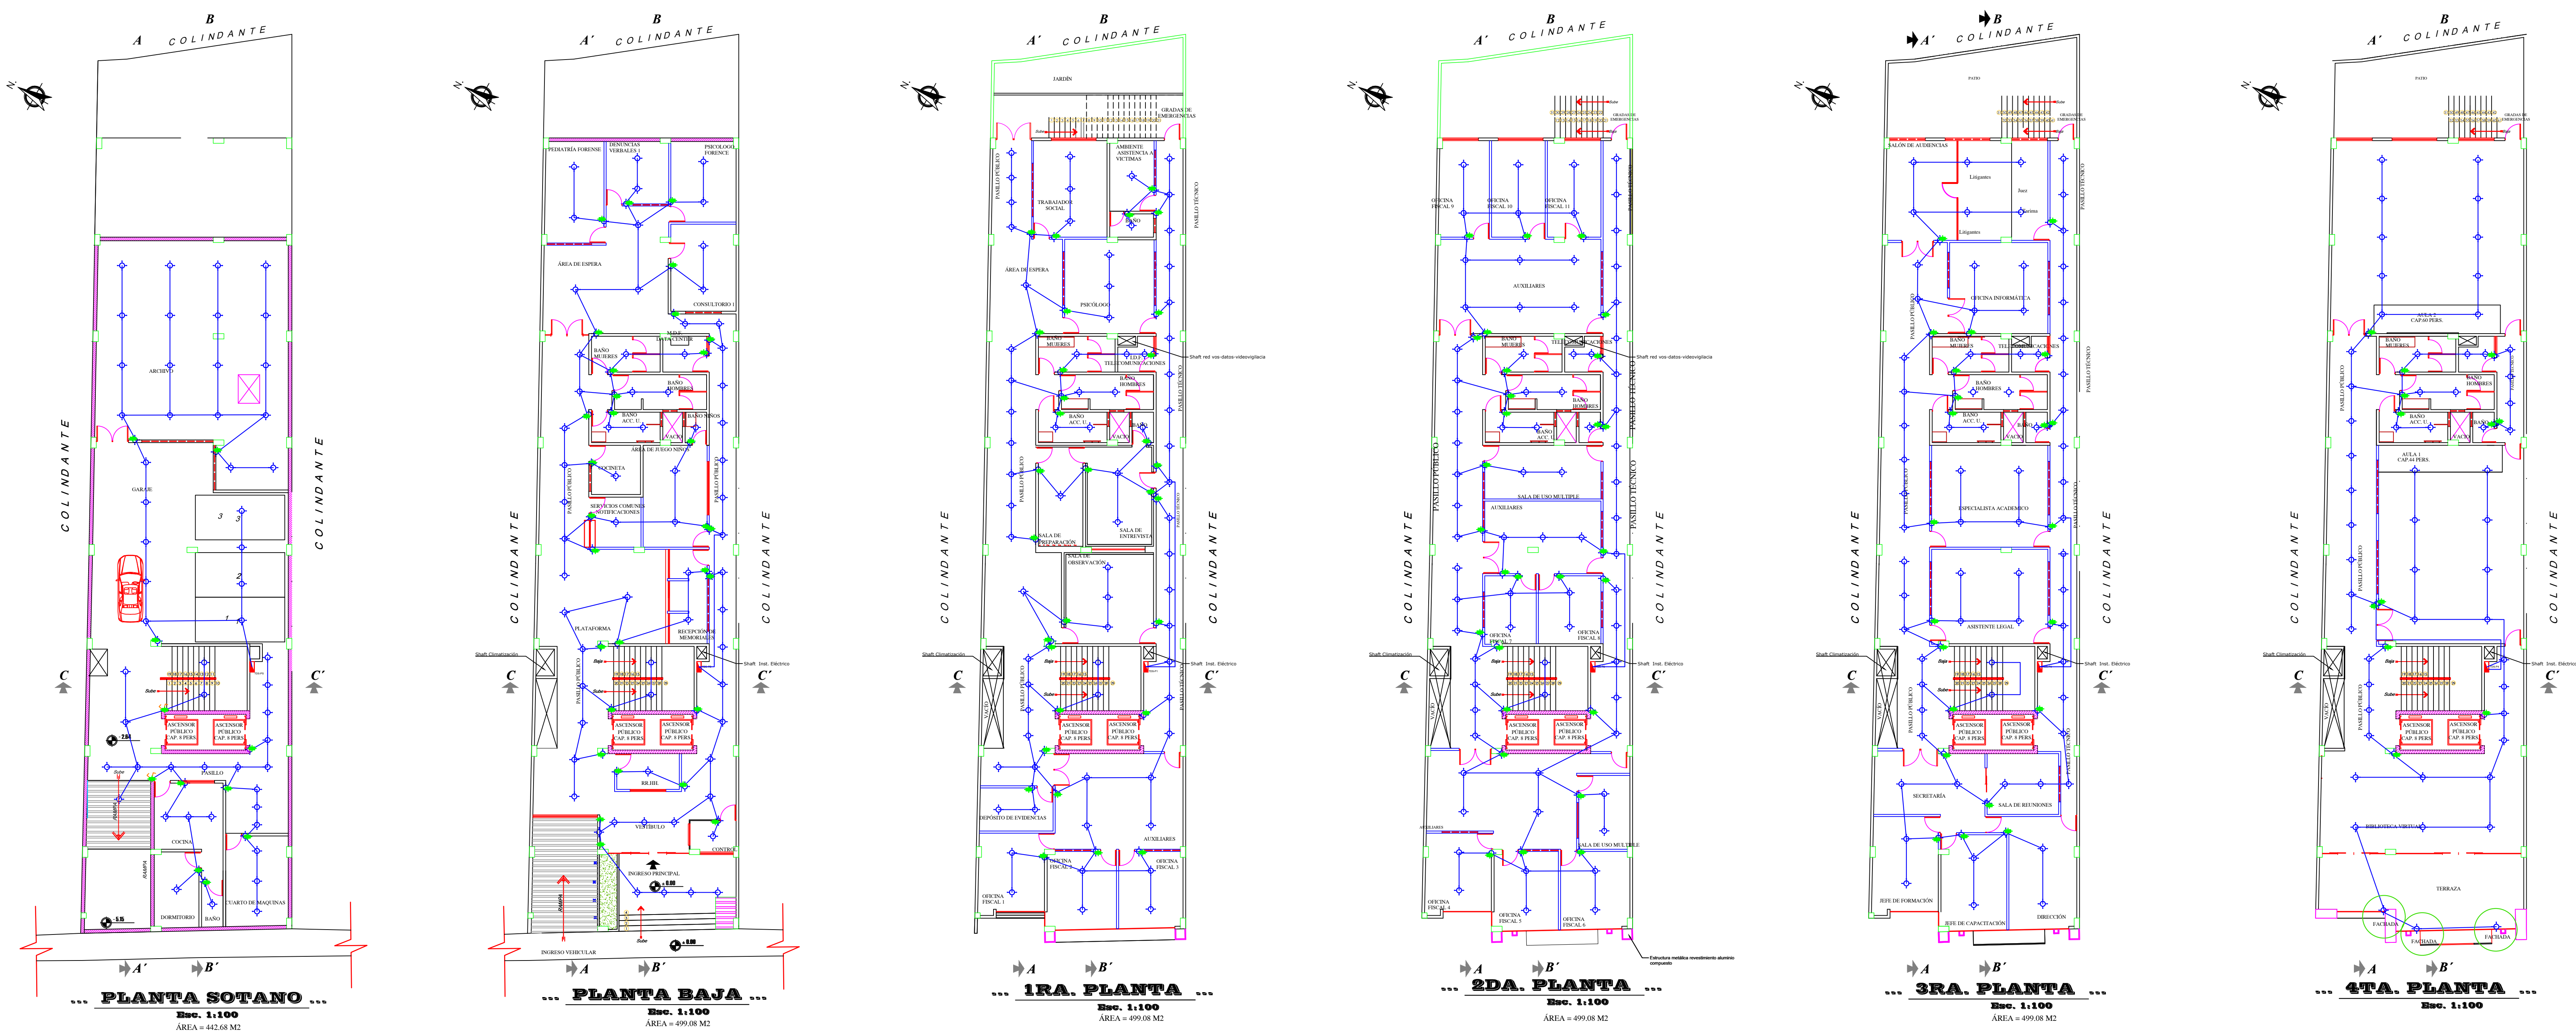

SIMBOLOGÍA	DESCRIPCIÓN
	Interruptor de Simple, h=1.25m.
	Interruptor conmutador, h=1.25m.
	Interruptor doble, h=1.25m.
	Caja Octogonal.
	Caja Rectangular.
	Ducteado de Iluminación, PVC - 3/4".
	Circuito de iluminación 1
	Circuito de iluminación 2
	Luminaria led 60 w
	Luminaria led 24 w
	Luminaria led 12 w
	Luminaria led 8 w

NOTAS:

REFERENCIAS

PLANOS:

INSTALACION ELECTRICA

PROYECTO:

DISENO ELECTRICO FISCALIA

PROPIETARIO:

FISCALIA

PROYECTISTA:

ING. JORGE FERNANDO POVEDA RUIZ

DIRECCION :

EDUARDO BERDECIO

CODIGO CATASTRAL	DISTRITO	MANZANA	LOTE
	007	0002	0016

SUP. TOTAL CONST:

2895.77 M2

FECHA: 05/09/2023

ESCALA INDICADAS

LÁMINA: 3 DE 16


SELLOS DE APROBACIÓN G.A.M.S.:

SELLOS ENTE COLEGIADO:

PLANO DE UBICACION :

Esp. 1: 8000

CIRCUITO DE TOMACORRIENTES

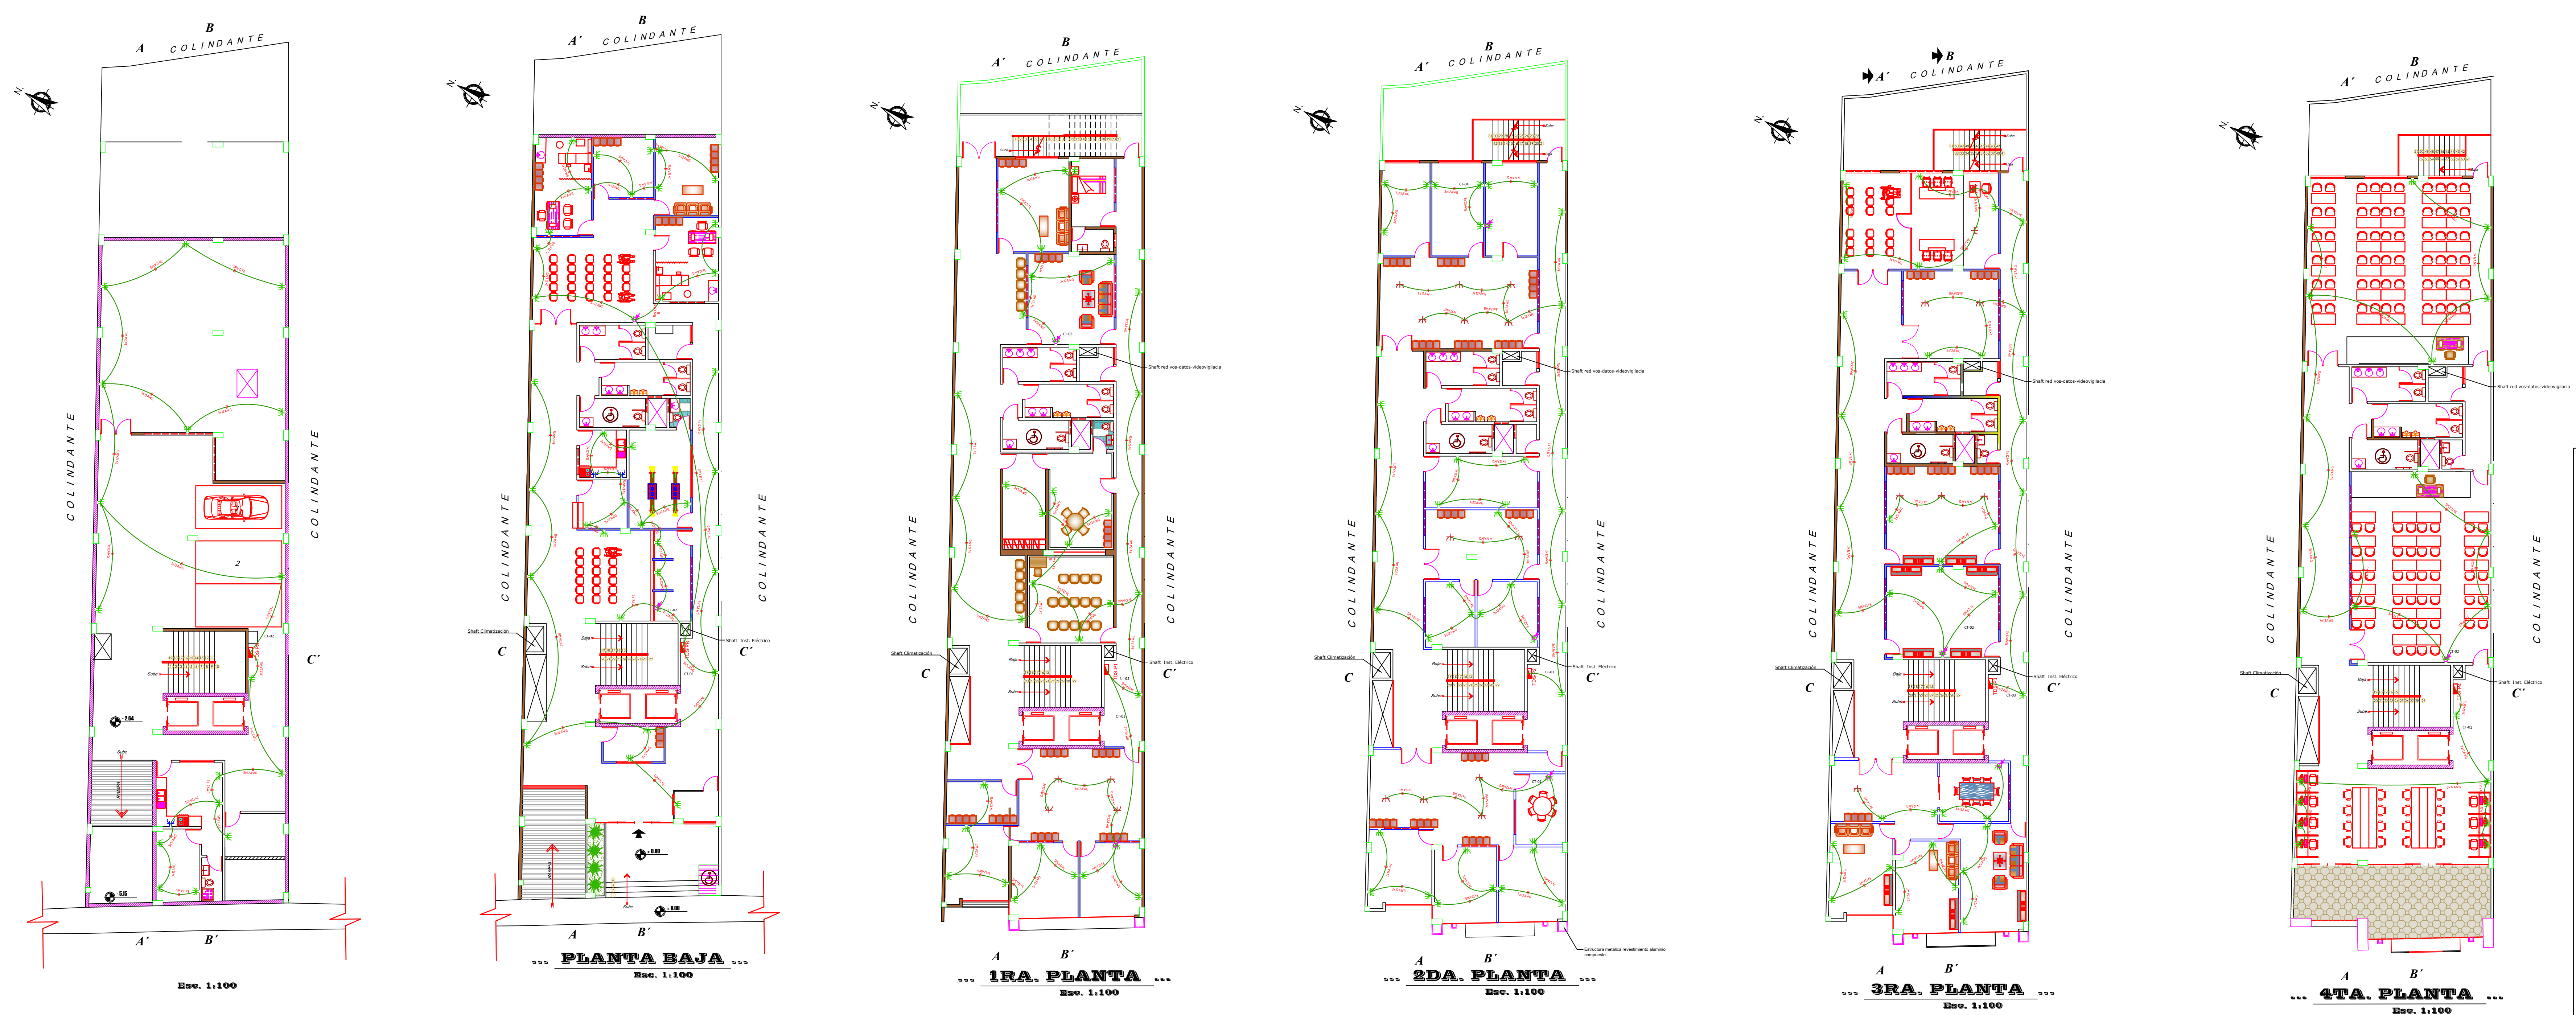

SIMBOLOGÍA	DESCRIPCIÓN
	Tablero de Distribución.
	Conductor con alimentacion desde arriba
	Toma normal a 0.3m
	Toma normal en suelo
	Caja Rectangular.
	Ducto PVC 3/4"
	Toma normal a 1.2m

NOTAS:

REFERENCIAS

PLANS:INSTALACION ELECTRICA

PROYECTO:
DISEÑO ELECTRICO FISCALIA

PROPIETARIO:
FISCALIA

PROYECTISTA:
ING. JORGE FERNANDO POVEDA RUIZ

DIRECCION :
EDUARDO BERDECIO

CODIGO CATASTRAL

007

0002

0016

SUP. TOTAL CONST:

2895.77 M2

FECHA: 05/09/2023

ESCALA INDICADAS

LÁMINA: 4 DE 16

SELOS DE APROBACIÓN G.A.M.S.:

SELOS ENTE COLEGIADO:

PLANO DE UBICACION :
Esp. 1: 5000

DUCTEADO DE TOMACORRIENTES



SIMBOLOGÍA	DESCRIPCIÓN
	Tablero de Distribución.
	Conductor con alimentacion desde arriba
	Toma normal a 0.3m
	Toma normal en suelo
	Caja Rectangular.
	Ducto PVC 3/4"
	Toma normal a 1.2m

NOTAS:

REFERENCIAS

PLANOS:

INSTALACION ELECTRICA

PROYECTO:

DISEÑO ELECTRICO FISCALIA

PROPIETARIO:

FISCALIA

PROYECTISTA:

ING. JORGE FERNANDO POVEDA RUIZ

DIRECCION :

EDUARDO BERDECIO

CODIGO CATASTRAL

007

0002

0016

SUP. TOTAL CONST:

2895.77 M2

FECHA: 05/09/2023

ESCALA INDICADAS

LÁMINA: 5 DE 16

Sellos de aprobación y colegiados






PLANO DE UBICACION :

Sellos de aprobación y colegiados

SELOS DE APROBACIÓN G.A.M.S.:

SELOS ENTE COLEGIADO:

CIRCUITO DE TOMACORRIENTES REGULADAS

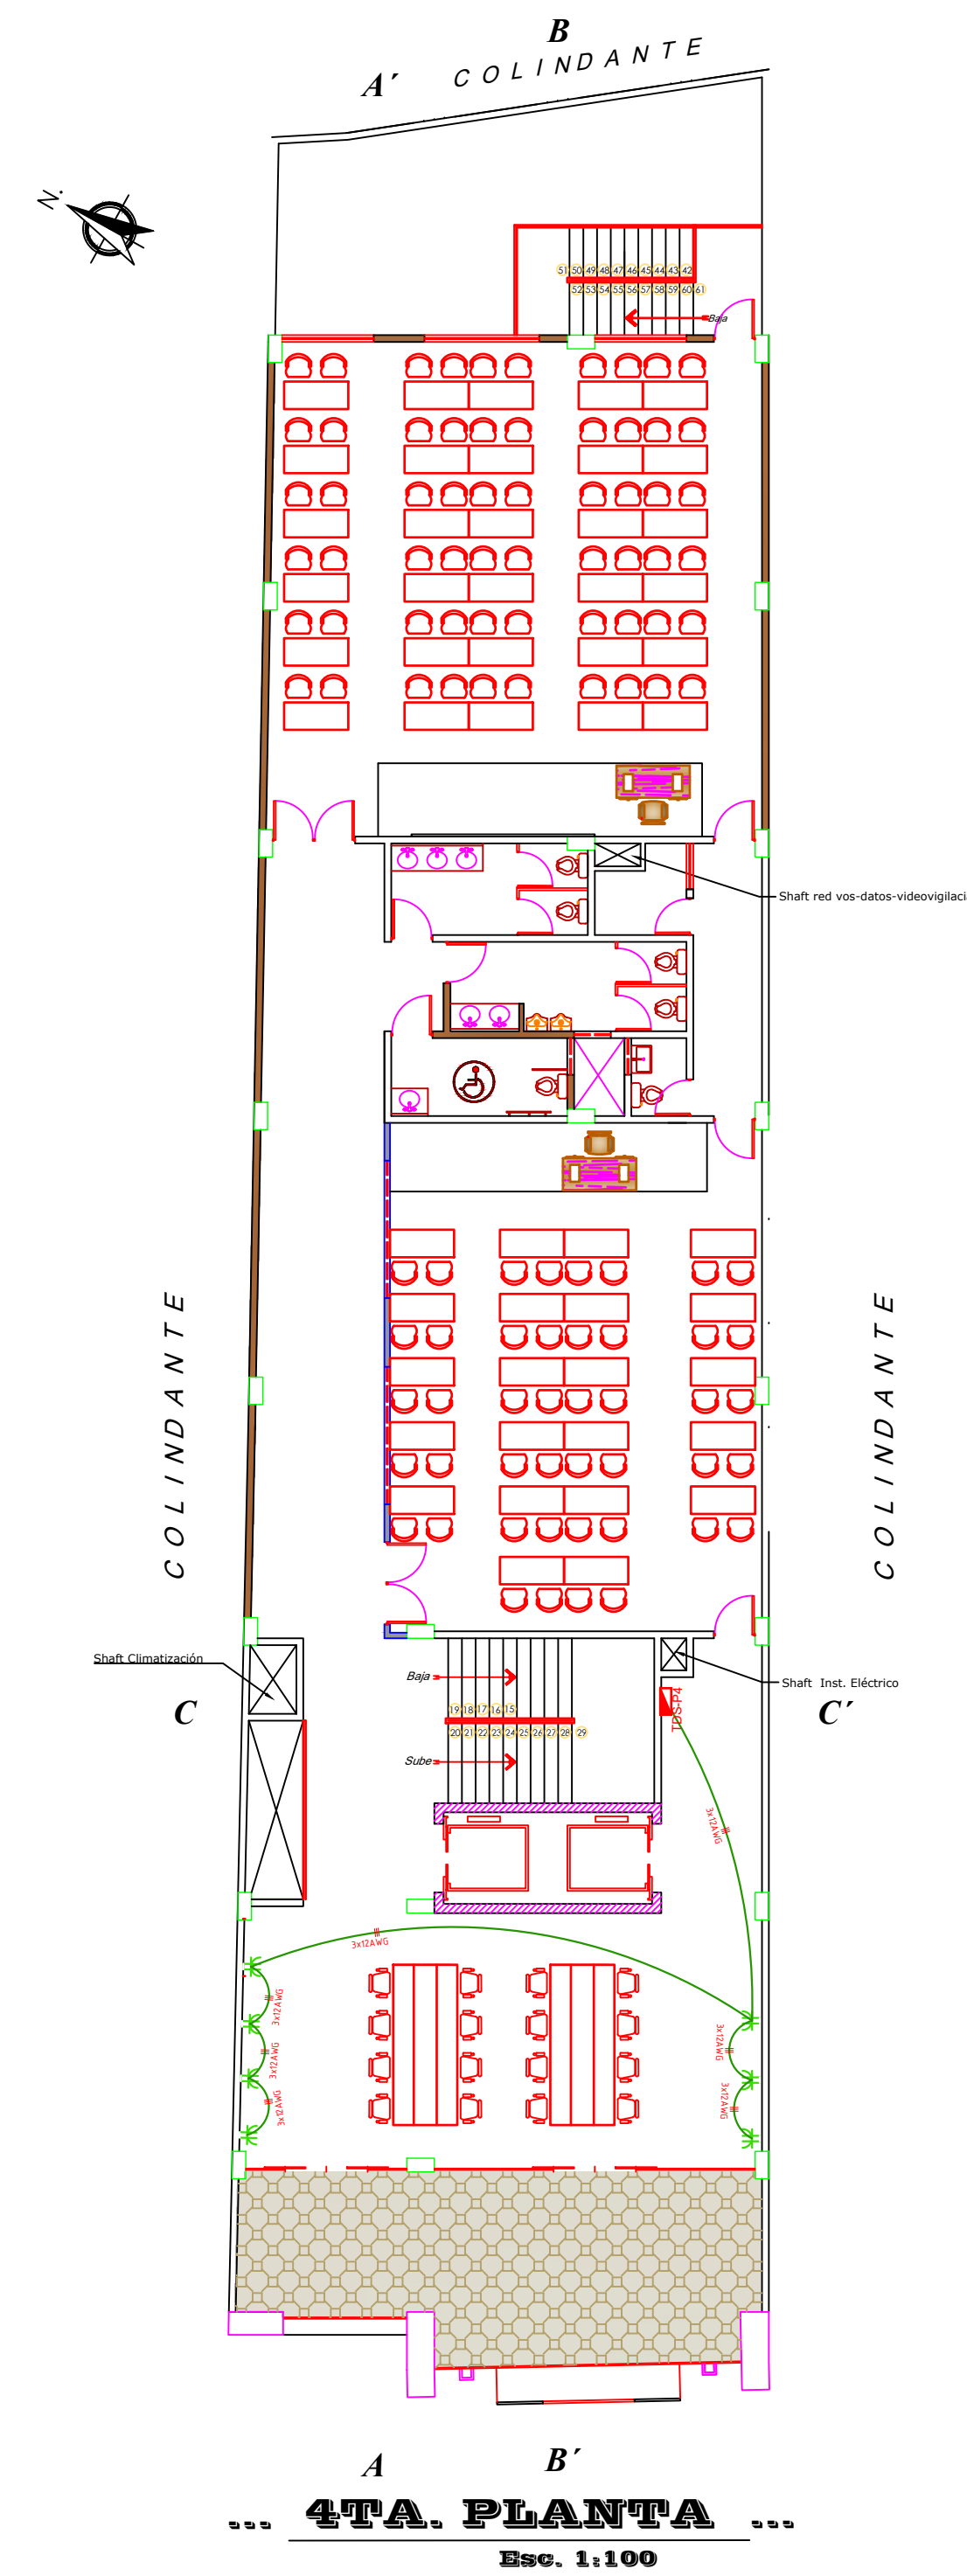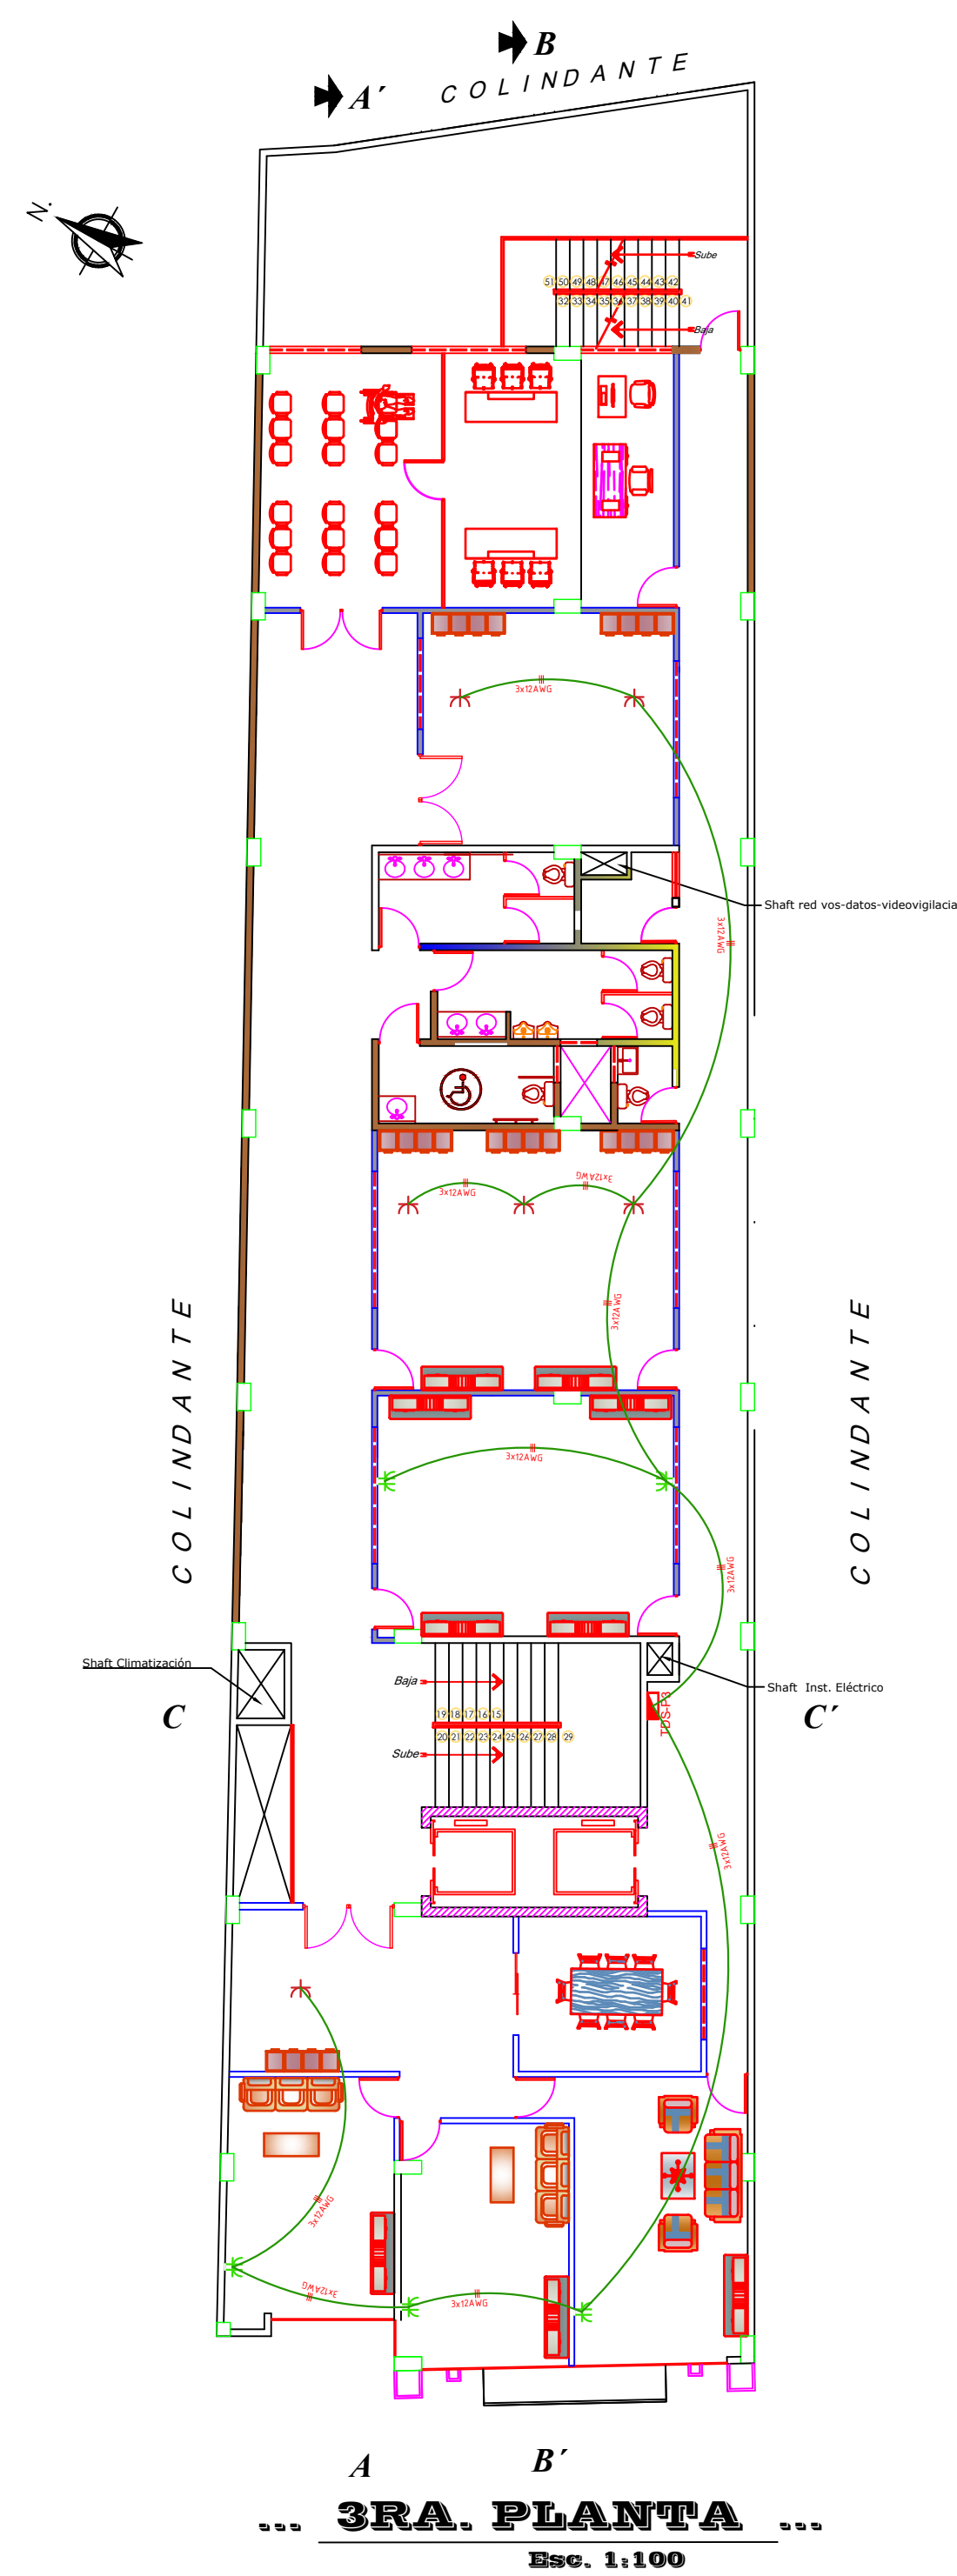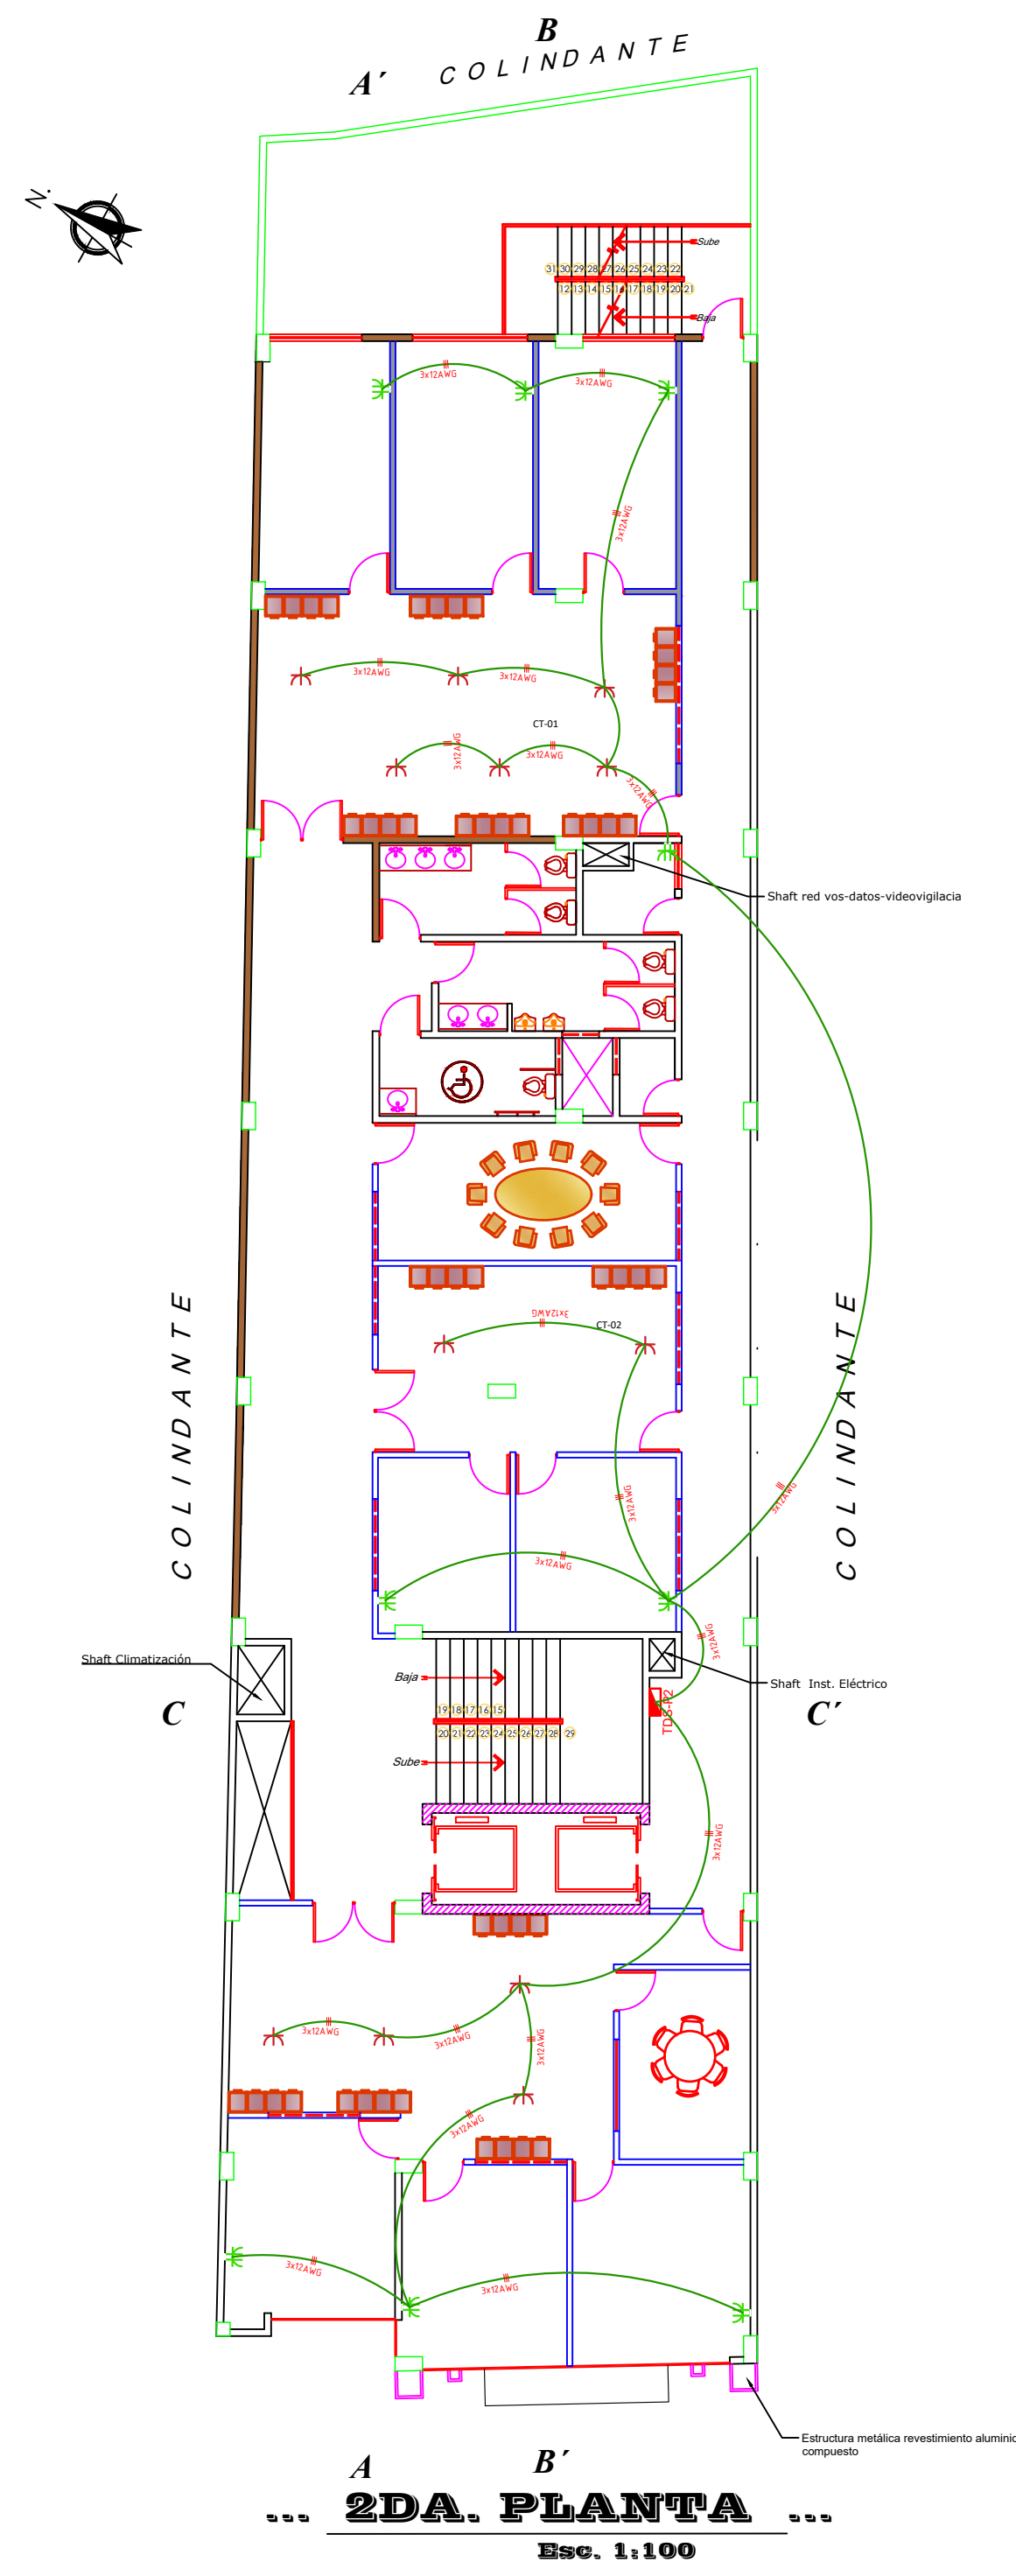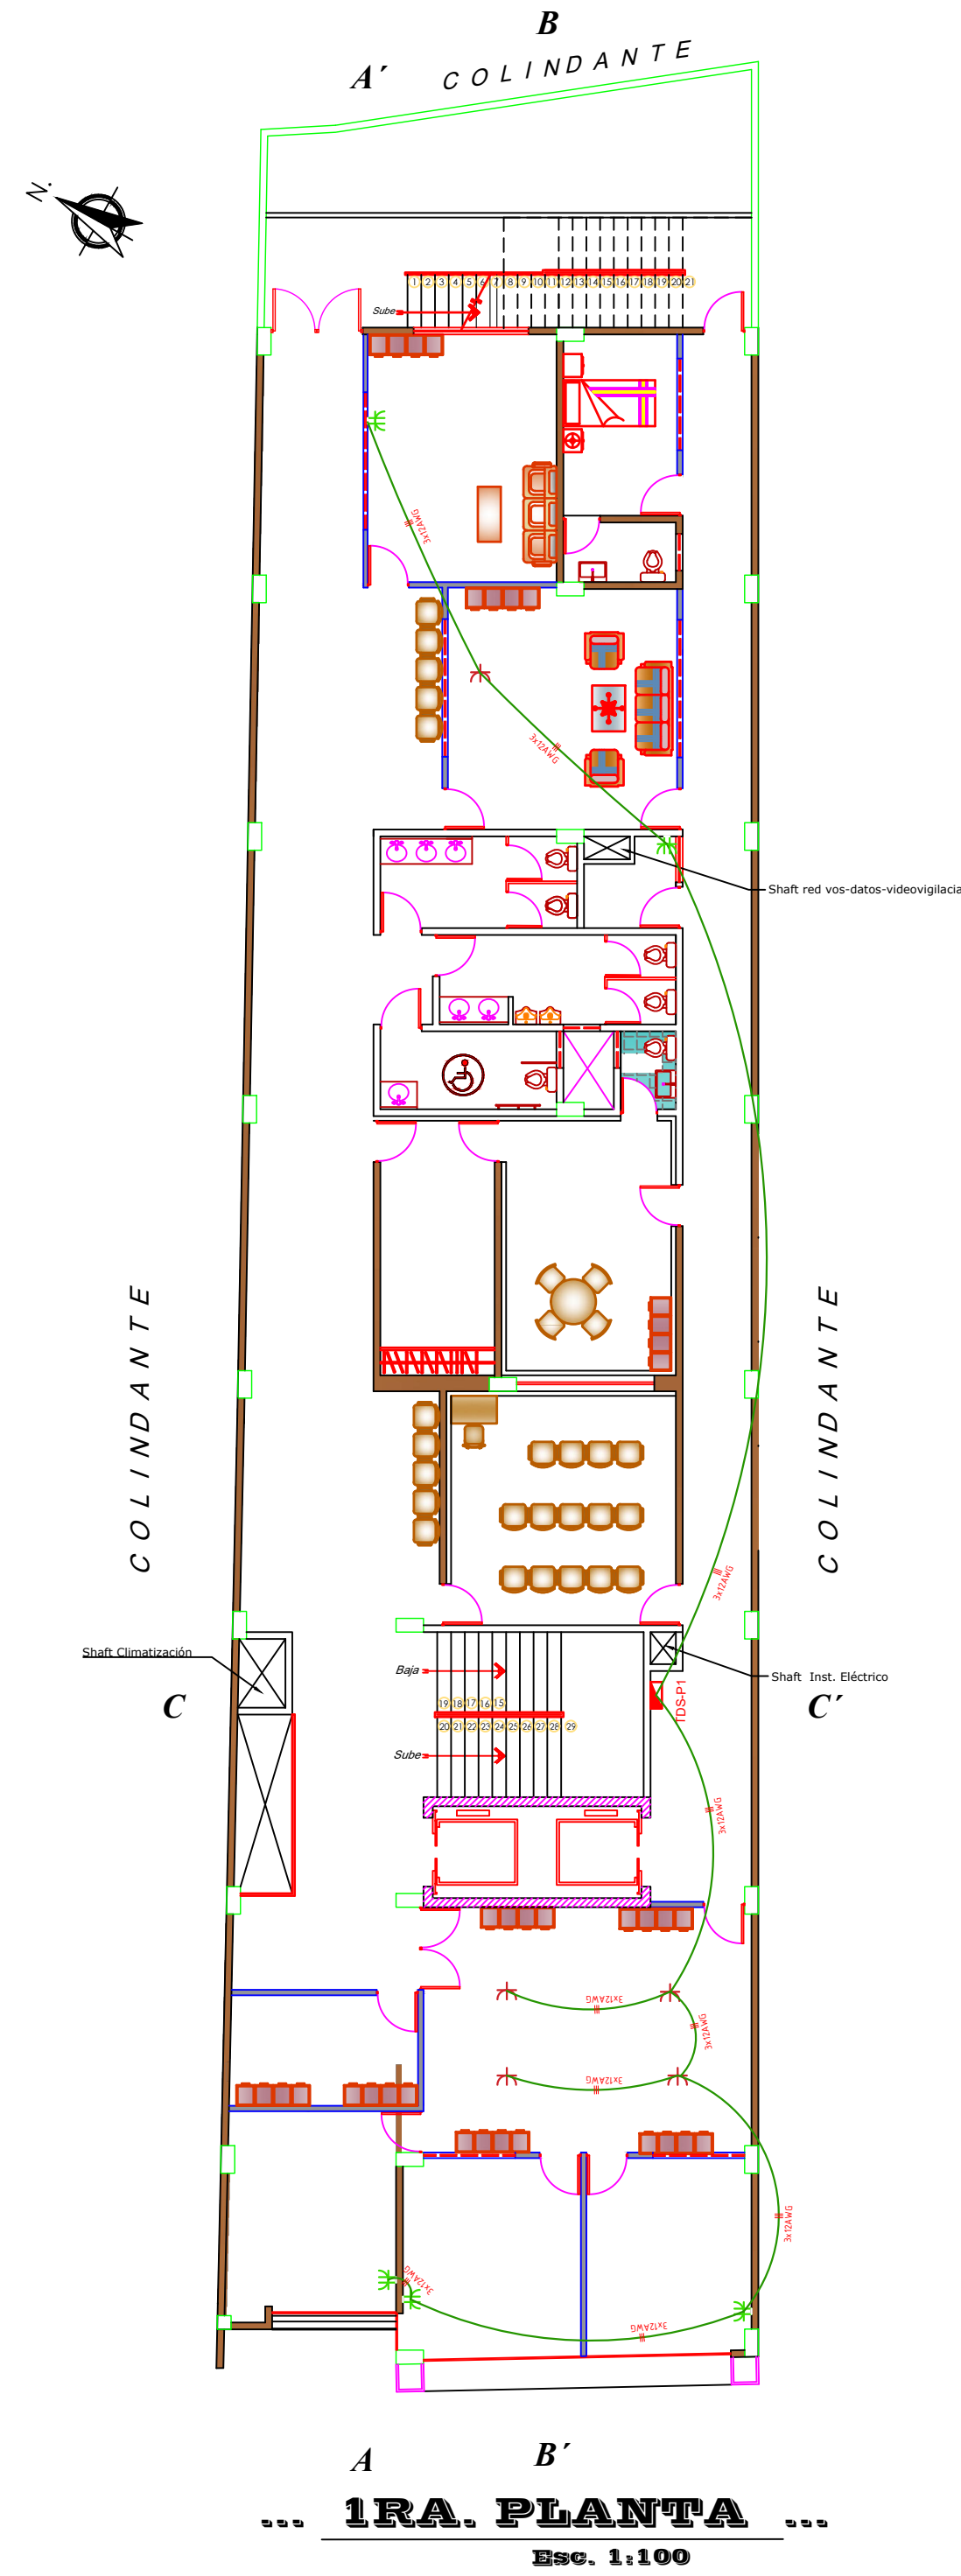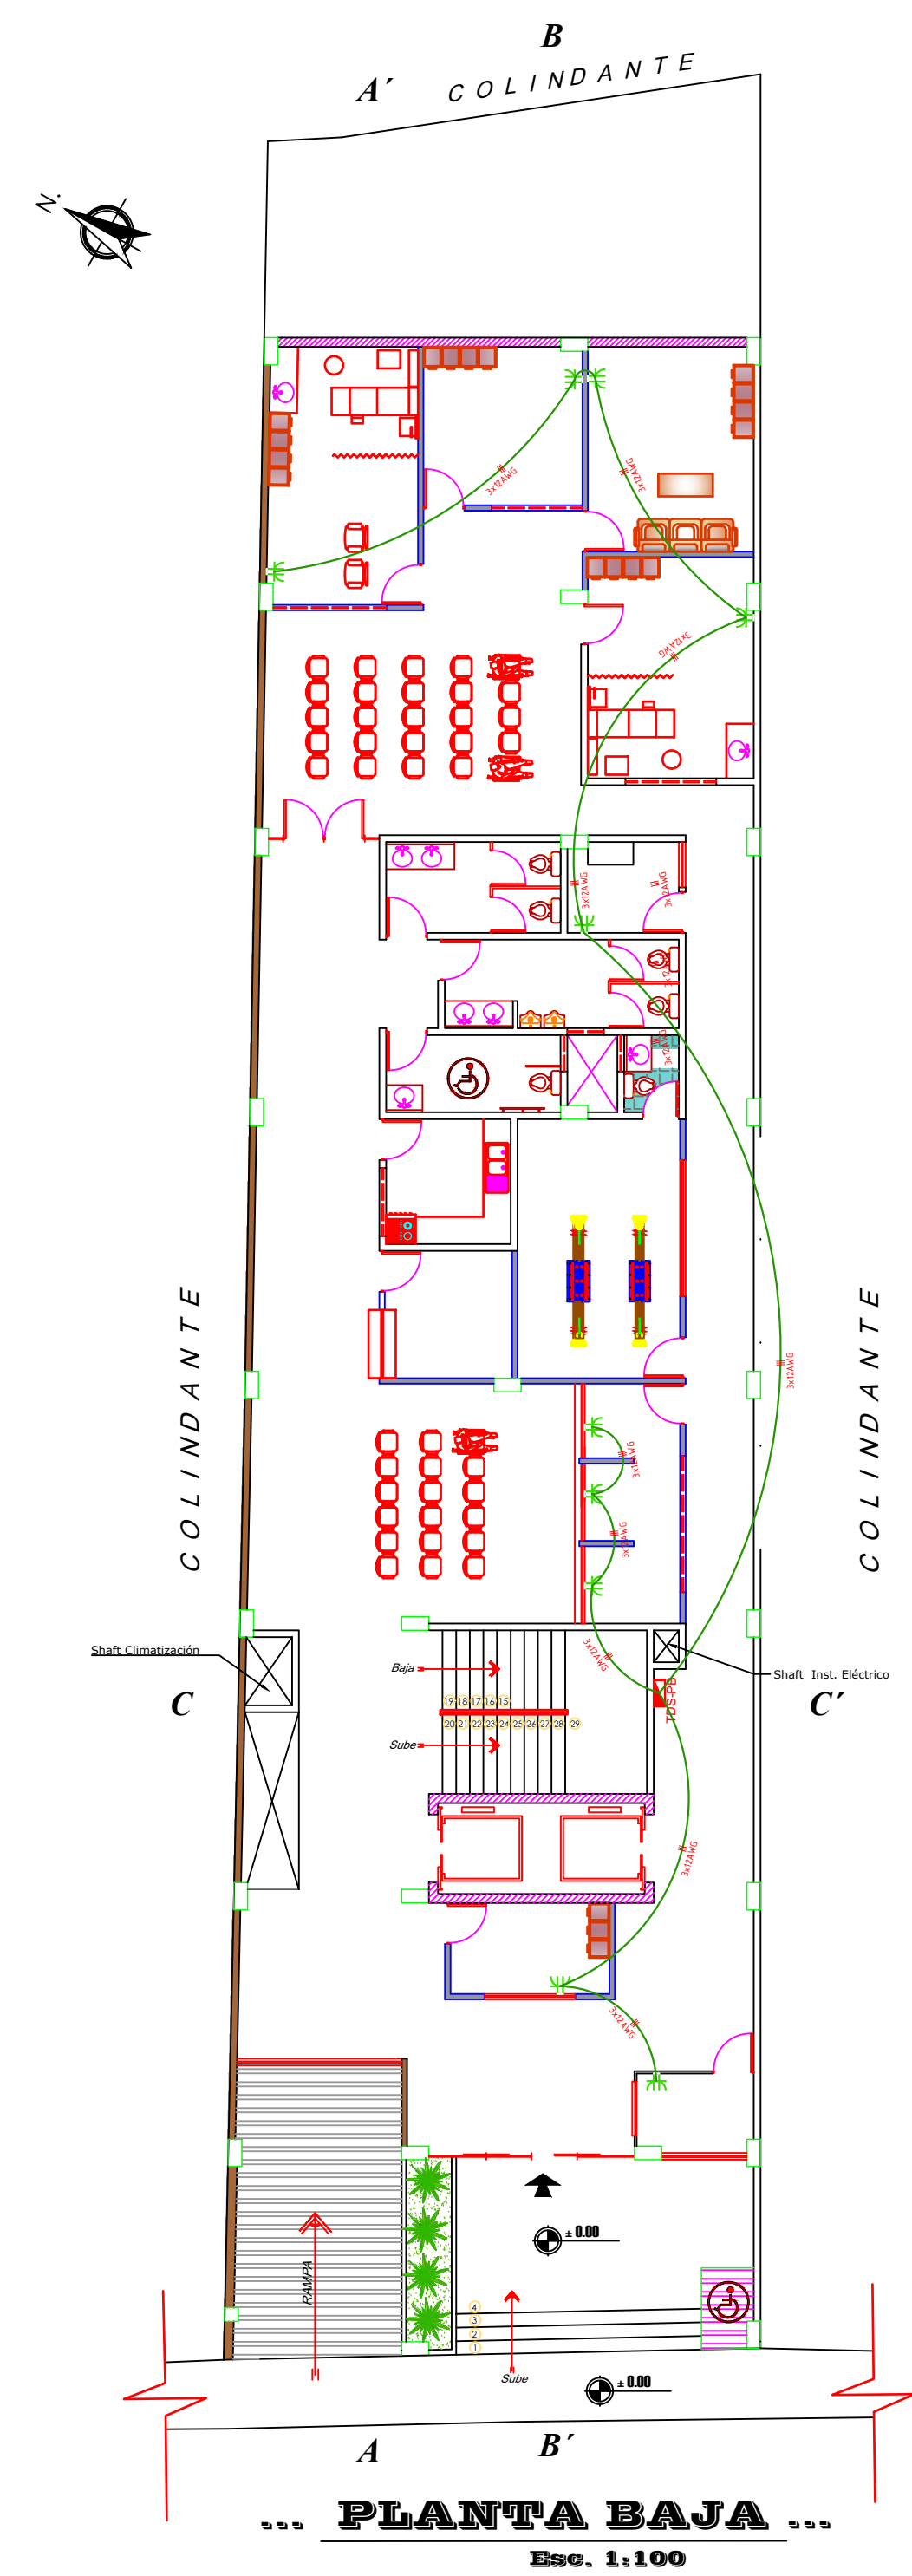

SIMBOLOGÍA	DESCRIPCIÓN
	Tablero de Distribución.
	Conductor con alimentacion desde arriba
	Toma regulada a 0.3m
	Toma regulada en suelo
	Caja Rectangular.
	Ducto PVC 3/4"

NOTAS:

REFERENCIAS

PLANOS:

INSTALACION ELECTRICA

PROYECTO:

DISEÑO ELECTRICIO FISCALIA

PROPIETARIO:

FISCALIA

PROYECTISTA:

ING. JORGE FERNANDO POVEDA RUIZ

DIRECCION :

EDUARDO BERDECIO

CODIGO CATASTRAL

00700020016

SUP. TOTAL CONST:

2895.77 M2

FECHA: 05/09/2023

ESCALA INDICADAS

LÁMINA: 6 DE 16






SELLOS DE APROBACIÓN G.A.M.S.:

SELLOS ENTE COLEGADO:

PLANO DE UBICACION :

DUCTEADO DE TOMACORRIENTES REGULADAS

SIMBOLOGÍA	DESCRIPCIÓN
	Tablero de Distribución.
	Conductor con alimentacion desde arriba
	Toma regulada a 0.3m
	Toma regulada en suelo
	Caja Rectangular.
	Ducto PVC 3/4"

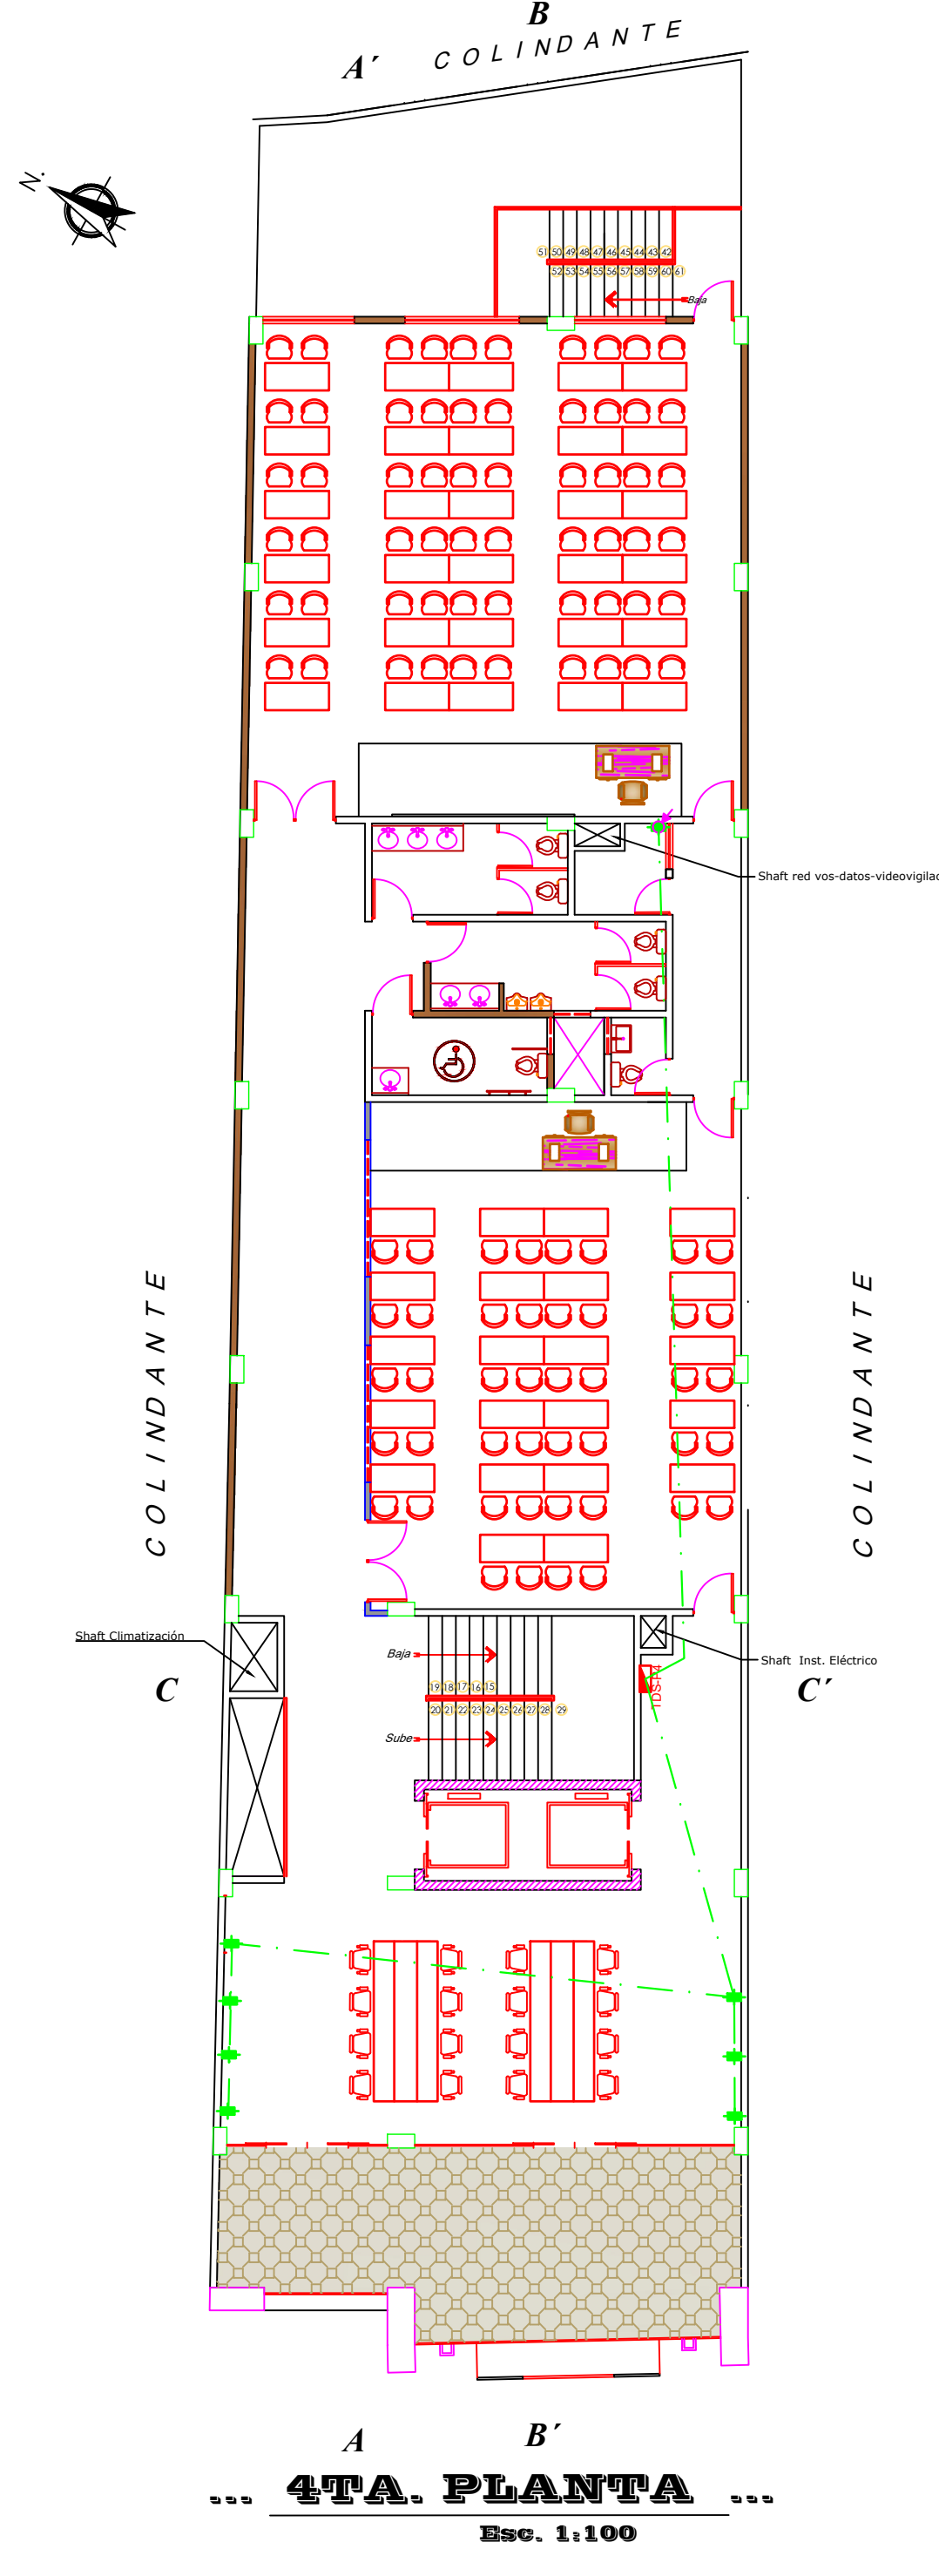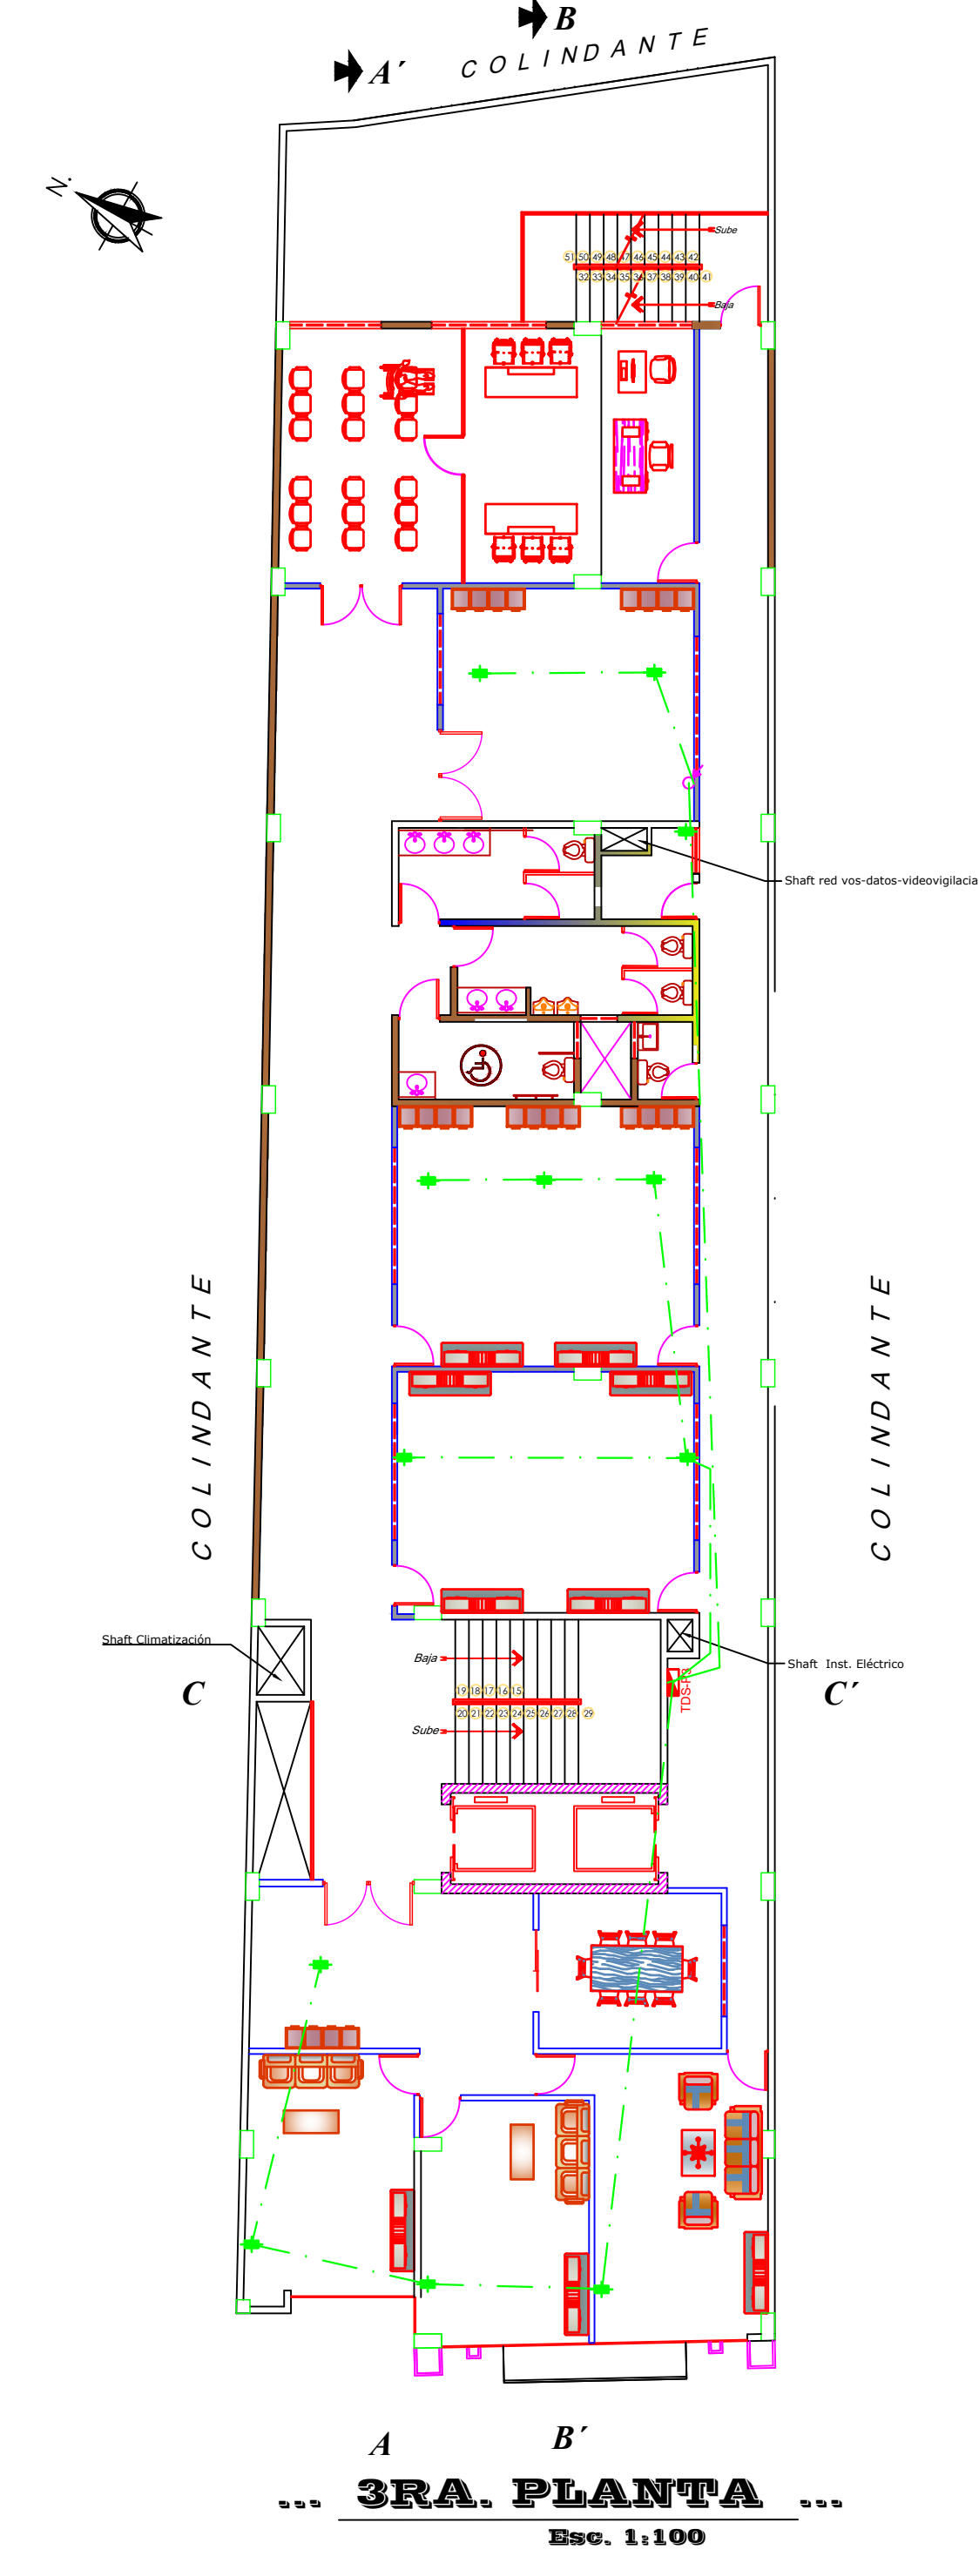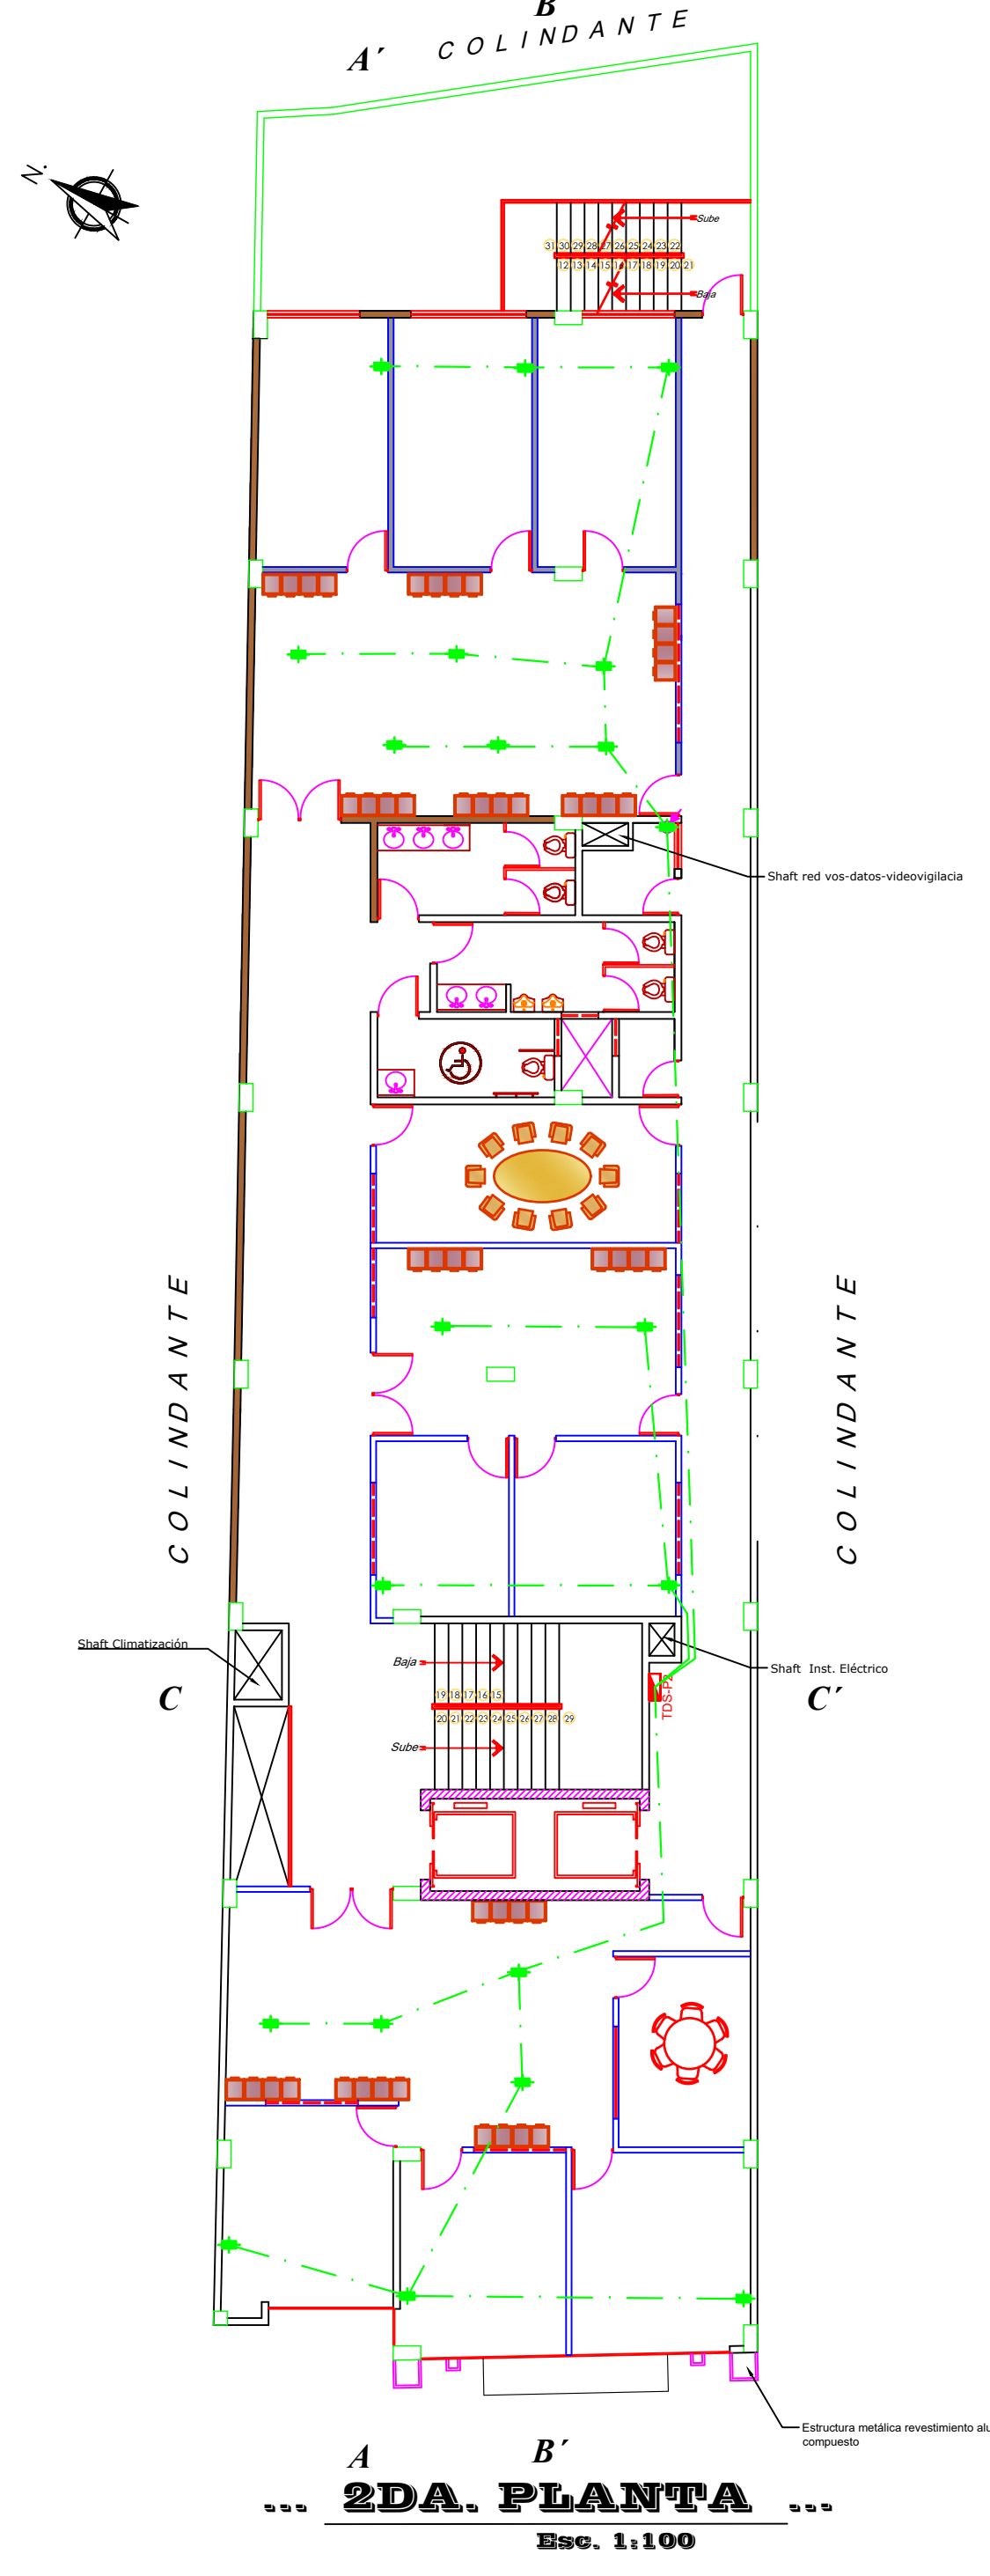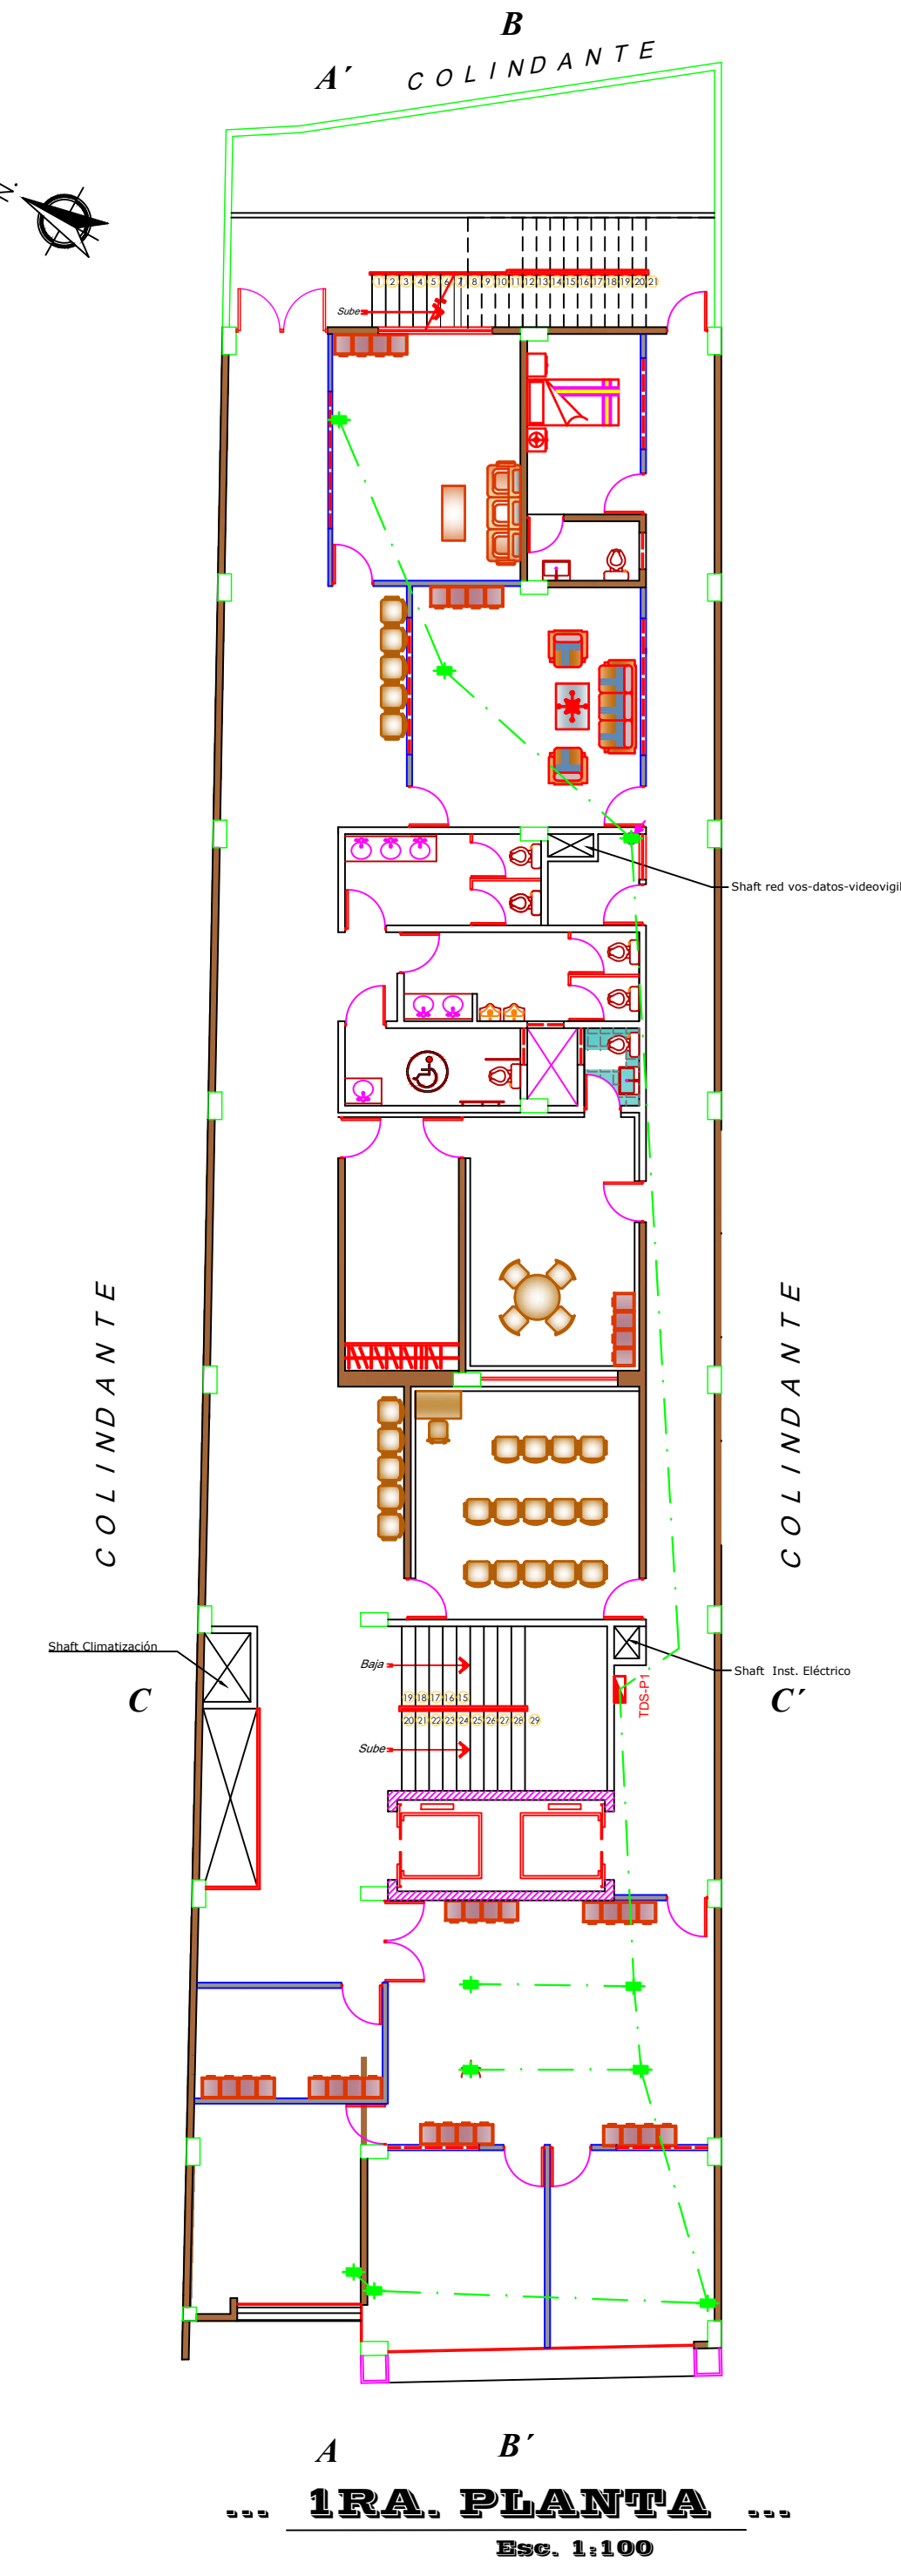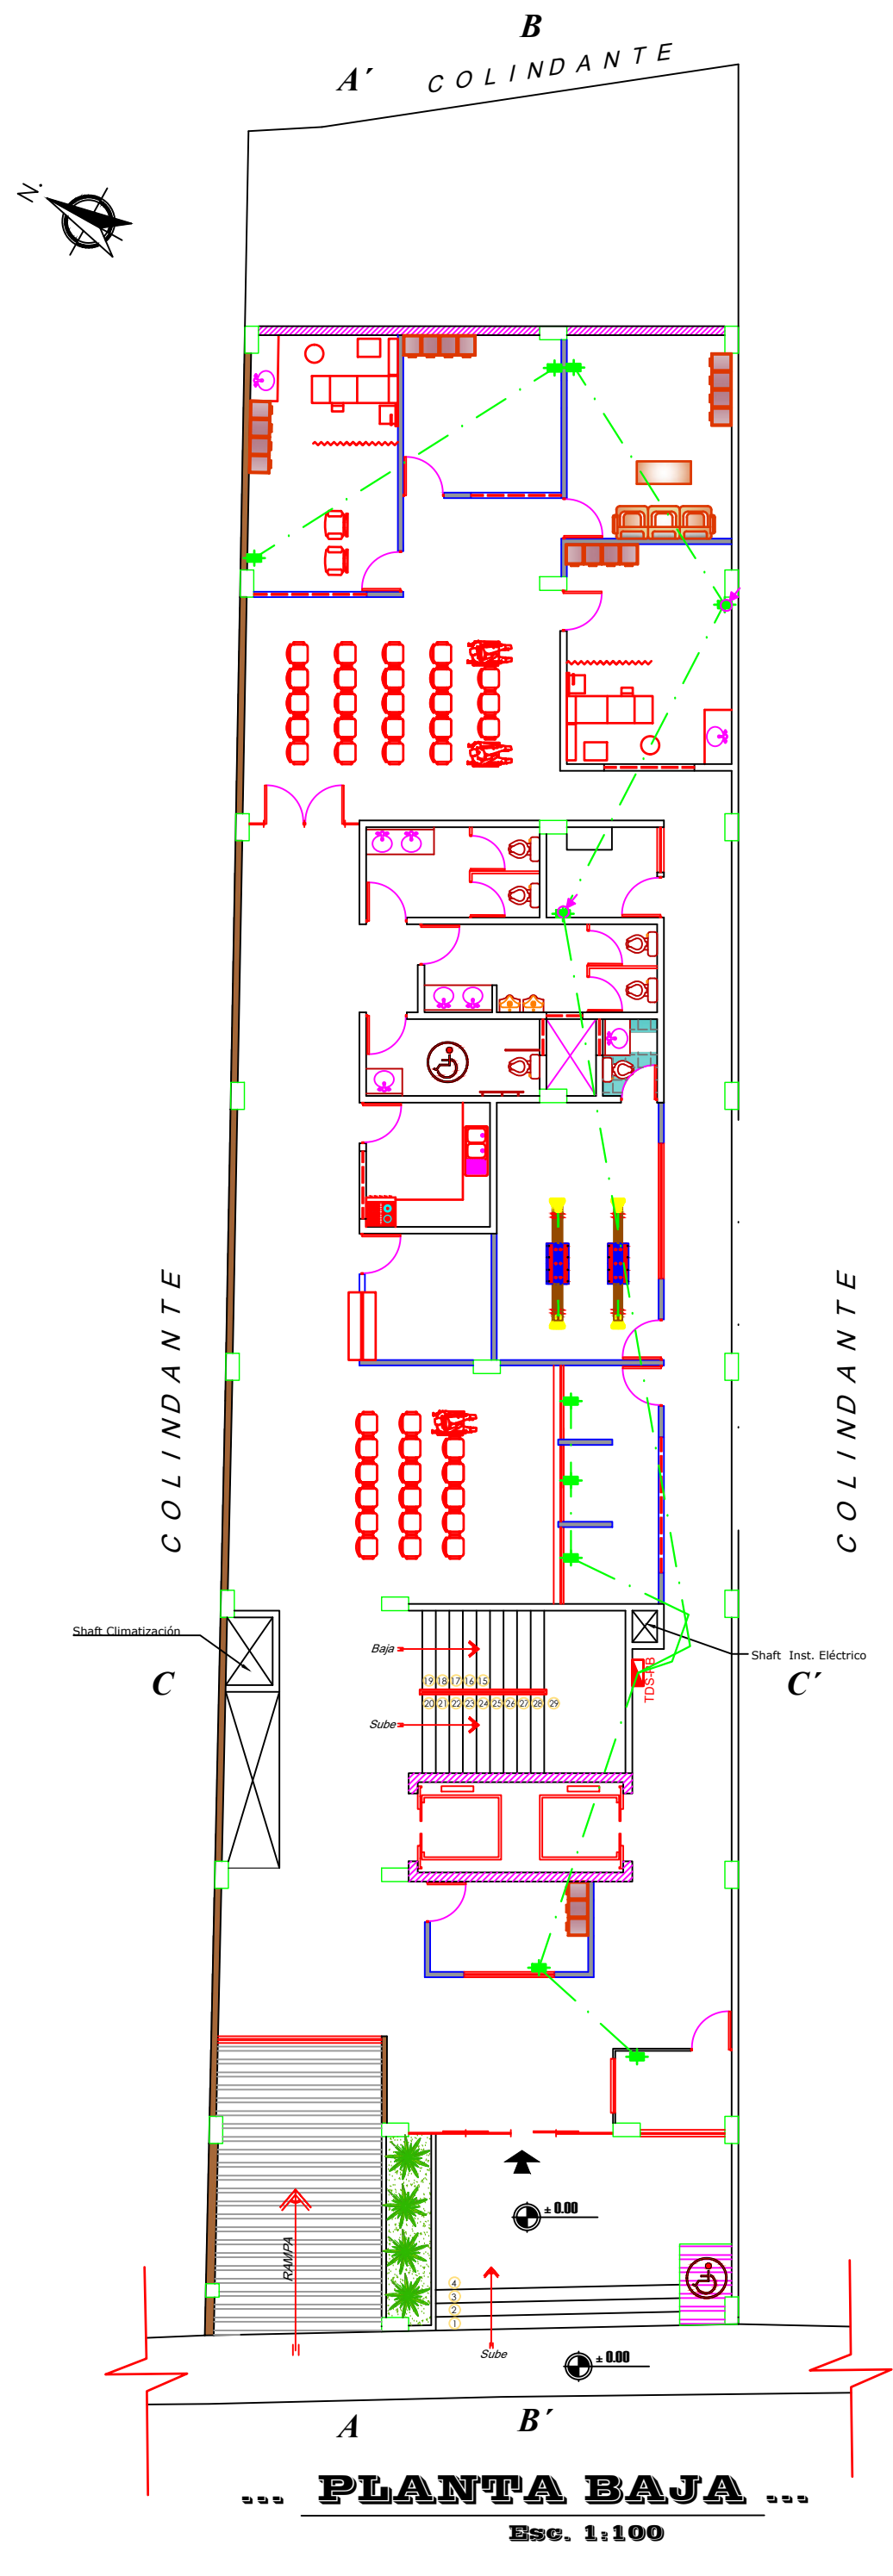

NOTAS:

REFERENCIAS

PLANOS:
INSTALACION ELECTRICA

PROYECTO:
DISEÑO ELECTRICO FISCALIA

PROPIETARIO:
FISCALIA

PROYECTISTA:
ING. JORGE FERNANDO POVEDA RUIZ

DIRECCION :
EDUARDO BERDECIO

CODIGO CATASTRAL	DISTRITO	MANZANA	LOTE
	007	0002	0016

SUP. TOTAL CONST: 2895.77 M2

FECHA: 05/09/2023


ESCALA INDICADAS: LÁMINA: 7 DE 16

SELLOS DE APROBACIÓN G.A.M.S.:

PLANO DE UBICACION :
Esc. 1: 5000

SELLOS ENTE COLEGADO:

CIRCUITOS DE FUERZAS

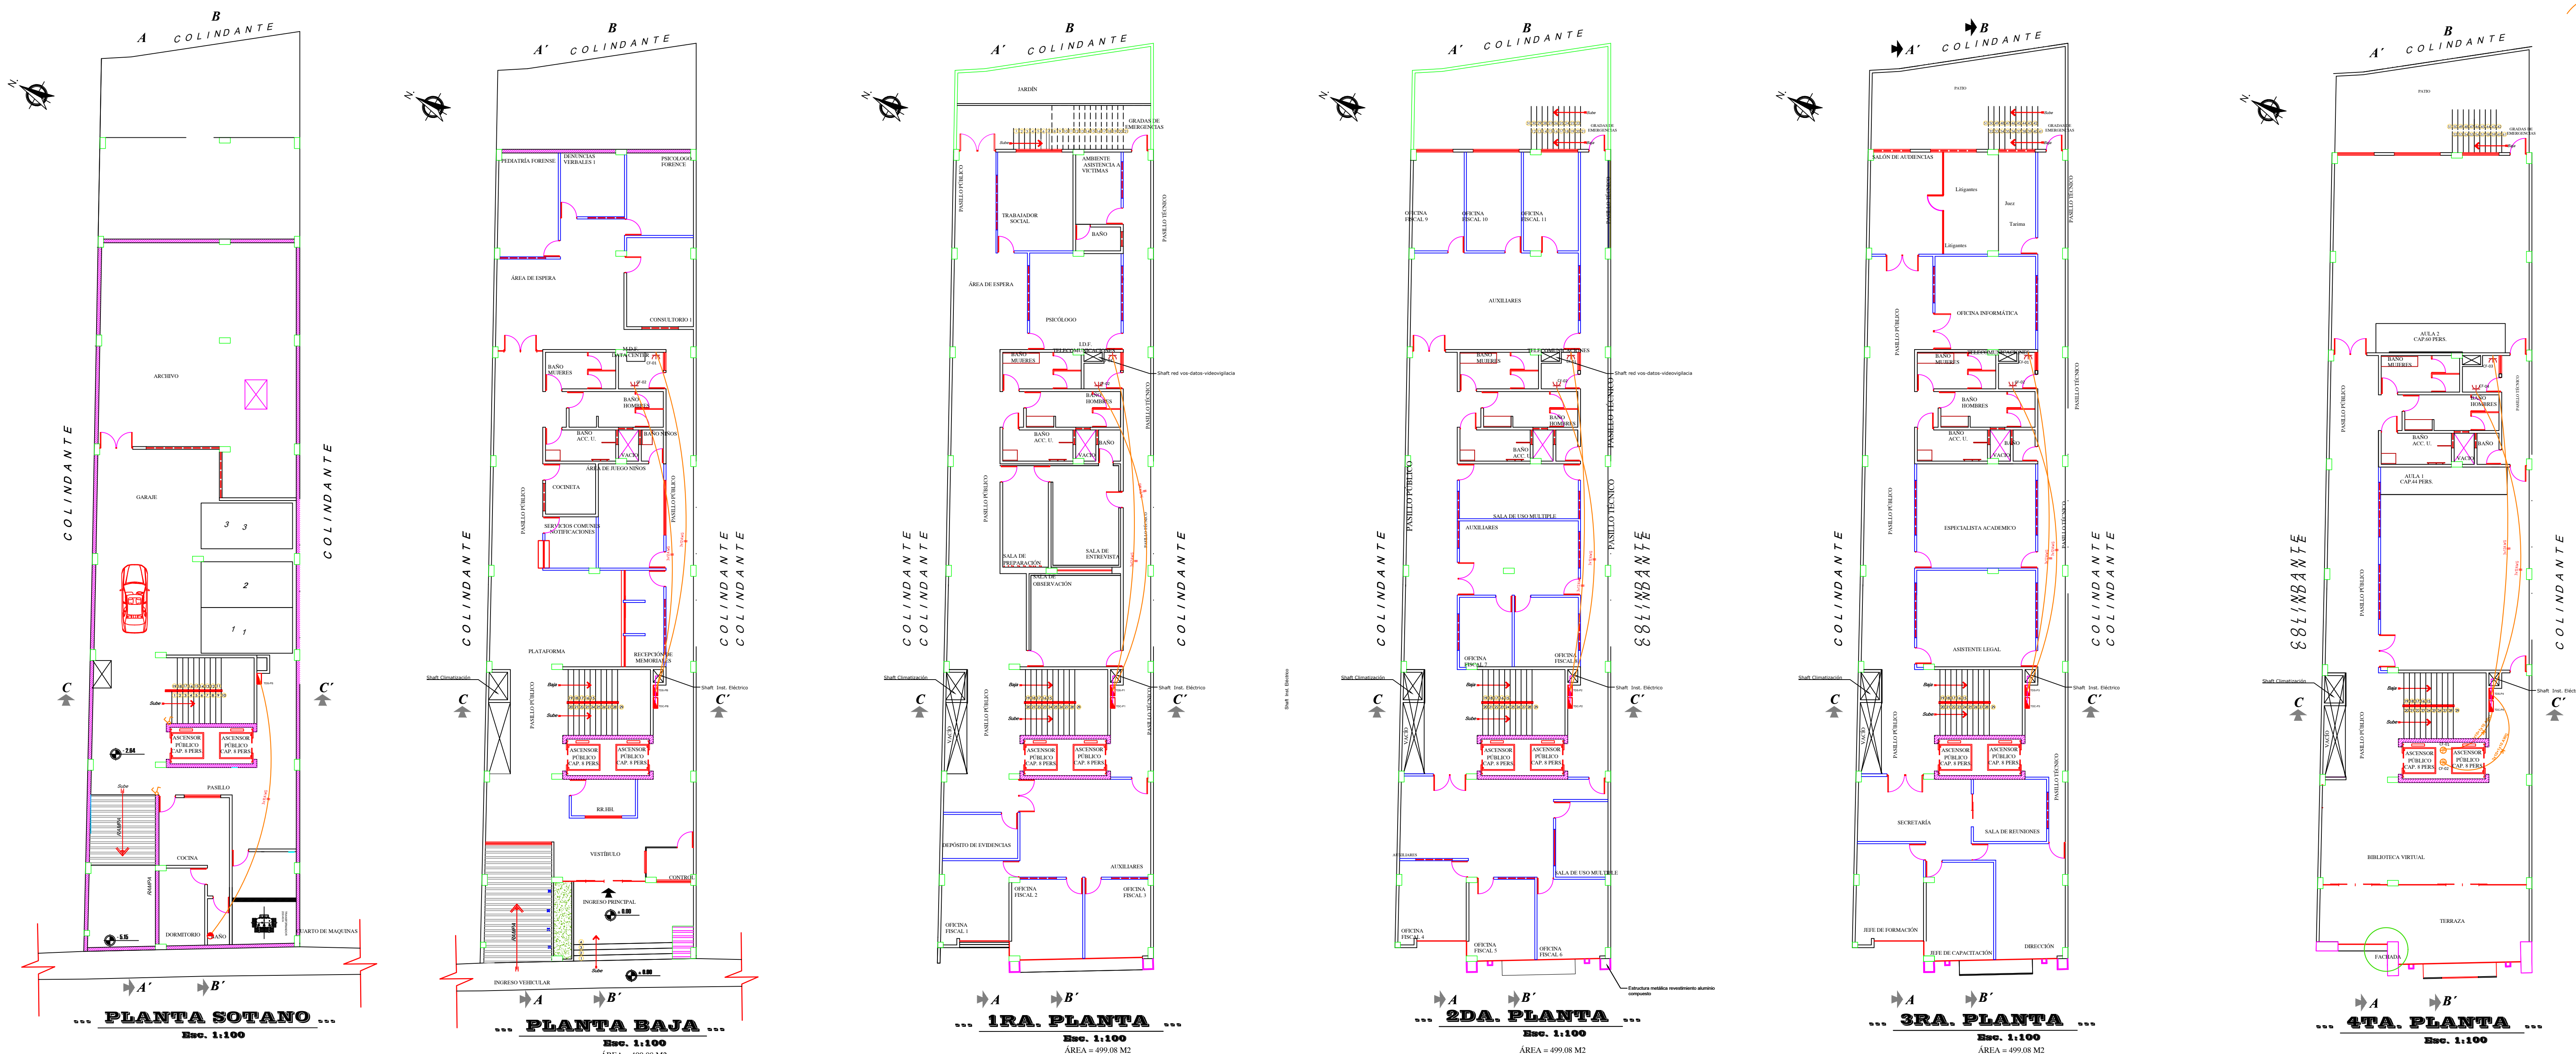

SIMBOLOGÍA	DESCRIPCIÓN
	Tomacorriente Doble Schuko + Tierra, h=1,3 m.
	Toma de Fuerza Monofásico + Tierra.
	Ducteado de Fuerza, PVC - 3/4".
	Circuito de fuerzas
	Toma de Fuerza Trifásico + Tierra.

NOTAS:

REFERENCIAS

PLANOS:

INSTALACION ELECTRICA

PROYECTO:
DISEÑO ELECTRICO FISCALIA

PROPIETARIO:
FISCALIA

PROYECTISTA:
ING. JORGE FERNANDO POVEDA RUIZ

DIRECCION :
EDUARDO BERDECIO

CODIGO CATASTRAL: 007 0002 0016

SUP. TOTAL CONST: 2895.77 M2


FECHA: 05/09/2023

ESCALA INDICADAS: LÁMINA: 8 DE 16

SELLOS DE APROBACIÓN G.A.M.S.:




PLANO DE UBICACION :

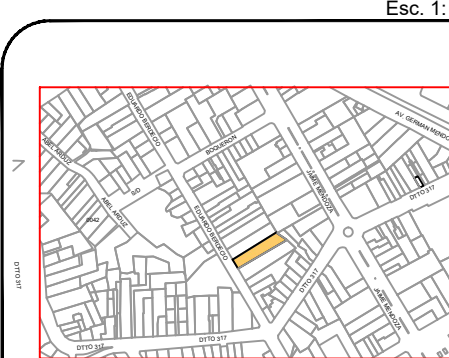

SELLOS ENTE COLEGADO:

DUCTEADO FUERZAS

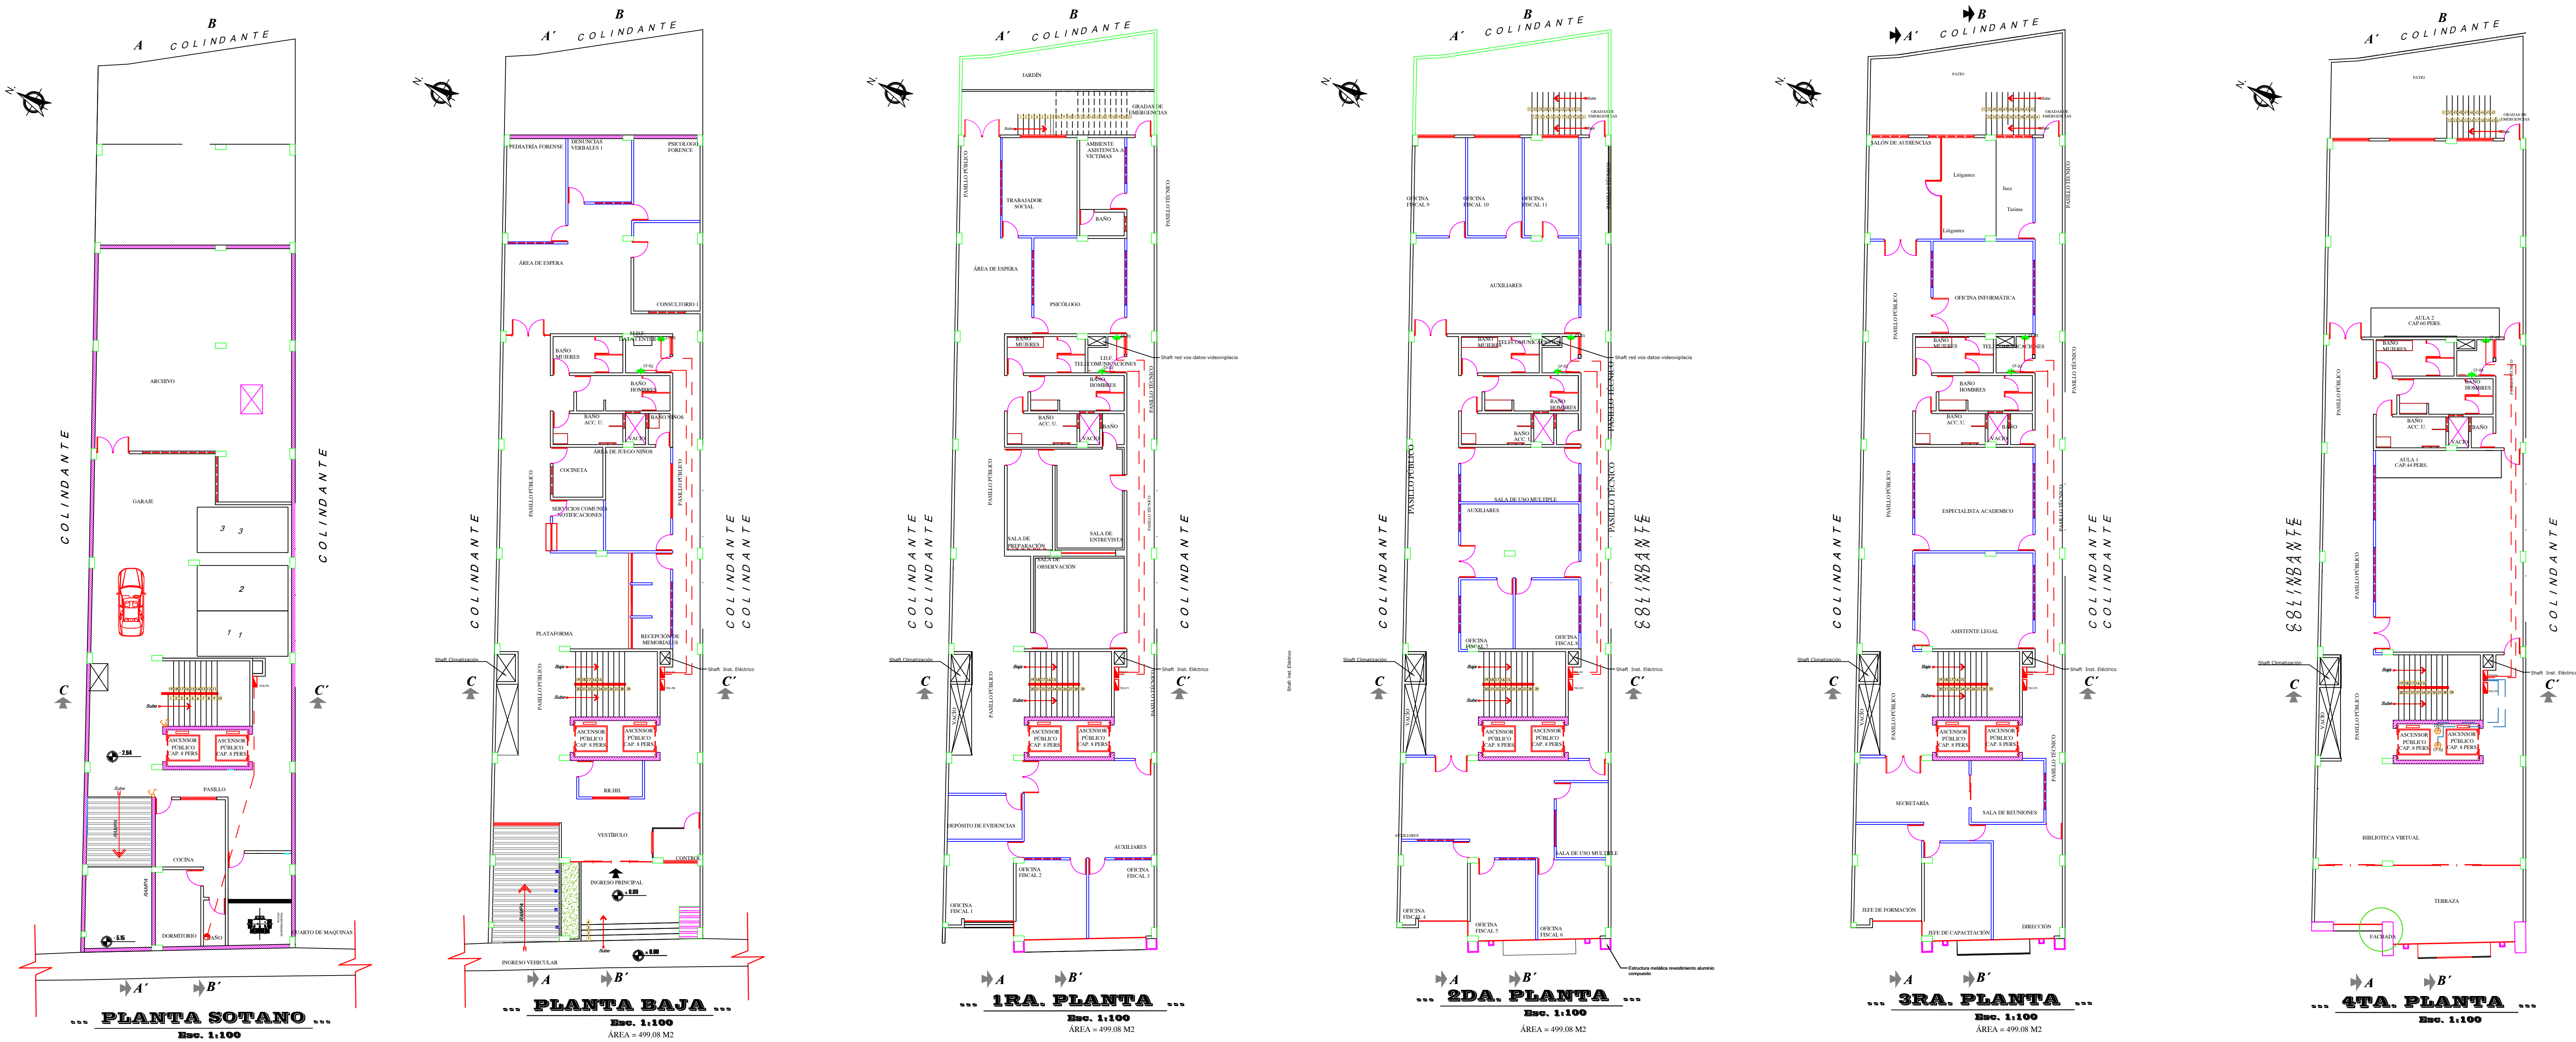

SIMBOLOGÍA	DESCRIPCIÓN
	Tomacorriente Doble Schuko + Tierra, h=1,3 m.
	Toma de Fuerza Monofásico + Tierra.
	Ducteado de Fuerza, PVC - 3/4".
	Ducteado de Fuerza, PVC - 1".
	Circuito de fuerzas
	Toma de Fuerza Trifásico + Tierra.

NOTAS:

REFERENCIAS

PLANOS: INSTALACION ELECTRICA

PROYECTO: DISEÑO ELECTRICO FISCALIA

PROPIETARIO: FISCALIA

PROYECTISTA: ING. JORGE FERNANDO POVEDA RUIZ

DIRECCION : EDUARDO BERDECIO

CODIGO CATASTRAL: 007 0002 0016

SUP. TOTAL CONST: 2895.77 M2

FECHA: 05/09/2023

ESCALA INDICADAS: LÁMINA: 9 DE 16

SELLOS DE APROBACIÓN G.A.M.S.:




PLANO DE UBICACION :



SELLOS ENTE COLEGADO:

CIRCUITO DE TOMA PARA CLIMATIZACION

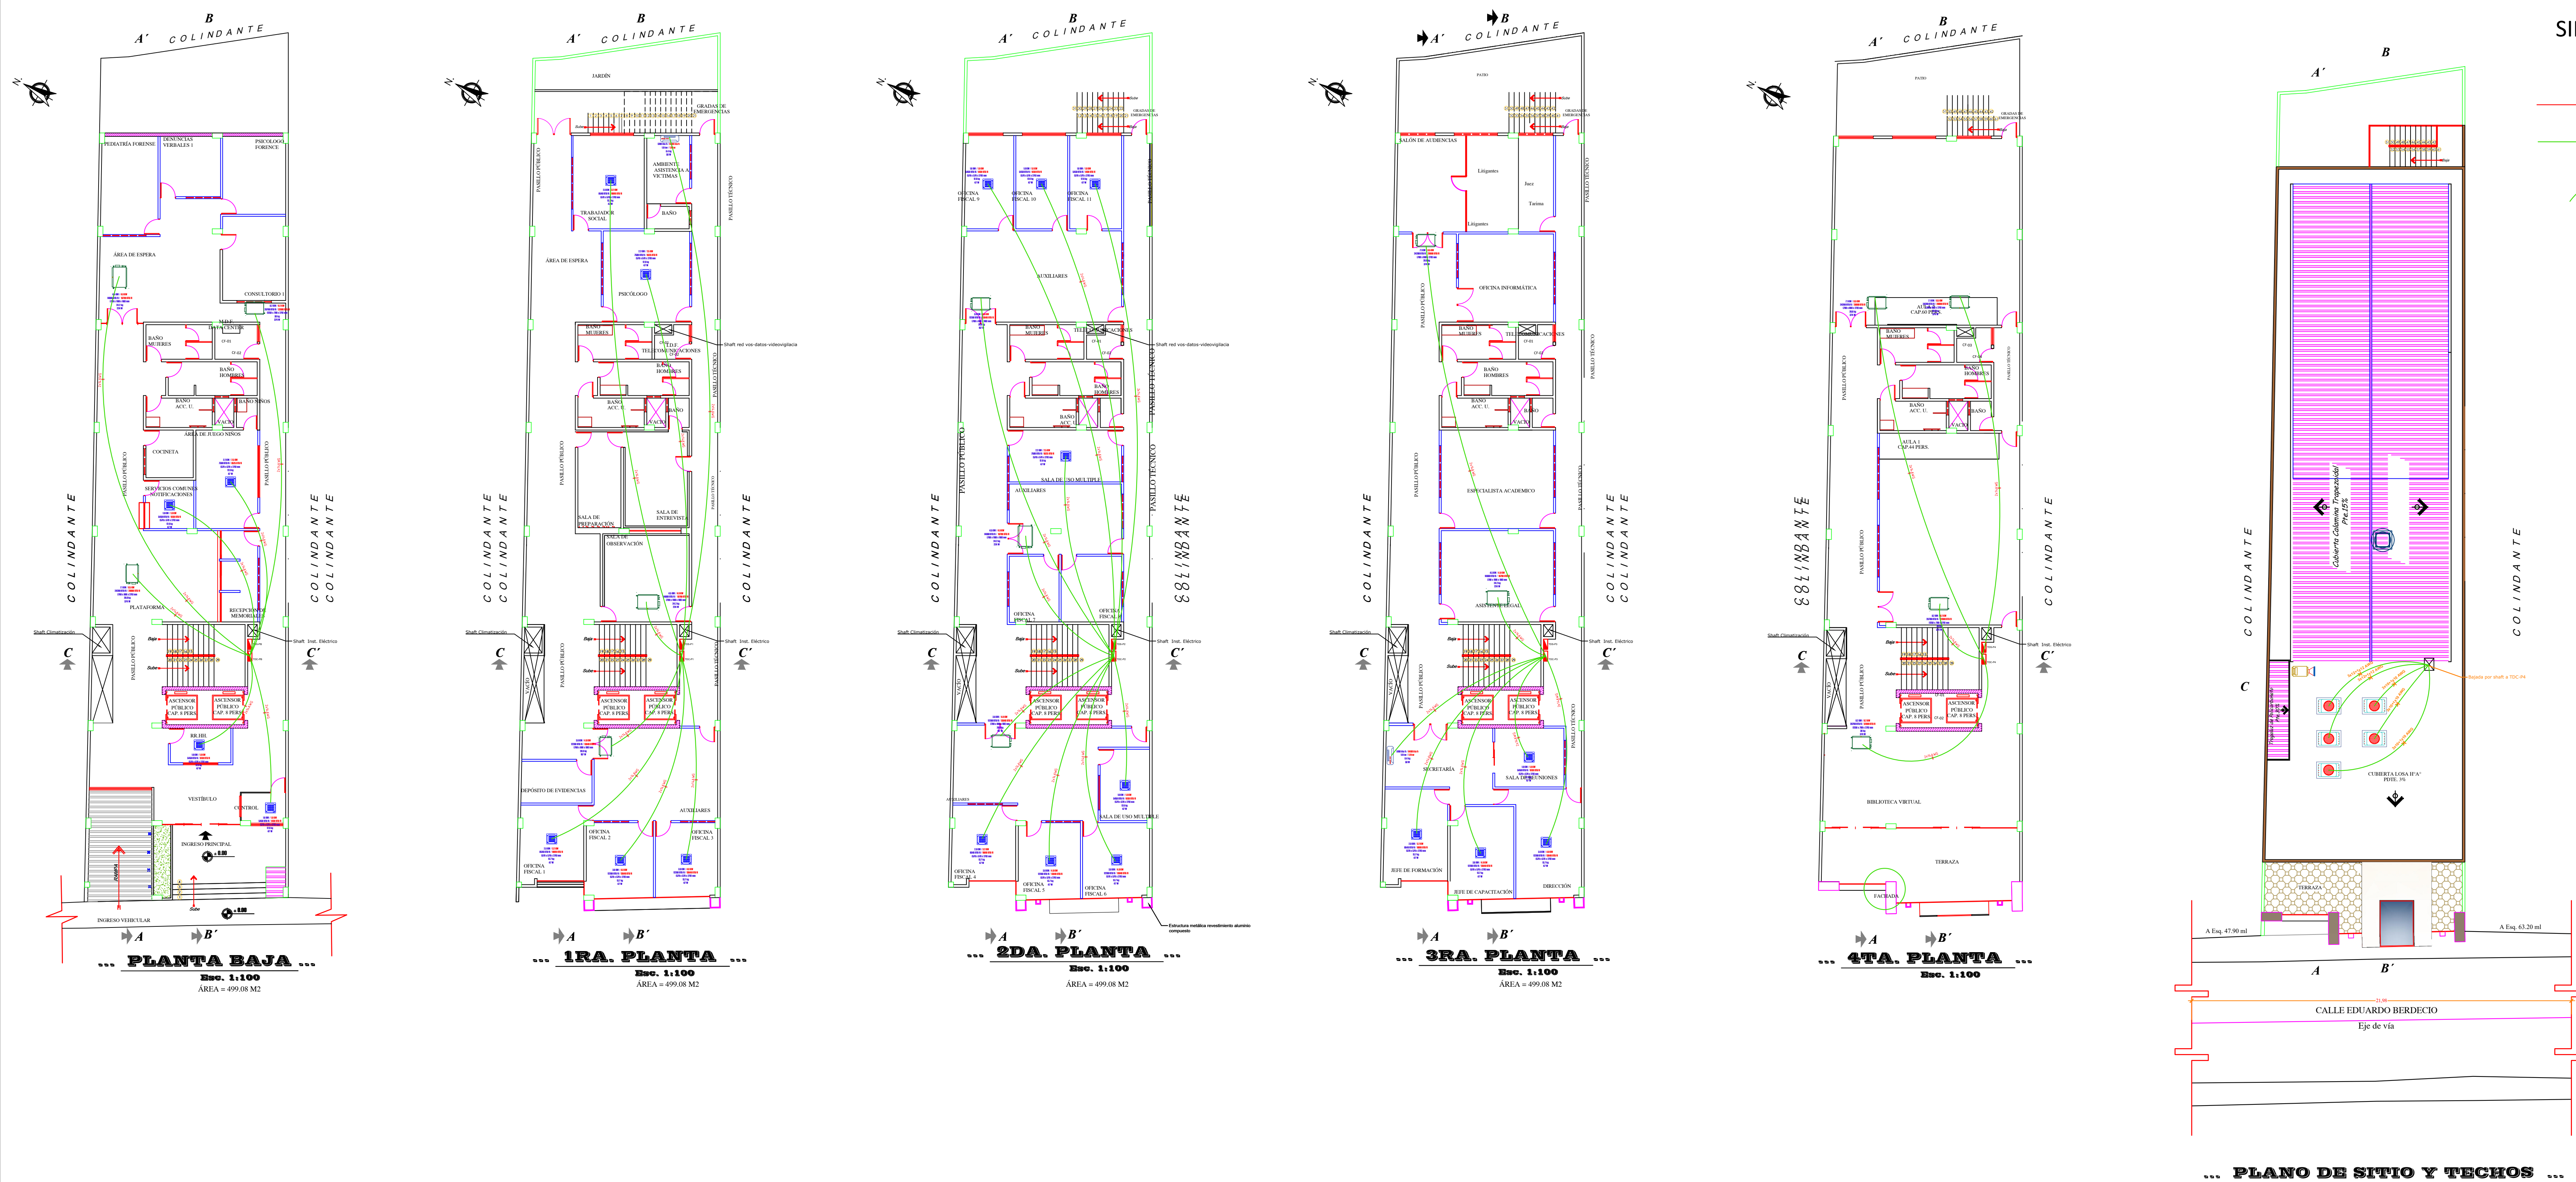

NOTAS:	
REFERENCIAS	
PLANOS:	
INSTALACION ELECTRICA	
PROYECTO:	
DISEÑO ELECTRICO FISCALIA	
PROPIETARIO:	
FISCALIA	
PROYECTISTA:	
ING. JORGE FERNANDO POVEDA RUIZ	
DIRECCION :	
EDUARDO BERDECIO	
CODIGO CATASTRAL:	
DISTRITO: 001	
MANZANA: 0002	
LOTE: 0016	
SUP. TOTAL CONST:	
2895.77 M2	
FECHA: 05/09/2023	
ESCALA INDICADAS:	
LÁMINA: 10 DE 16	
SELLOS DE APROBACIÓN G.A.M.S.:	
SELLOS ENTE COLEGADO:	

PLANO DE UBICACION :

Escala: 1: 5000

DUCTEADO DE TOMA PARA CLIMATIZACION




NOTAS:		
REFERENCIAS		
PLANOS:		
INSTALACION ELECTRICA		
PROYECTO:		
DISEÑO ELECTRICIO FISCALIA		
PROPIETARIO:		
FISCALIA		
PROYECTISTA:		
ING. JORGE FERNANDO POVEDA RUIZ		
DIRECCION :		
EDUARDO BERDECIO		
CODIGO CATASTRAL	DISTRITO	MANZANA
007	0002	0016
SUP. TOTAL CONST:		
2895.77 M ²		
FECHA: 05/09/2023		
ESCALA INDICADAS		
LÁMINA: 11 DE 16		
SELLOS DE APROBACIÓN G.A.M.S.:		
SELLOS ENTE COLEGADO:		

PLANO DE UBICACION :

Escala: 1: 5000


DISTRIBUCION DE TABLEROS

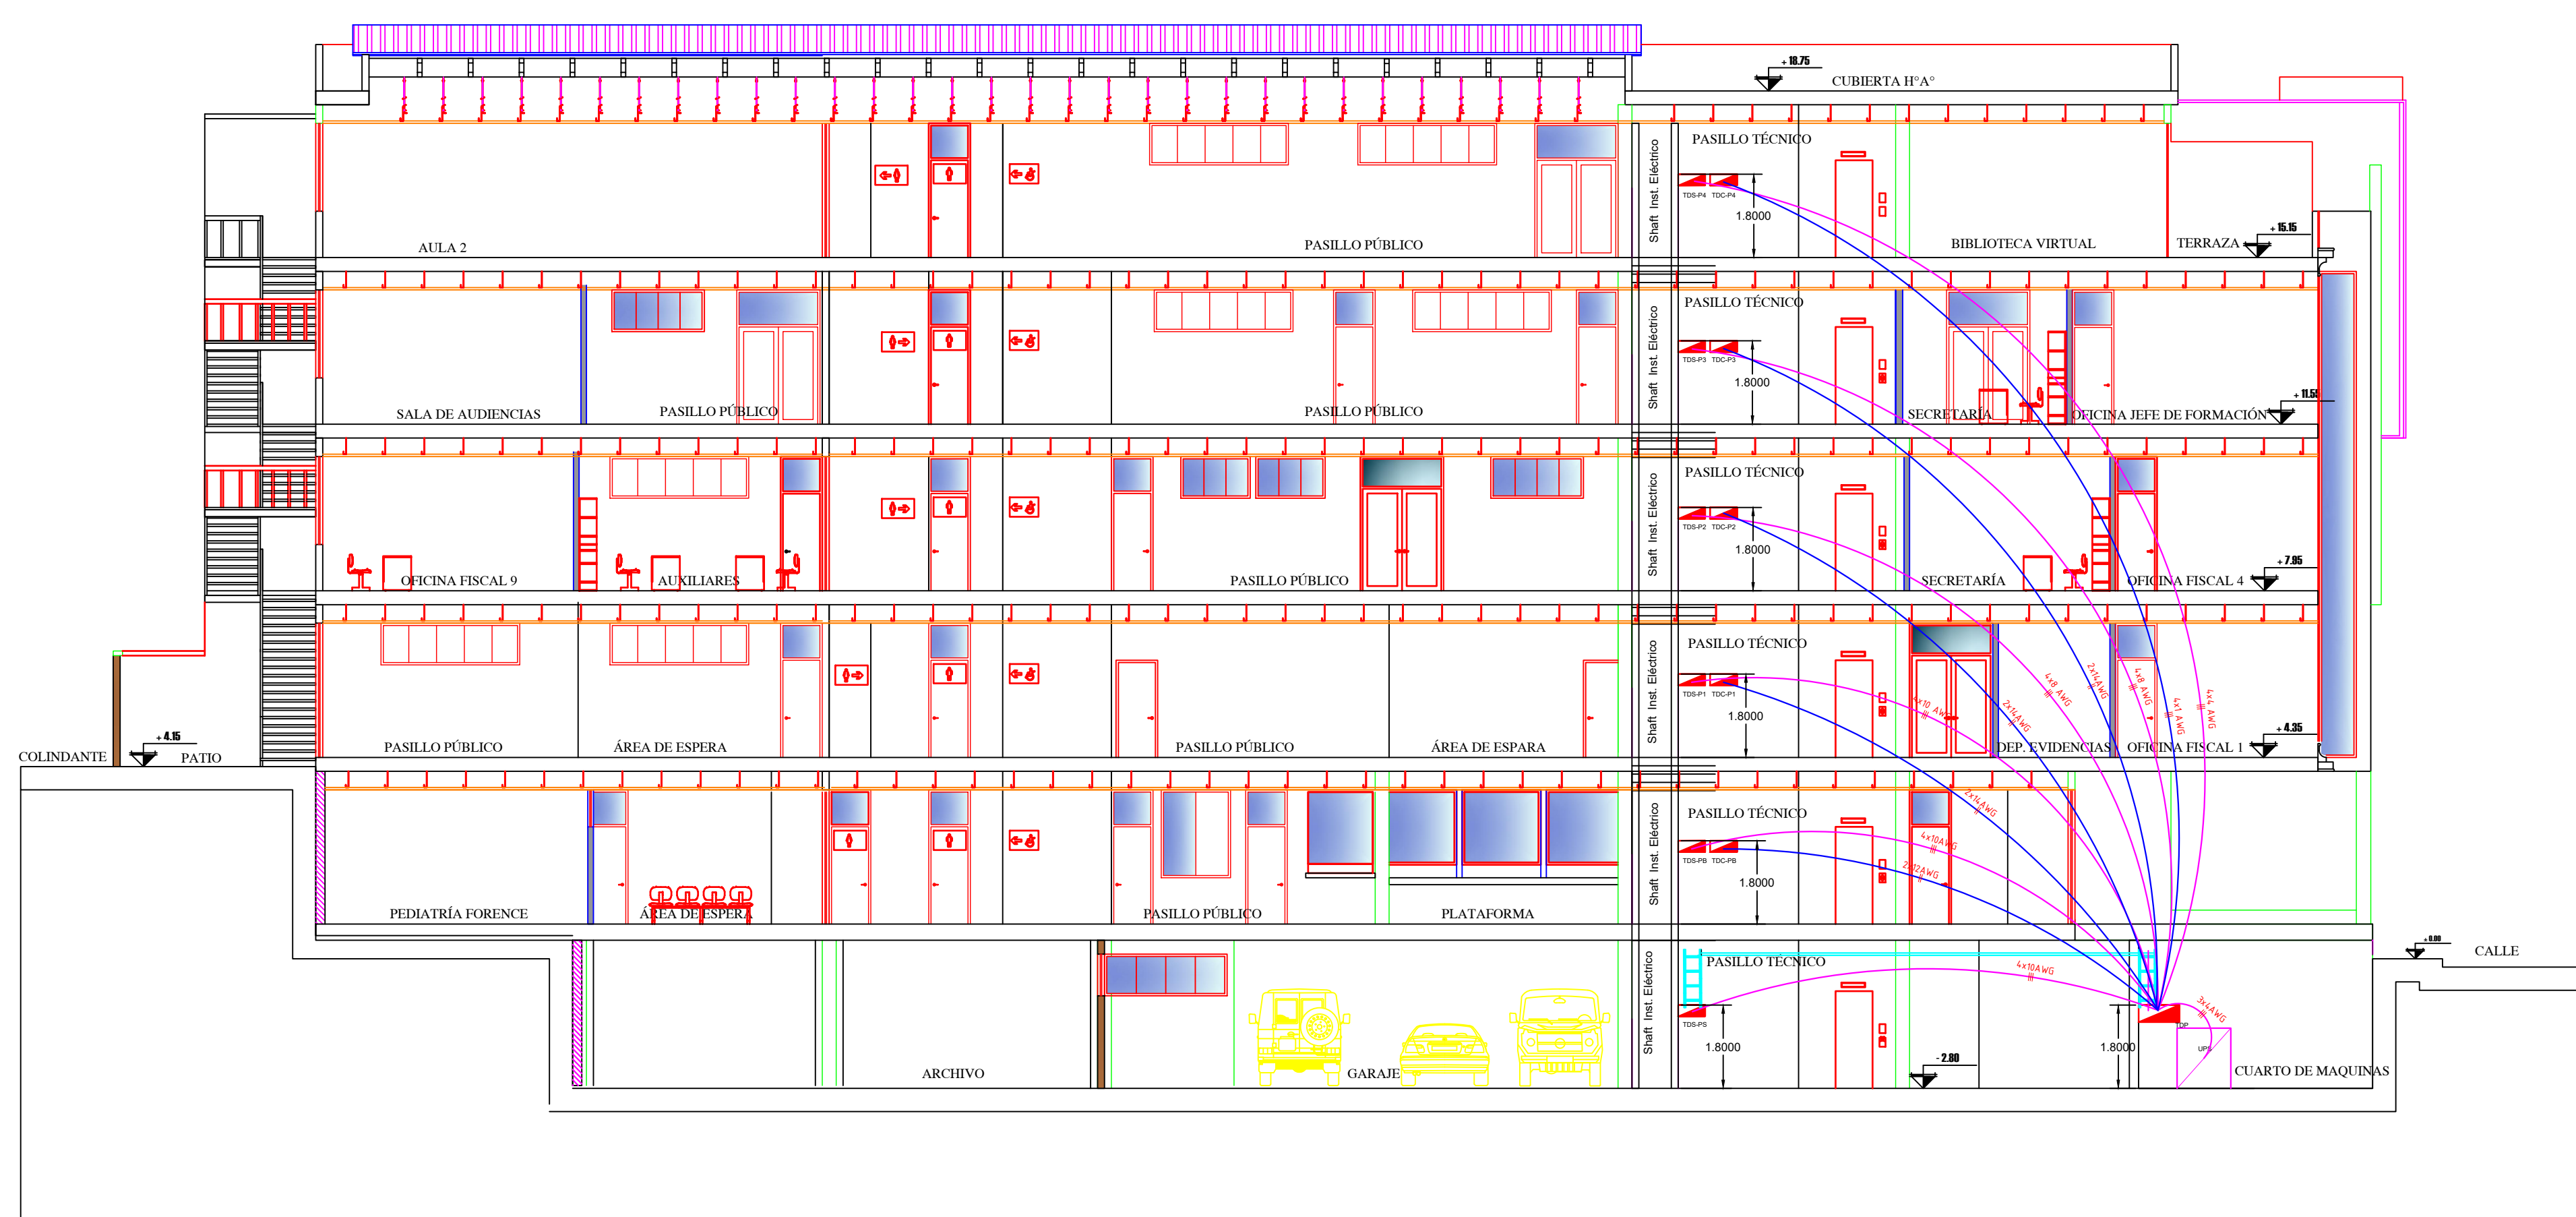

... CORTE A-A' ...
Esc. 1:50



... CORTE A-A' ...
Esc. 1:50

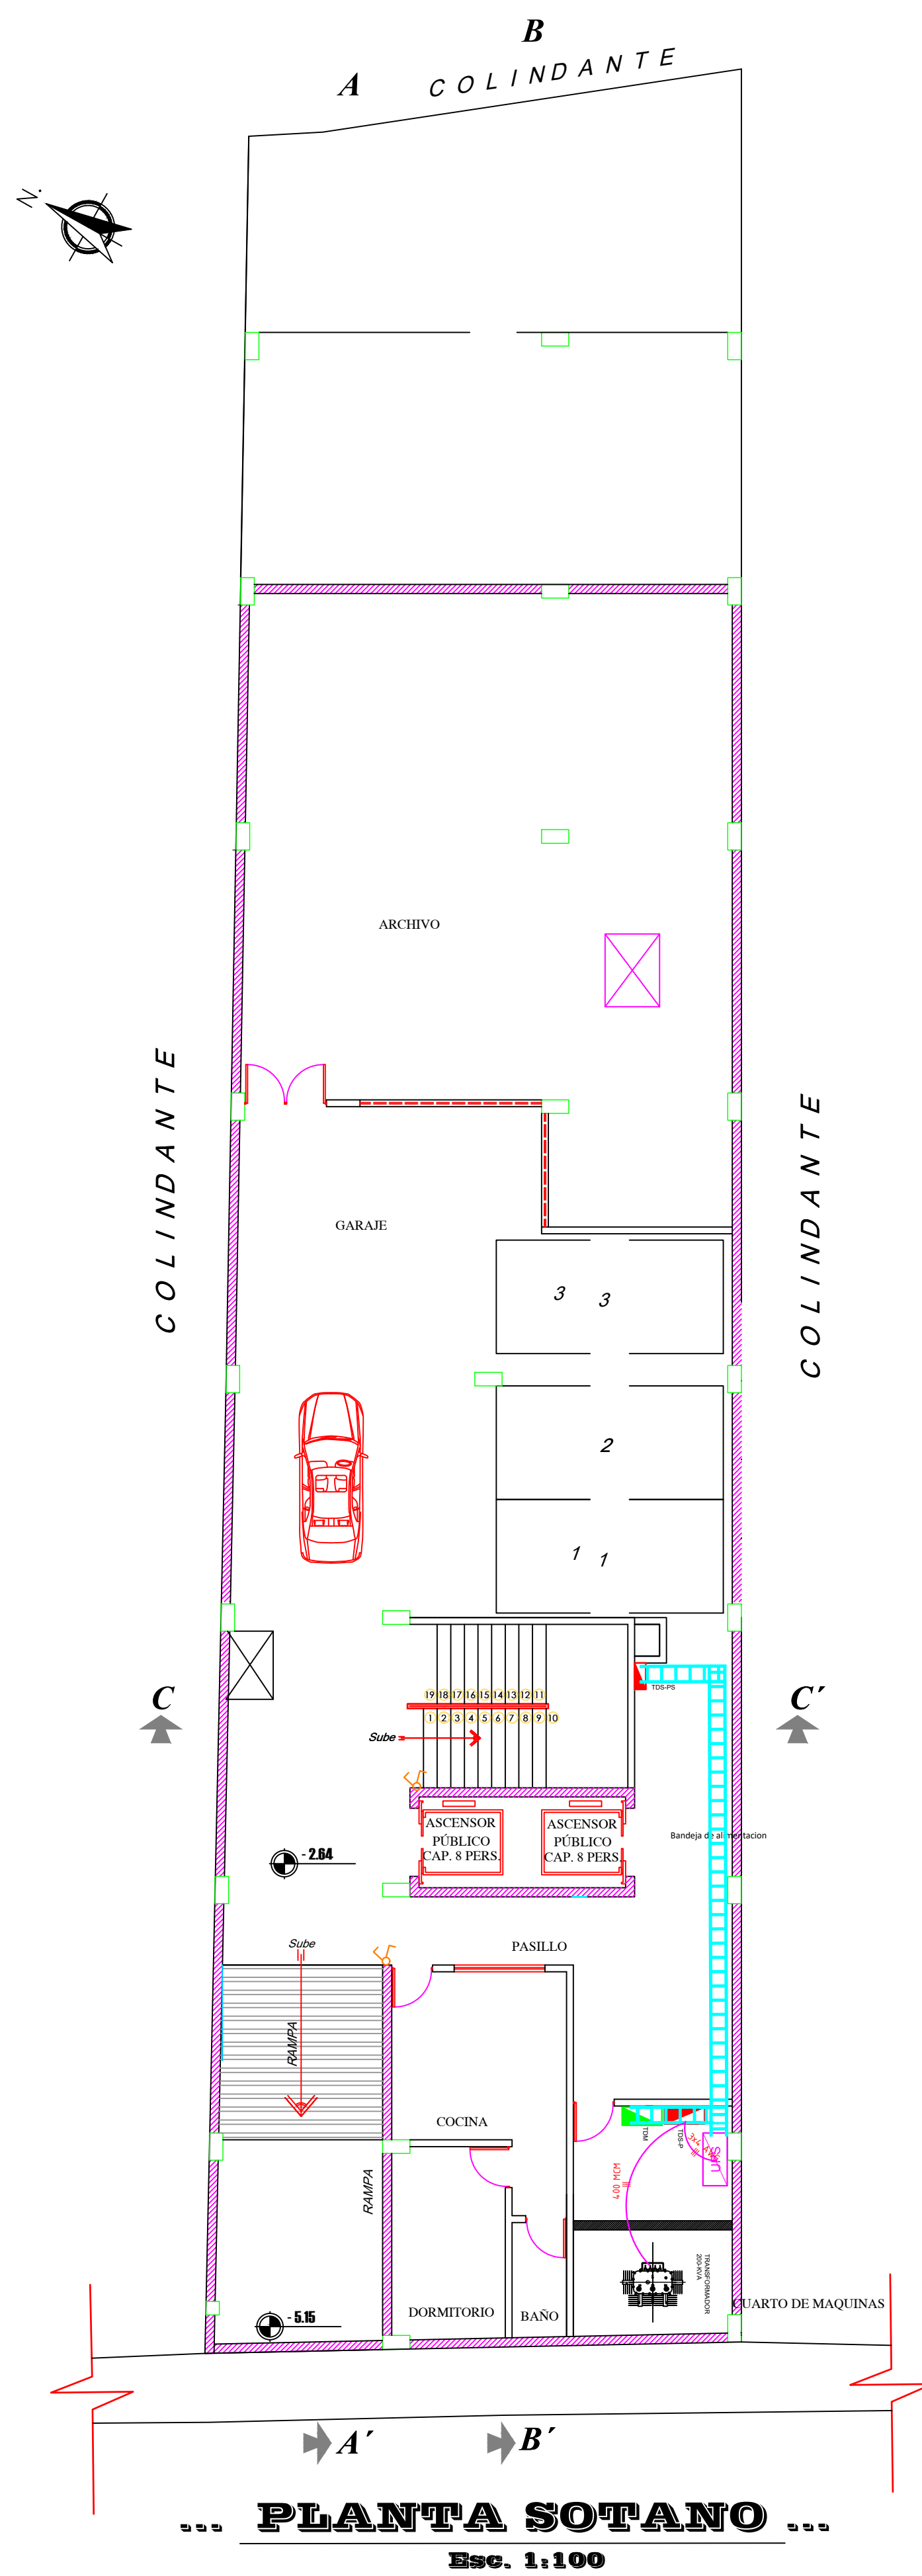

... PLANTA SOTANO ...
Esc. 1:100

SIMBOLOGÍA	DESCRIPCION
	Tablero de medicion
	Tablero de distribucion principal
	Tablero de distribucion secundario-Plata sotano
	Tablero de distribucion secundario-Plata baja
	Tablero de distribucion secundario-Piso 1
	Tablero de distribucion secundario-Piso 2
	Tablero de distribucion secundario-Piso 3
	Tablero de distribucion secundario-Piso 4
	Tablero de distribucion climatizacion-Planta baja
	Tablero de distribucion climatizacion-Piso 1
	Tablero de distribucion climatizacion-Piso 2
	Tablero de distribucion climatizacion-Piso 3
	Tablero de distribucion climatizacion-Piso 4
	Circuitos de alimentacion a tableros secundarios
	Circuitos de alimetacion a tableros de climatizacion
	Bandeja de alimentacion

NOTAS:

REFERENCIAS

INSTALACION ELECTRICA

PROYECTO:
DISEÑO ELECTRICIO FISCALIA

PROPIETARIO:
FISCALIA

PROYECTISTA:
ING. JORGE FERNANDO POVEDA RUIZ

DIRECCION :
EDUARDO BERDECIO


CODIGO CATASTRAL: 001 0002 0016

SUP. TOTAL CONST: 2895.77 M2


FECHA: 05/09/2023

ESCALA INDICADAS: LÁMINA: 12 DE 16

SELLOS DE APROBACIÓN G.A.M.S.:

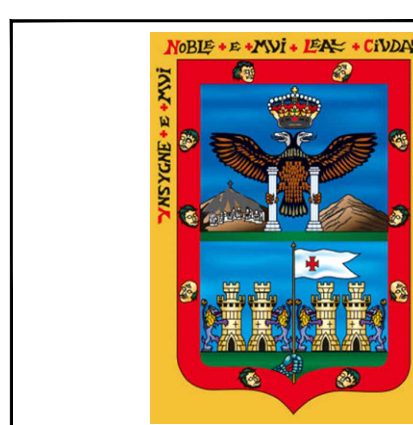


PLANO DE UBICACION :

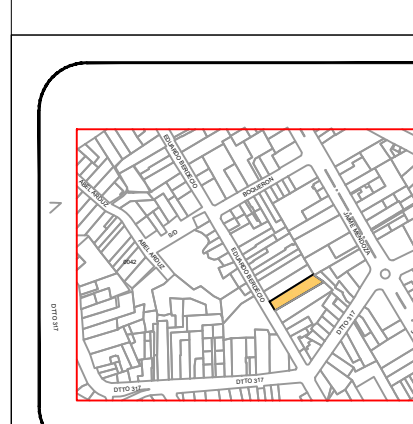


SELLOS ENTE COLEGADO:

ACOMETIDA SUBTERRANEA

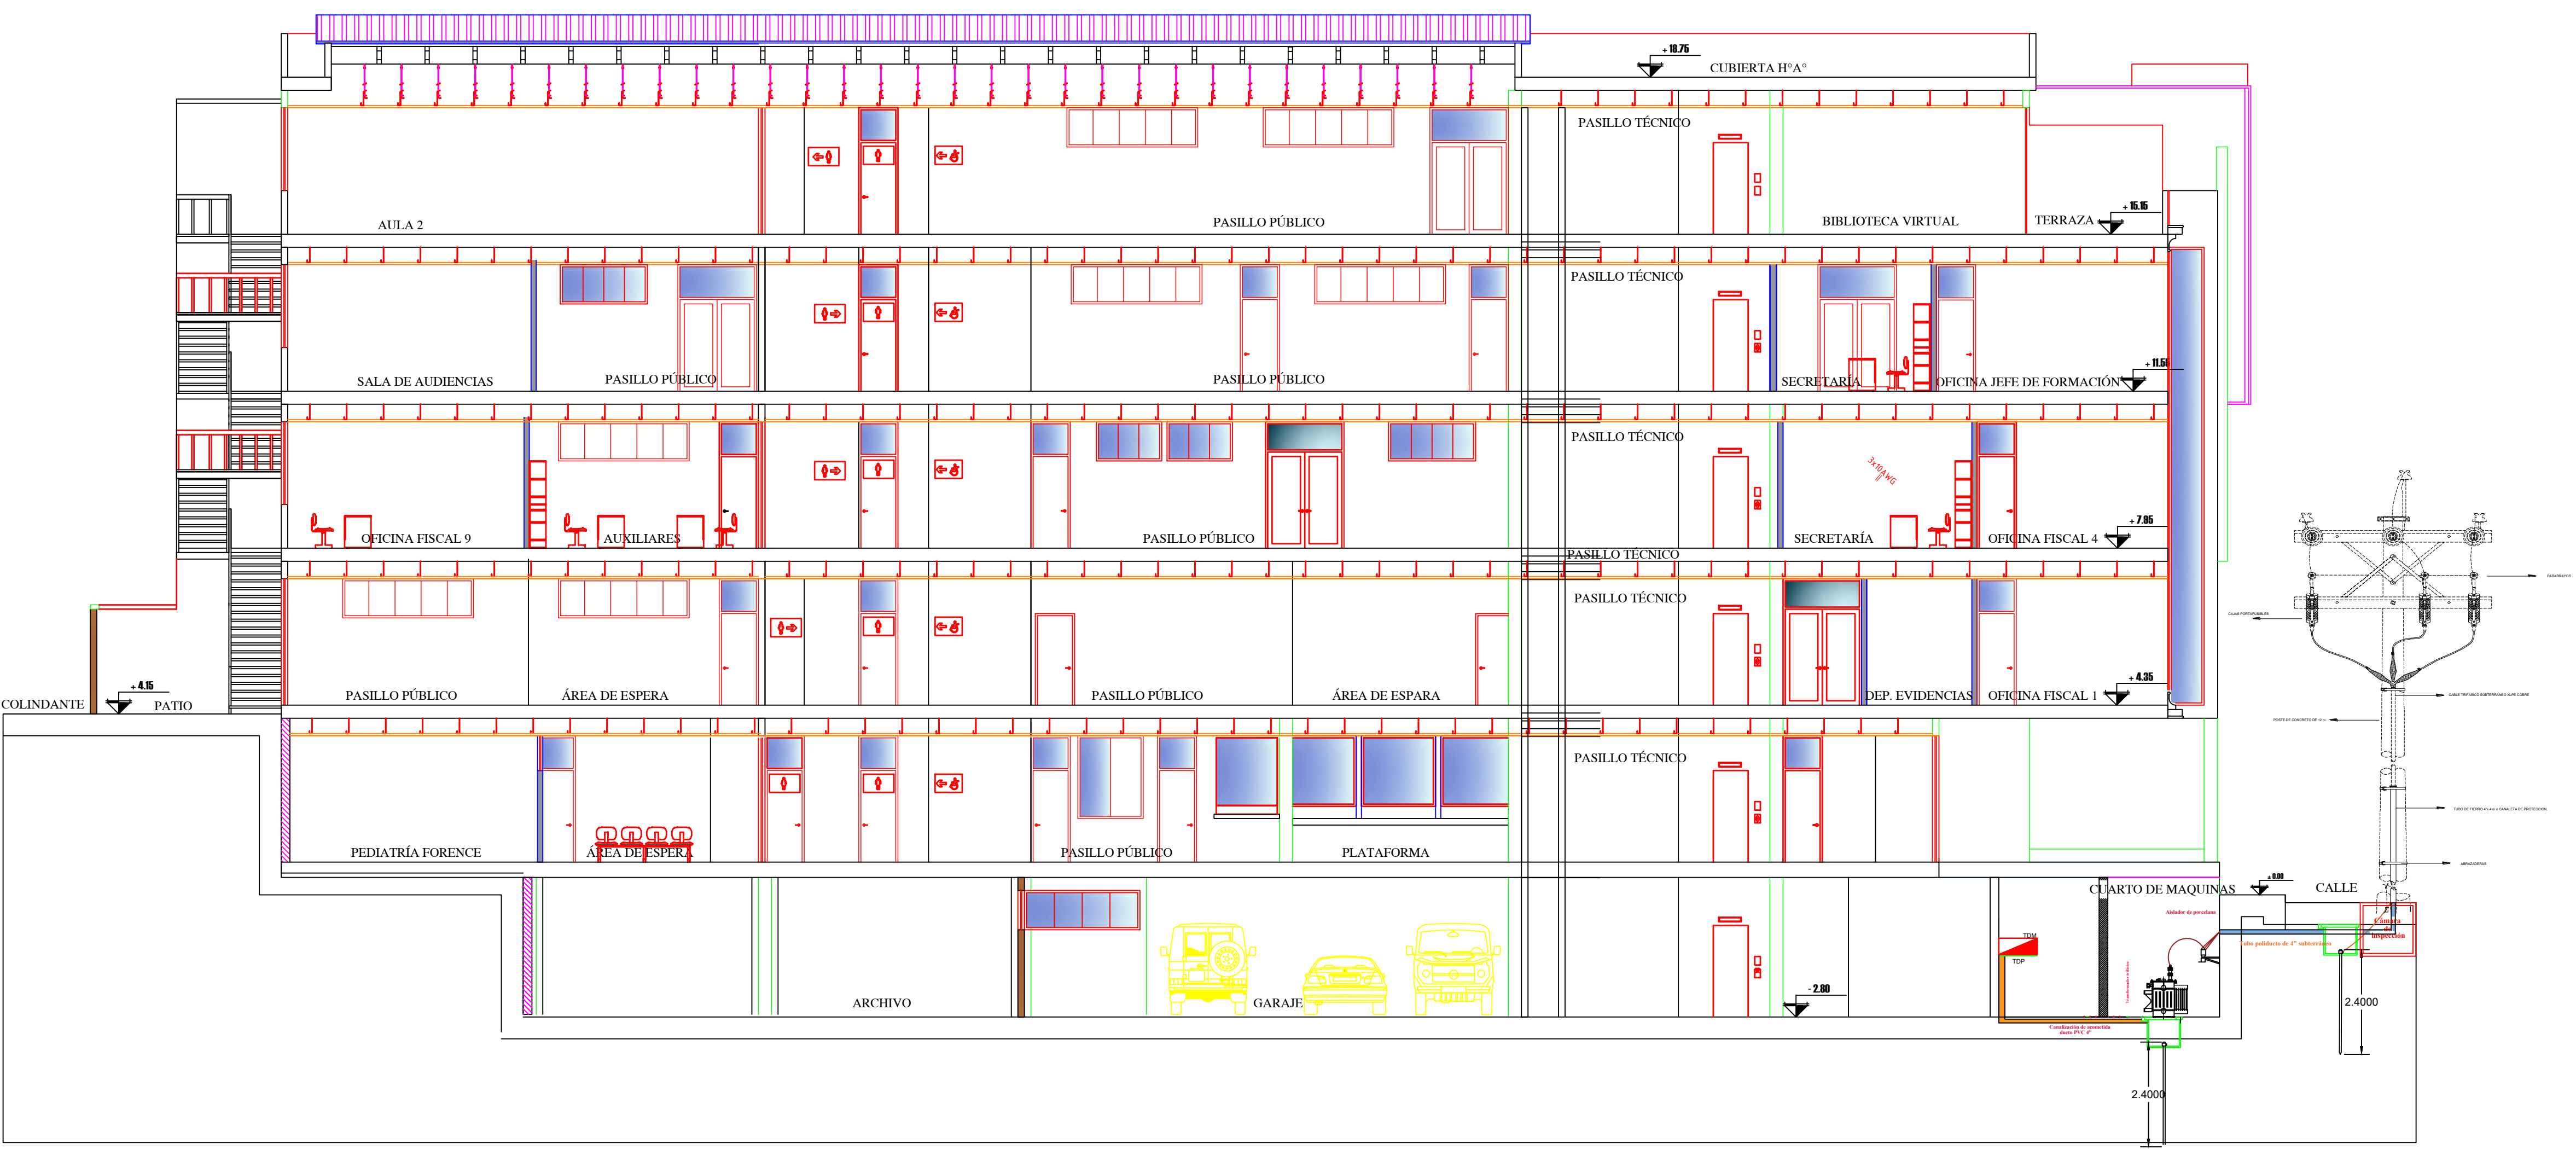

... CORTE A-A ...
Esc. 1:50

DETALLE CUARTO DE TRANSFORMACION

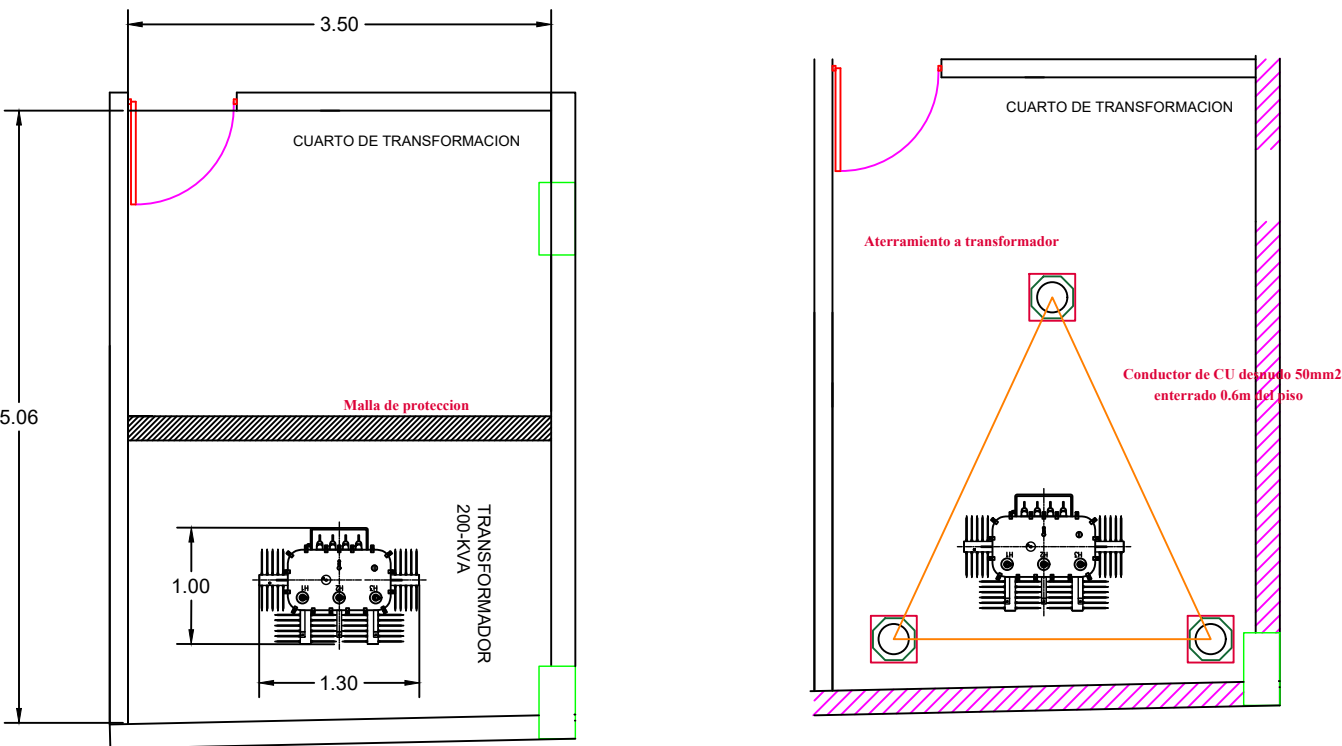

SIMBOLOGÍA	DESCRIPCIÓN
	Tablero de medicion
	Transformador trifasico 200 kva
	Jabalina 5/8" 2,4 m
	Camara de inspeccion 1.20 x 1.20 m
	Jabalina 5/8" 2,4 m
	Poste de media tension

NOTAS:

REFERENCIAS

PLANOS:
INSTALACION ELECTRICA

PROYECTO:
DISEÑO ELECTRICO FISCALIA

PROPIETARIO:
FISCALIA

PROYECTISTA:
ING. JORGE FERNANDO POVEDA RUIZ

DIRECCION :
EDUARDO BERDECIO

CODIGO CATASTRAL	DISTRITO	MANZANA	LOTE
007	0002	0016	

SUP. TOTAL CONST: 2895.77 M2

FECHA: 05/09/2023


ESCALA INDICADAS: LÁMINA: 13 DE 16

SELLOS DE APROBACIÓN G.A.M.S.:

PLANO DE UBICACION :
Esc. 1: 5000


SELLOS ENTE COLEGADO:

SISTEMA DE PUESTA A TIERRA

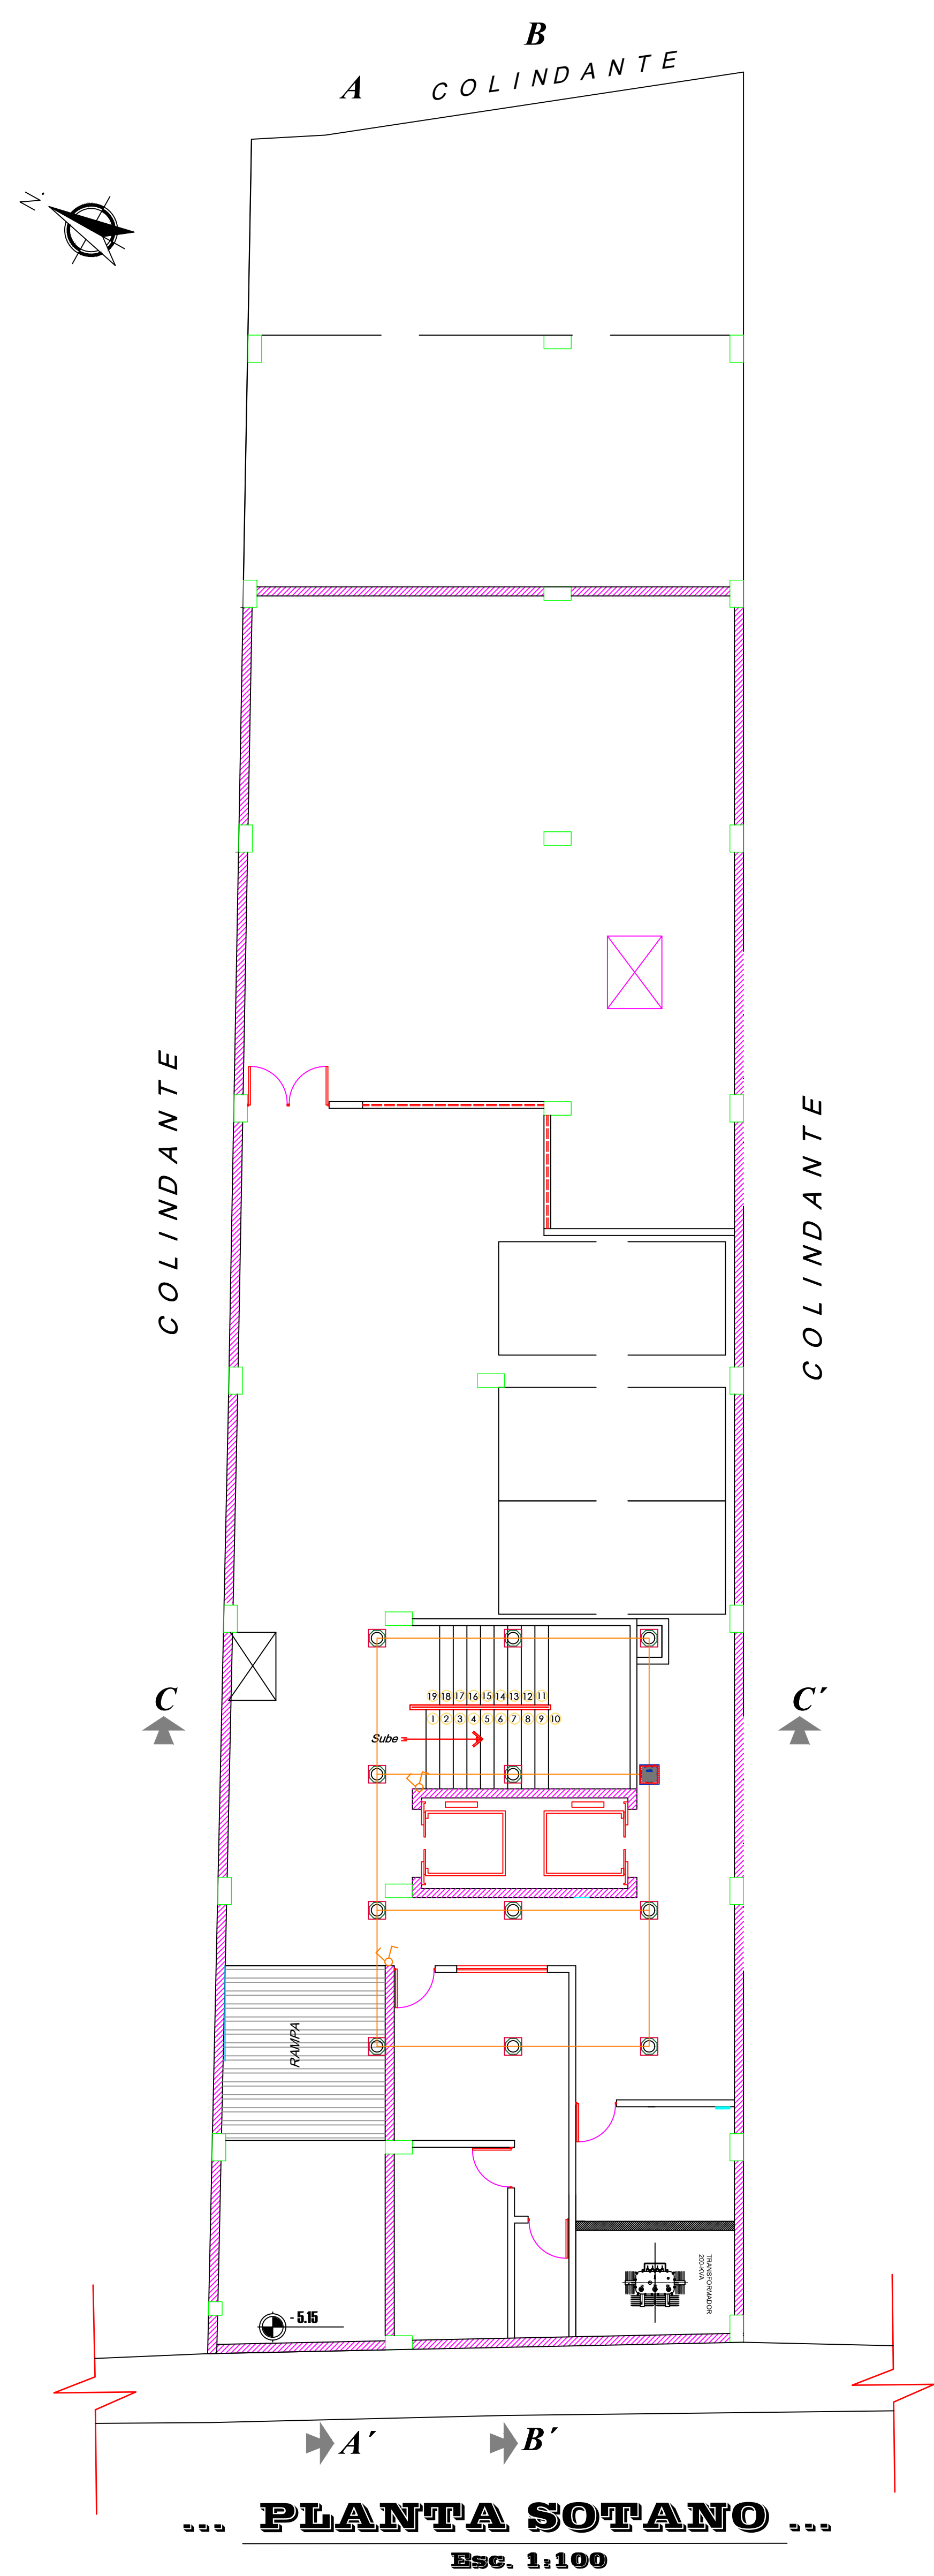

SIMBOLOGÍA	DESCRIPCIÓN
	Conductor CU desnudo 50 mm2 Enterrado a 0.6m
	Jabalina 5/8" 2,4 m

DETALLE CAMARA DE INSPECCION DE LA JABALINA

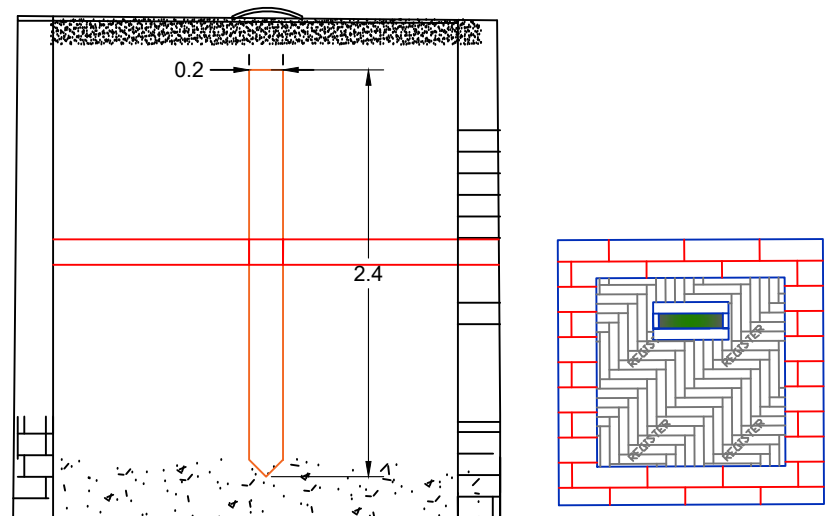

NOTAS:

REFERENCIAS

PLANOS:

INSTALACION ELECTRICA

PROYECTO:

DISEÑO ELECTRICO FISCALIA

PROPIETARIO:

FISCALIA

PROYECTISTA:

ING. JORGE FERNANDO POVEDA RUIZ

DIRECCION :

EDUARDO BERDECIO

CODIGO CATASTRAL

DISTRITO

007

MANZANA

0002

LOTE

0016

SUP. TOTAL CONST:

2895.77 M2

FECHA: 05/09/2023

ESCALA INDICADAS

LÁMINA: 14 DE 16



SELLOS DE APROBACIÓN G.A.M.S.:


PLANO DE UBICACION :

Esc. 1: 5000

SELLOS ENTE COLEGIADO:

SISTEMA DE PARARRAYOS

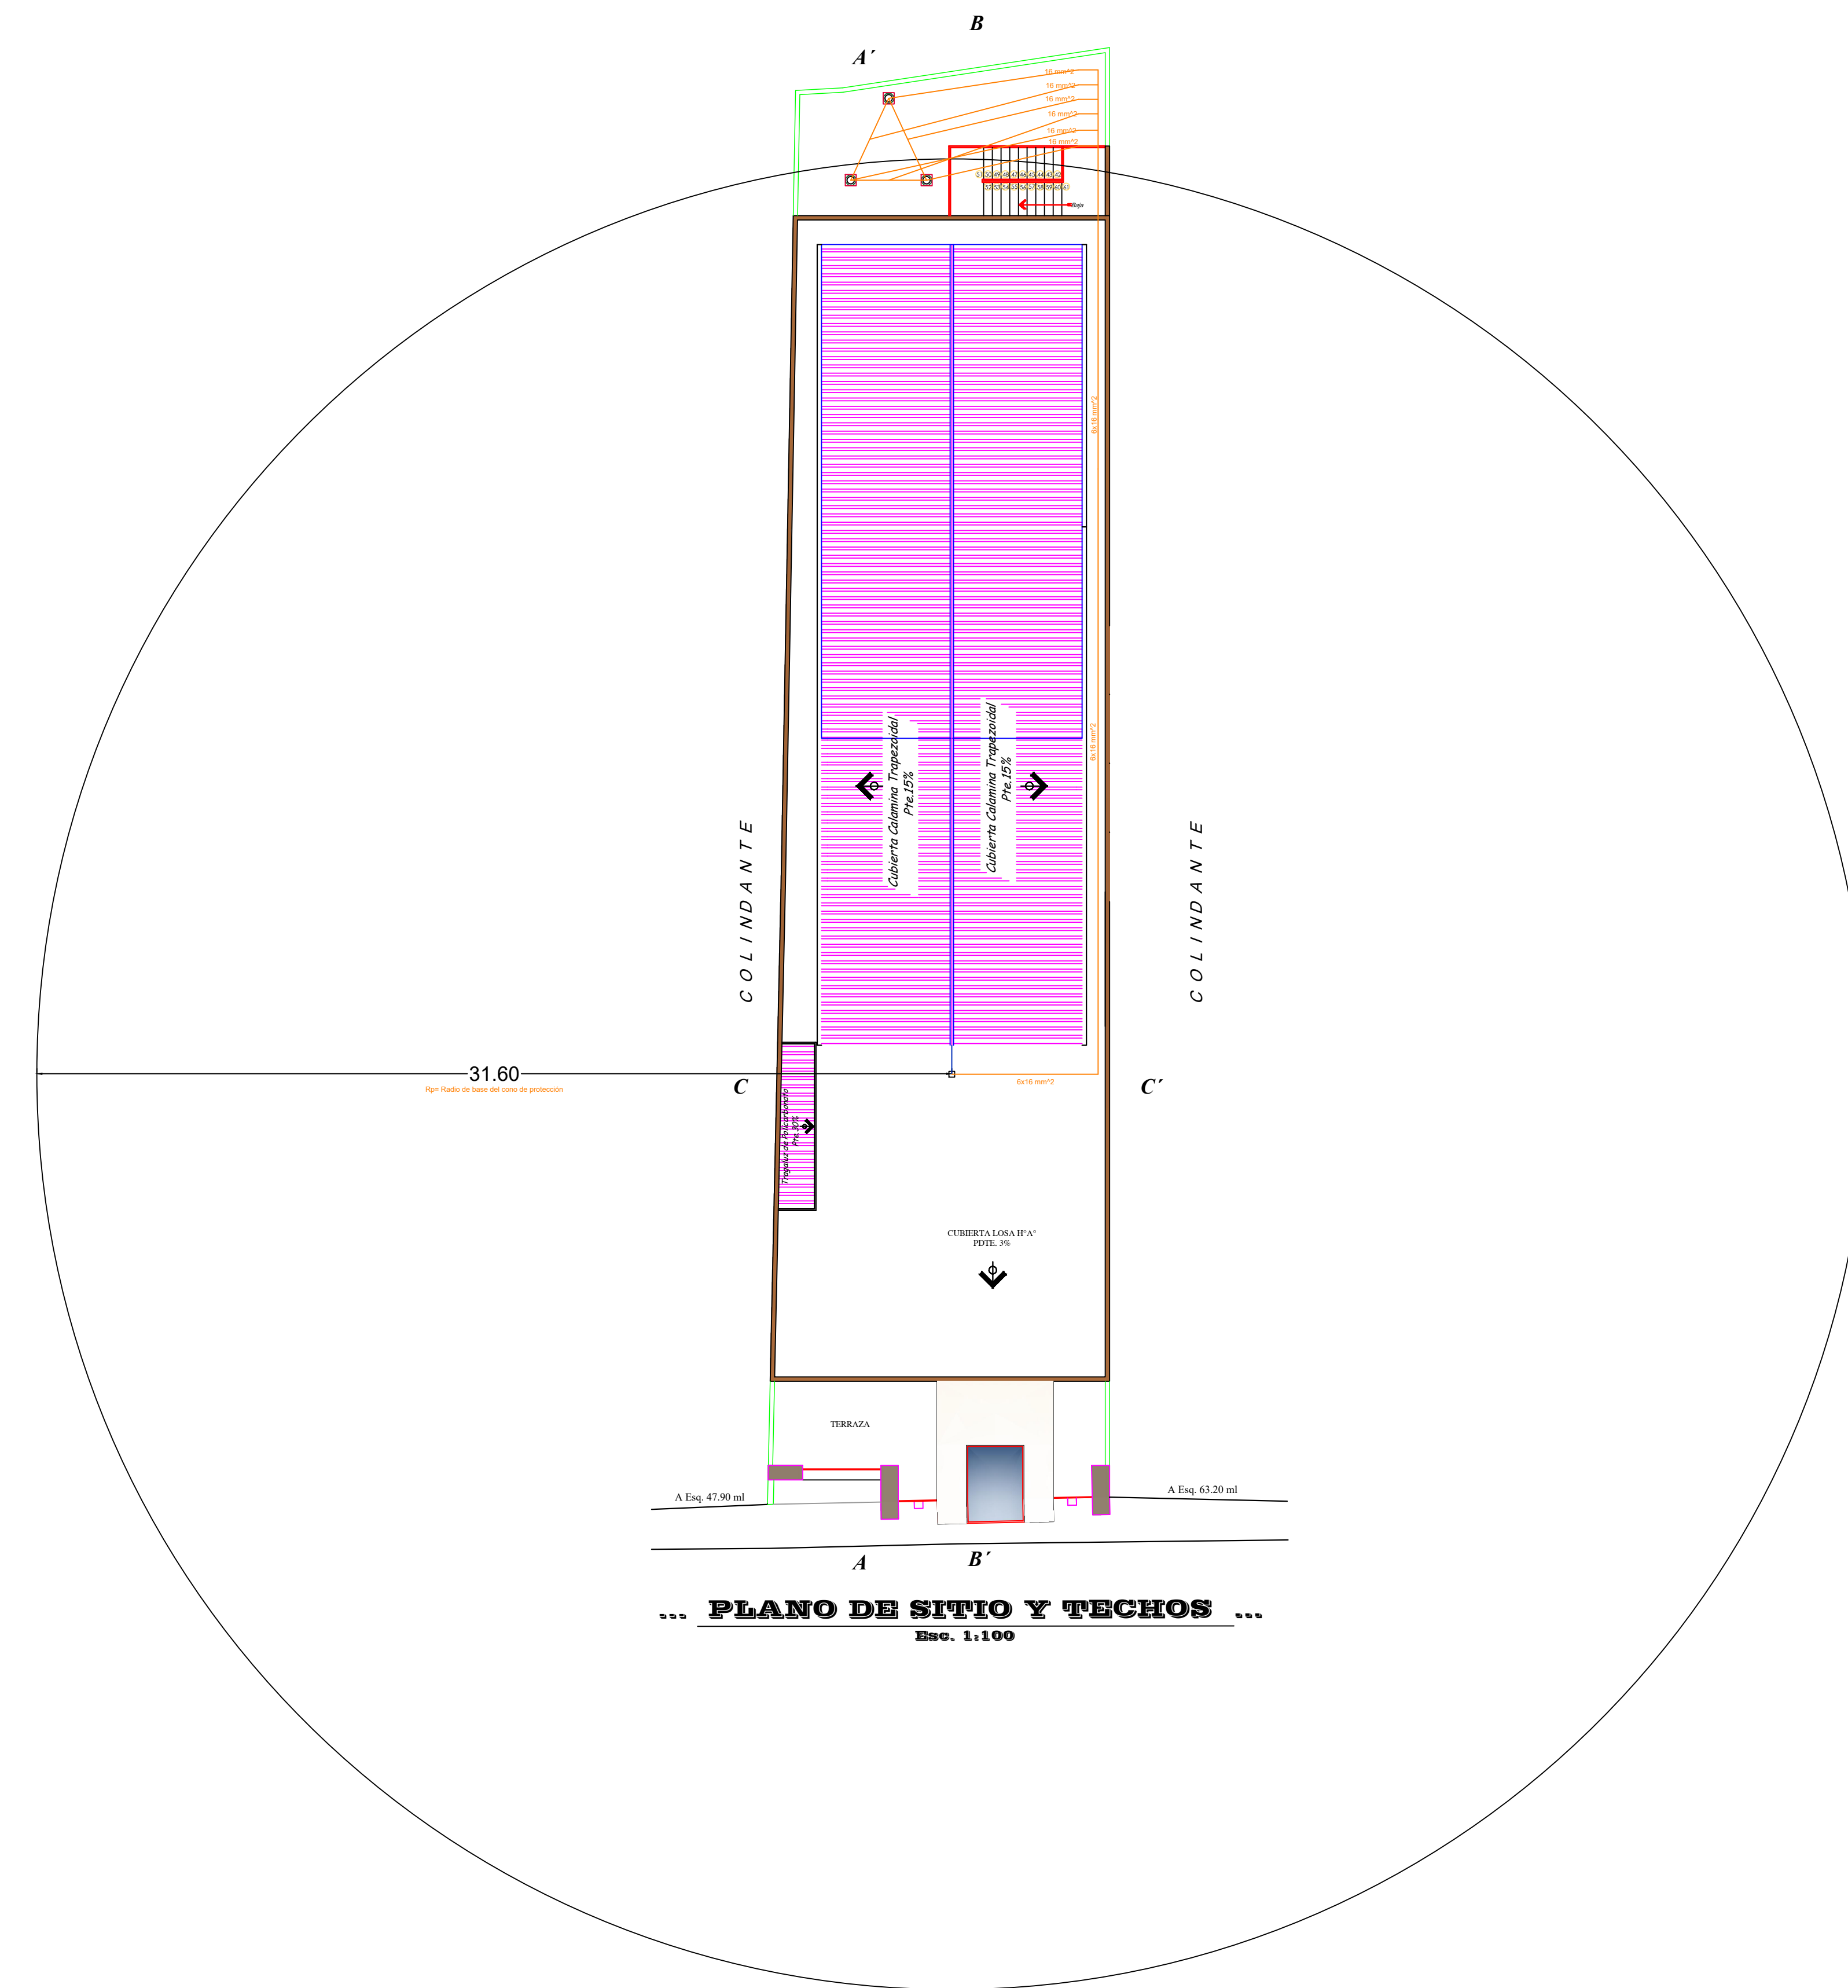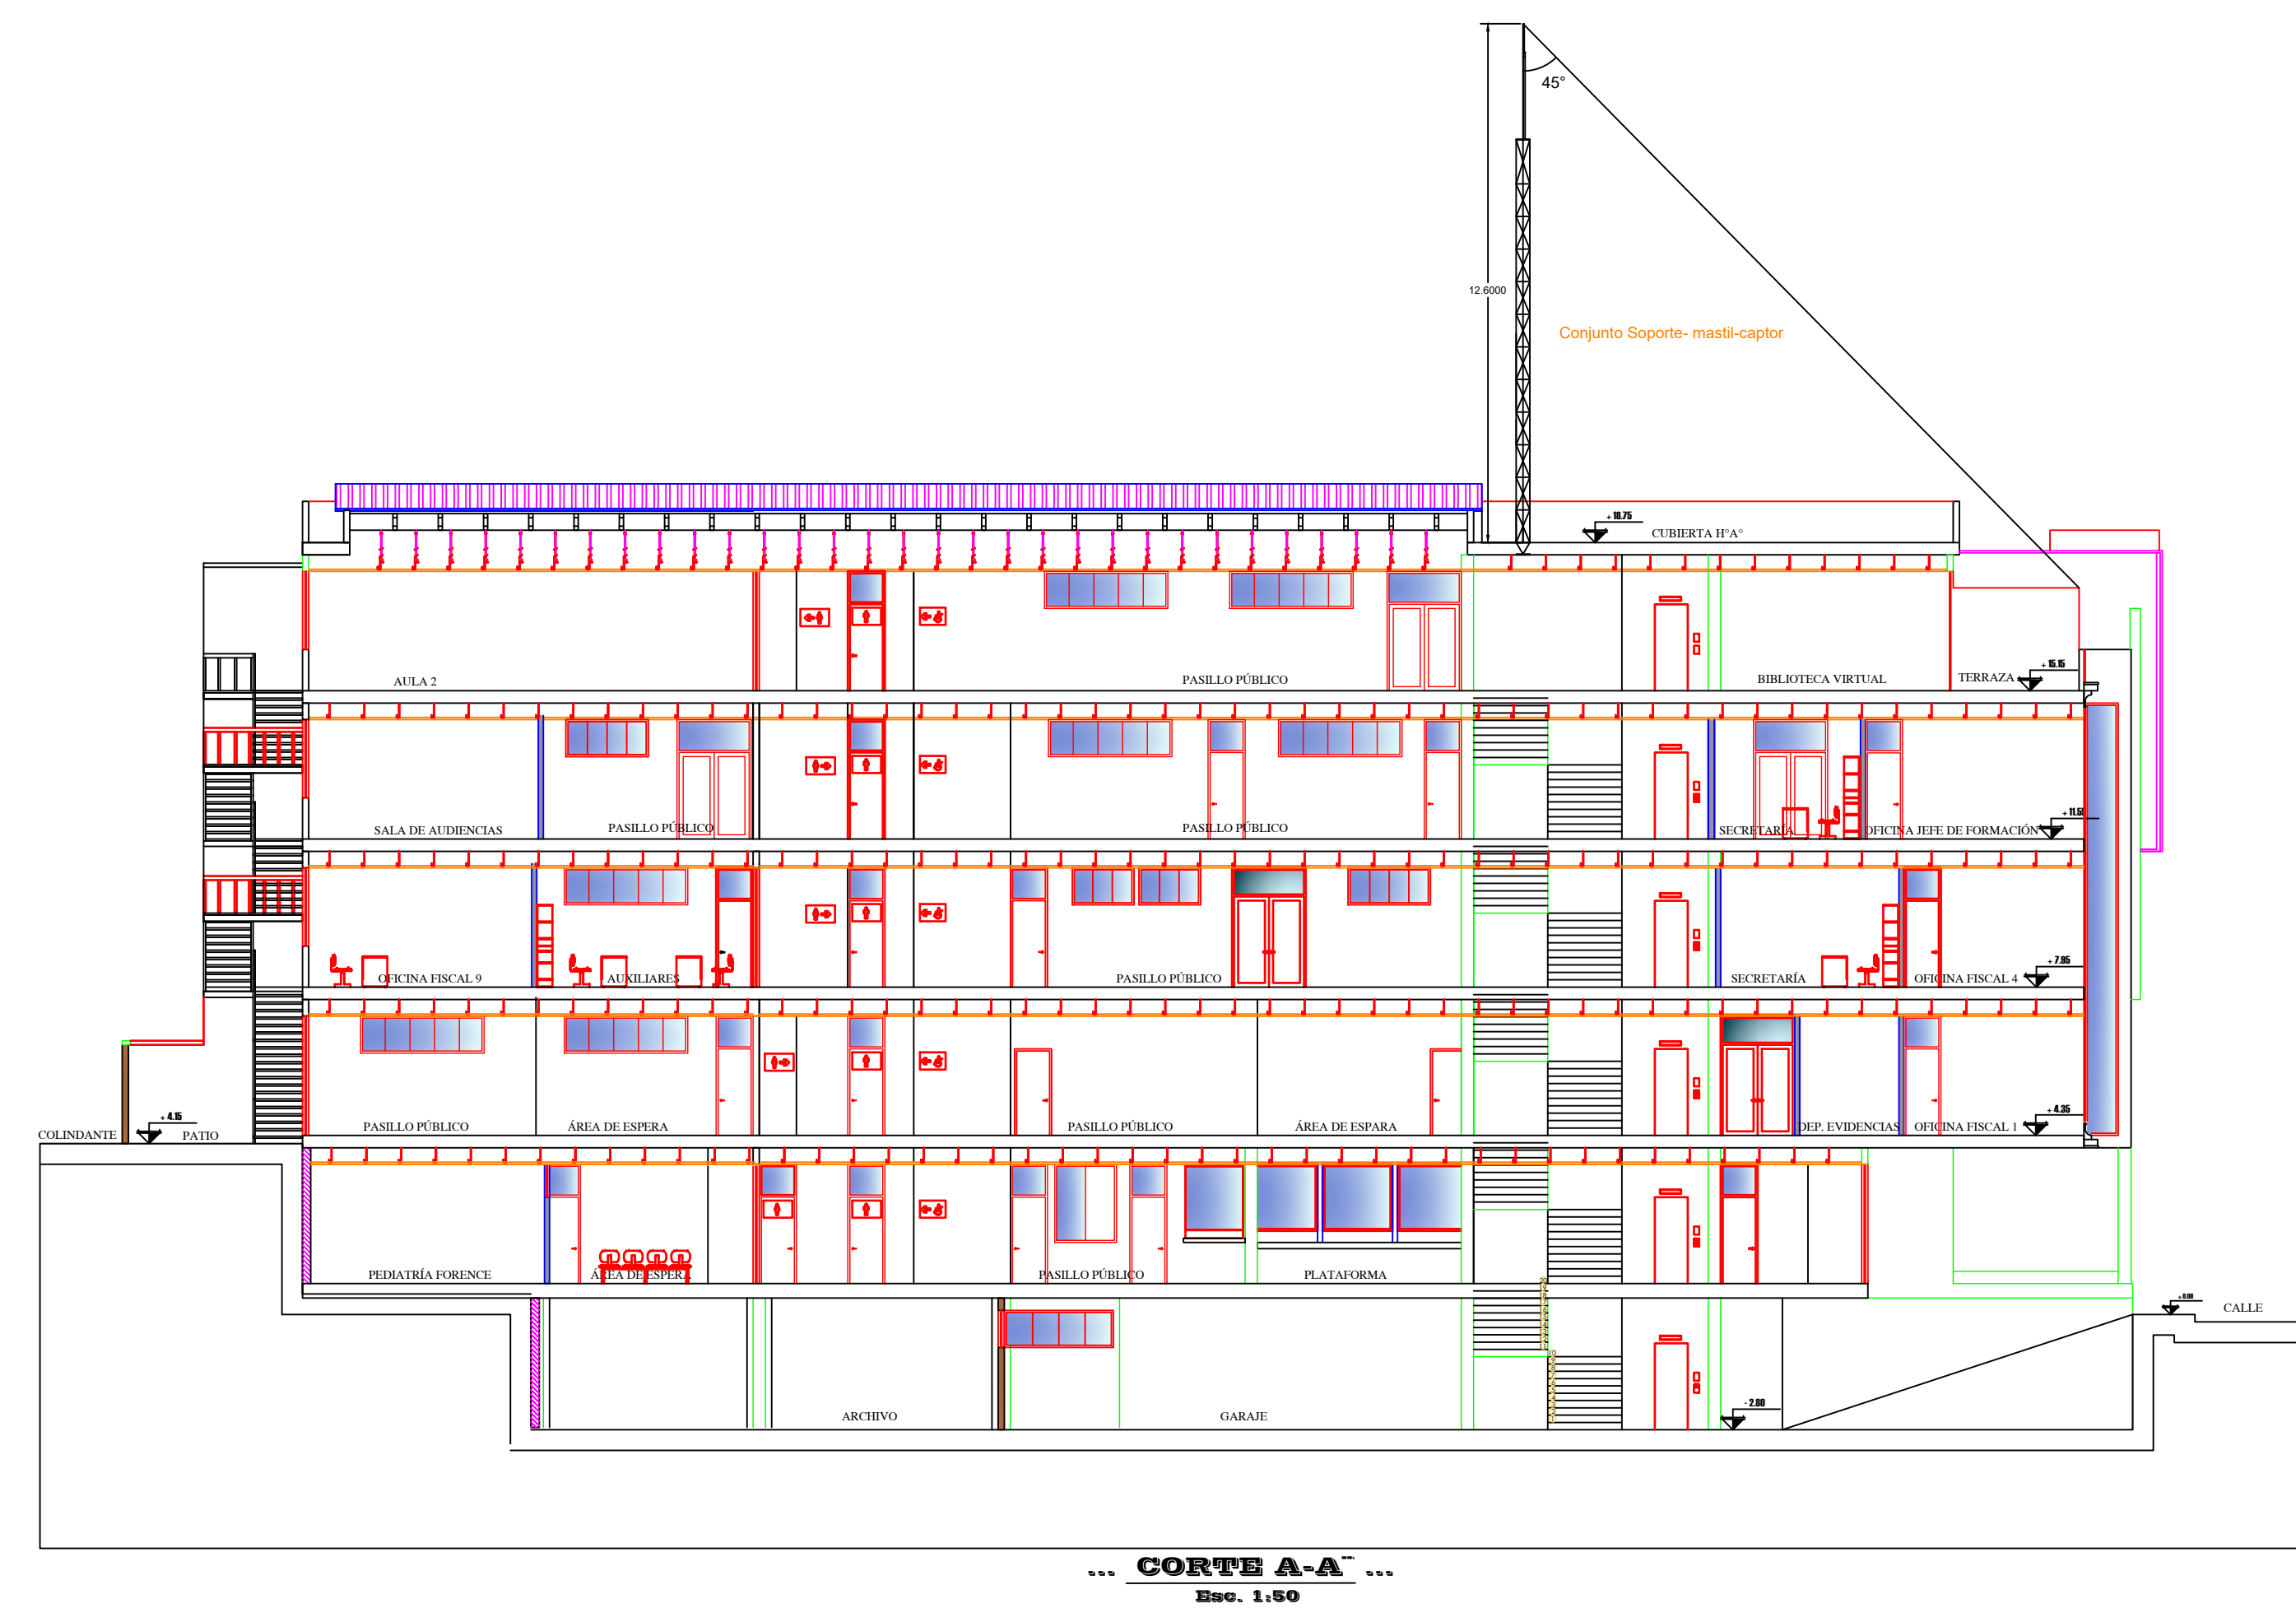

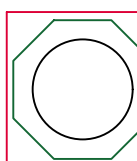SIMBOLOGÍA	DESCRIPCIÓN
	Soporte-Captor y Mastil
	Captor
	Conductores de descenso
	Jabalina 5/8" 2.4 m

NOTAS:		
REFERENCIAS		
PLANOS:		
INSTALACION ELECTRICA		
PROYECTO: DISEÑO ELECTRICO FISCALIA		
PROPIETARIO: FISCALIA		
PROYECTISTA: ING. JORGE FERNANDO POVEDA RUIZ		
DIRECCION : EDUARDO BERDECIO		
CODIGO CATASTRAL	DIRECCION 007	MANZANA 0002
SUP. TOTAL CONST.		2895.77 M2
FECHA :05/09/2023		
ESCALA INDICADAS		LÁMINA: 15 DE 16
SELLOS DE APROBACIÓN G.A.M.S.:		
PLANO DE UBICACION :		
Esc. 1: 5000		
		
SELLOS ENTE COLEGADO:		