


DIAGRAMA UNIFILAR

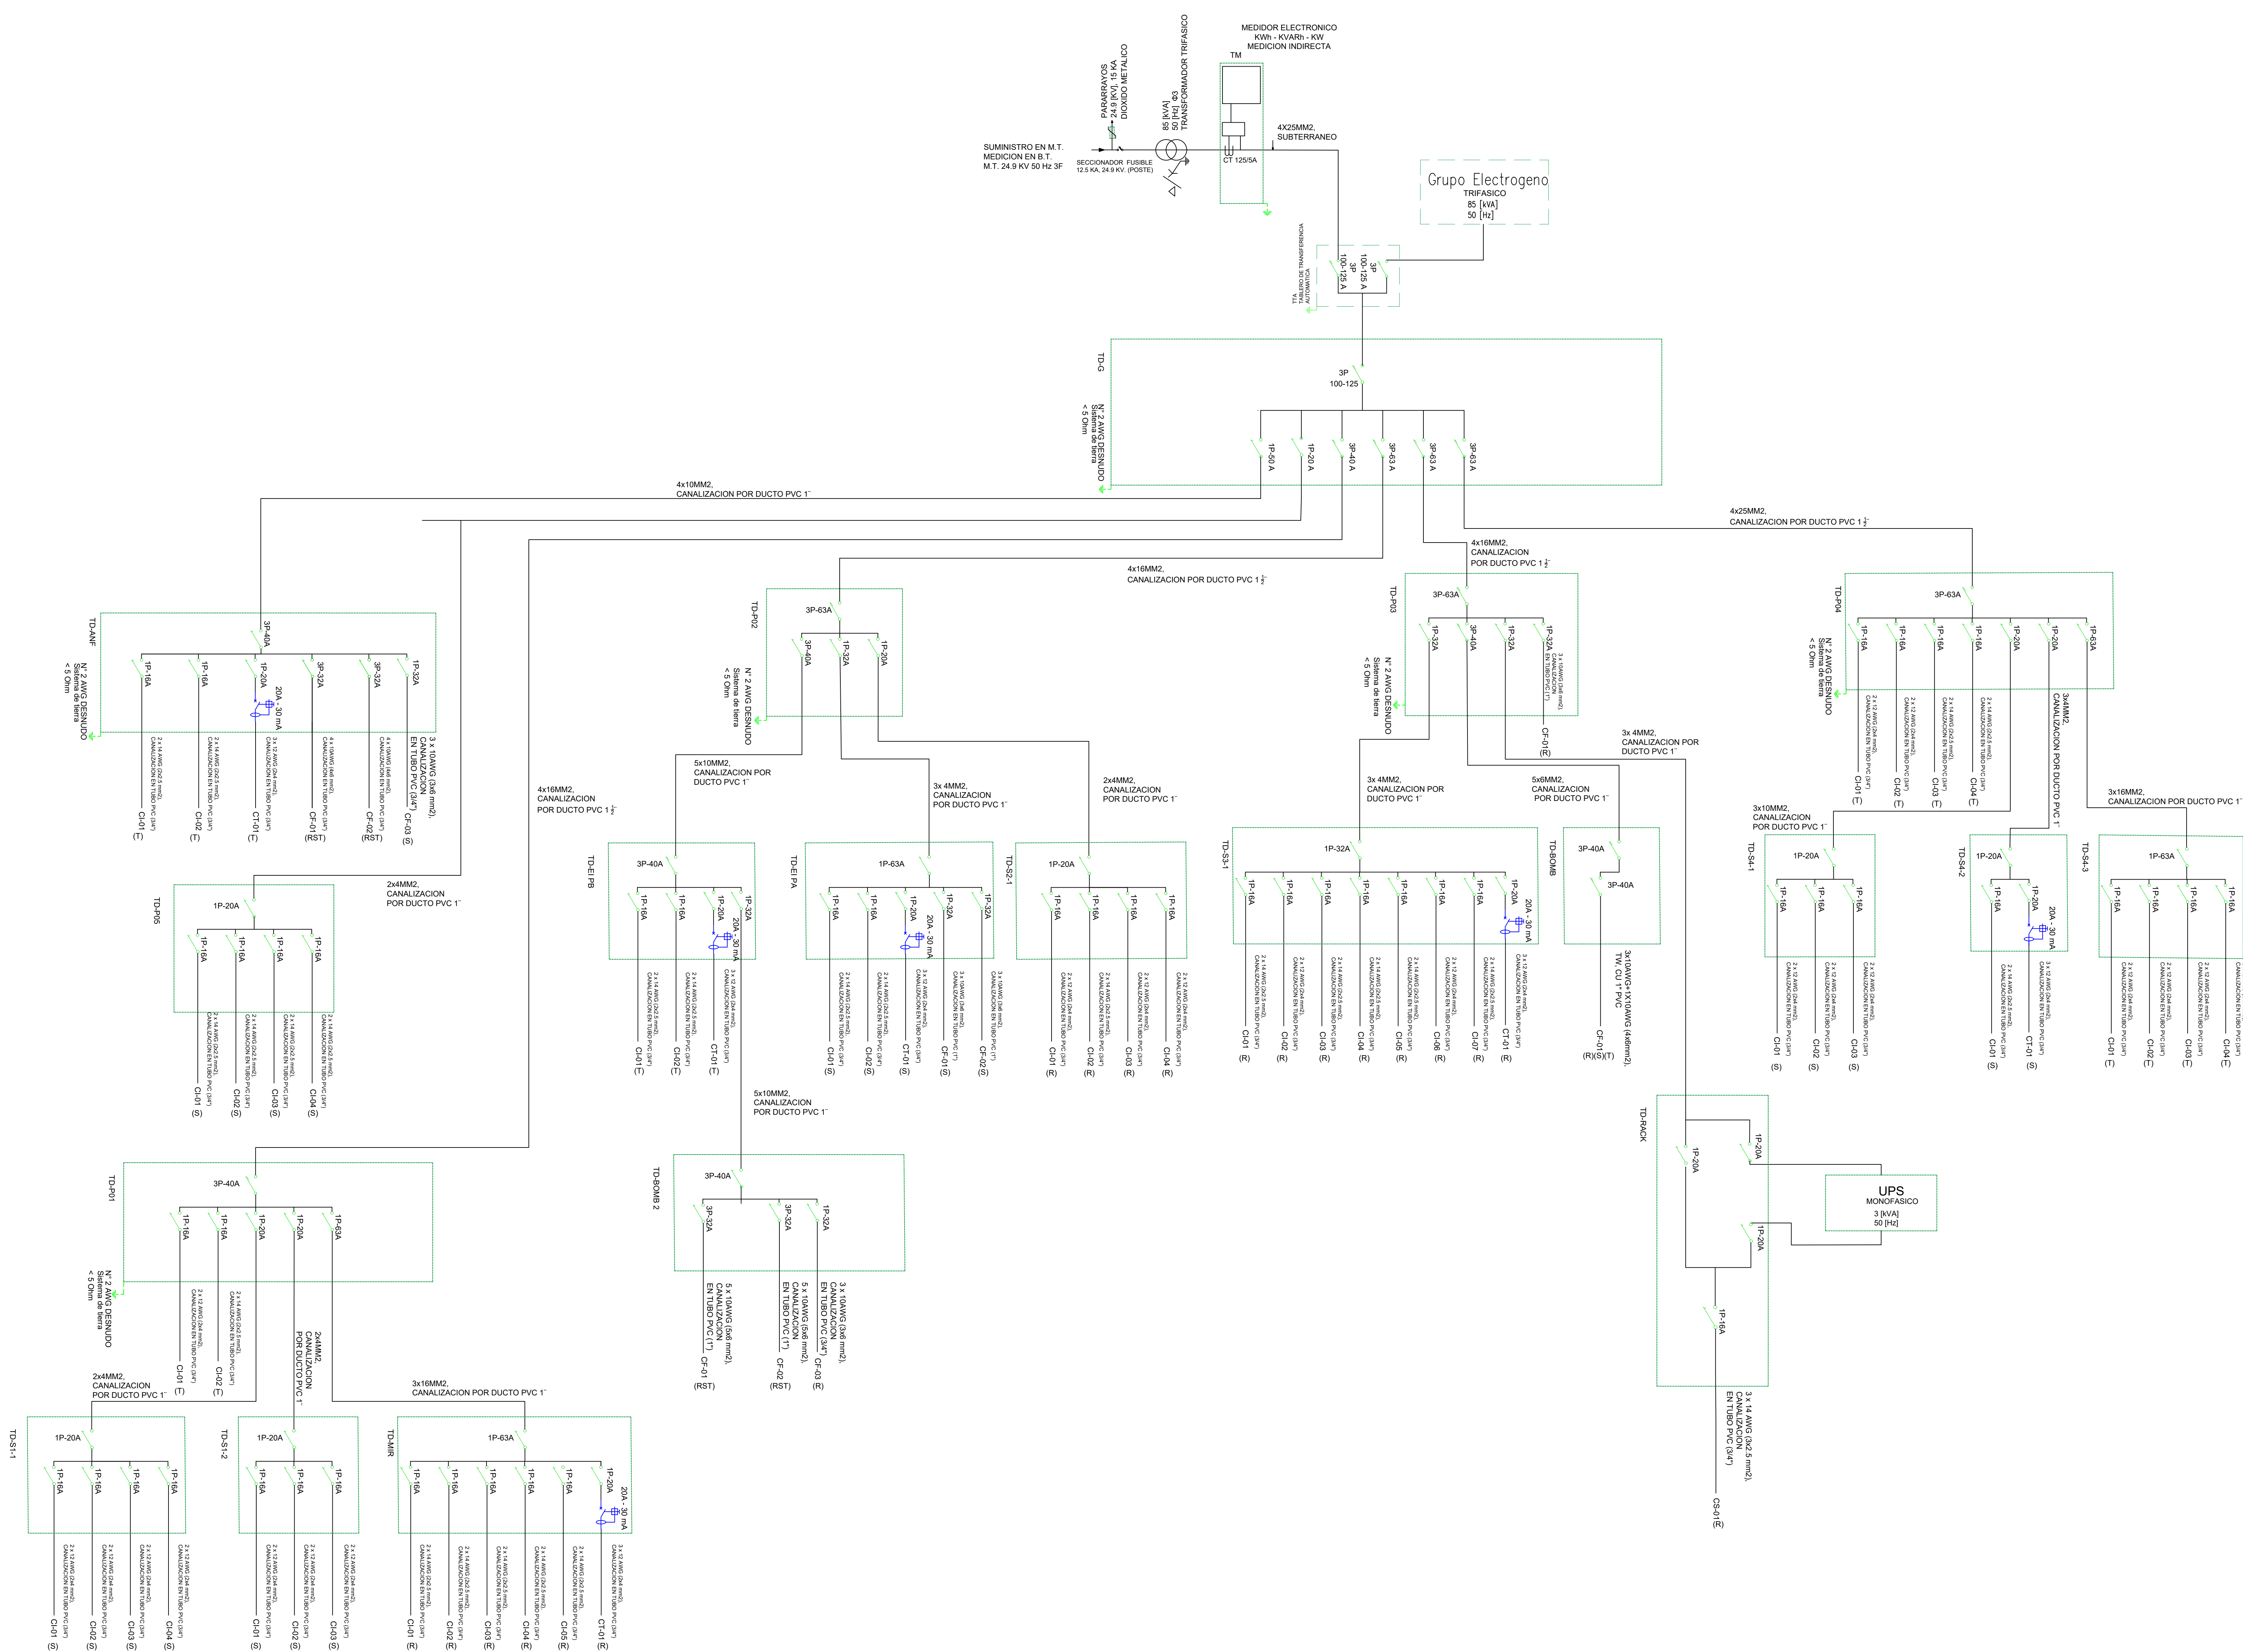

SIMBOLOGÍA	DESCRIPCIÓN
	Interruptor termomagnético tripolar
	Interruptor termomagnético monopolar
	Interruptor diferencial
	Transformador trifásico

DIAGRAMA UNIFILAR

PROPIETARIO (S):
GOBIERNO AUTÓNOMO MUNICIPAL DE COBILIA

UBICACION ESC: 1:1000

PROYECTO:
SERVICIO DE CONSULTORÍA POR PRODUCTO PARA EL ESTUDIO DE DISEÑO TÉCNICO DE PREVENCIÓN "CONSTRUCCIÓN PLAZA DEL BICENTENARIO DE BOUVIA EN EL MUNICIPIO DE COBILIA"

ZONA : MANANTIAL
AV/ CALLE : ENTRE AV/ TAHUAMANU ESQ. AV. LAS PALMAS ESQ. AV. 9 DE FEBRERO.
DISTRITO : 02 **PREDIO :** 001
MANZANO : 051 **CÓDIGO CAT. :** 02 051 001
FECHA : Cobija, Diciembre 2024

SUPERFICIE DE LOTE : 35089.57 m2
SUPERFICIE A CONSTRUIR : 852.78 m2
SUPERFICIE CUBIERTA ABIERTA (MIRADOR) : 1472.46 m2
ÁREAS A CONSTRUIR

N I V E L E S	RELEV.	CONST.	PARCIAL.
Nivel 1 (antiestructo)	+2.00	845.12	845.12 m2
Nivel 1 (Servicio P. pública)	+1.45	106.40	106.40 m2
Nivel 1 (Kiosco)	+1.75	95.14	95.14 m2
Nivel 1 (Puesto de seguridad 1)	-2.76	3.06	3.06 m2
Nivel 1 (Puesto de seguridad 1)	112.00	3.06	3.06 m2
Nivel 1 (Interculturalidad)	+4.00	571.42	571.42 m2
Nivel 2 (Interculturalidad)	+3.25	254.65	254.65 m2
TOTAL		826.07m2	852.78 m2
SUPERFICIE TOTAL CONSTRUIDA			1678.85 m2

TIPOLOGÍA DE ZONA:
Z.1

ESCALA:
INDICADAS

Nº LAMINA:
ELT32

SELO DE APROBACION G.A.M.C.

FIRMA DEL PROPIETARIO

RESPONSABLE
PLAN REGULADOR GAMC

JEFE
PLAN REGULADOR GAMC

DIRECTOR
PLAN REGULADOR GAMC

SELO DE ENTE COLEGIADO

ING. JOSÉ ANTONIO VELARDE NAVARRO
SELO